


NEW

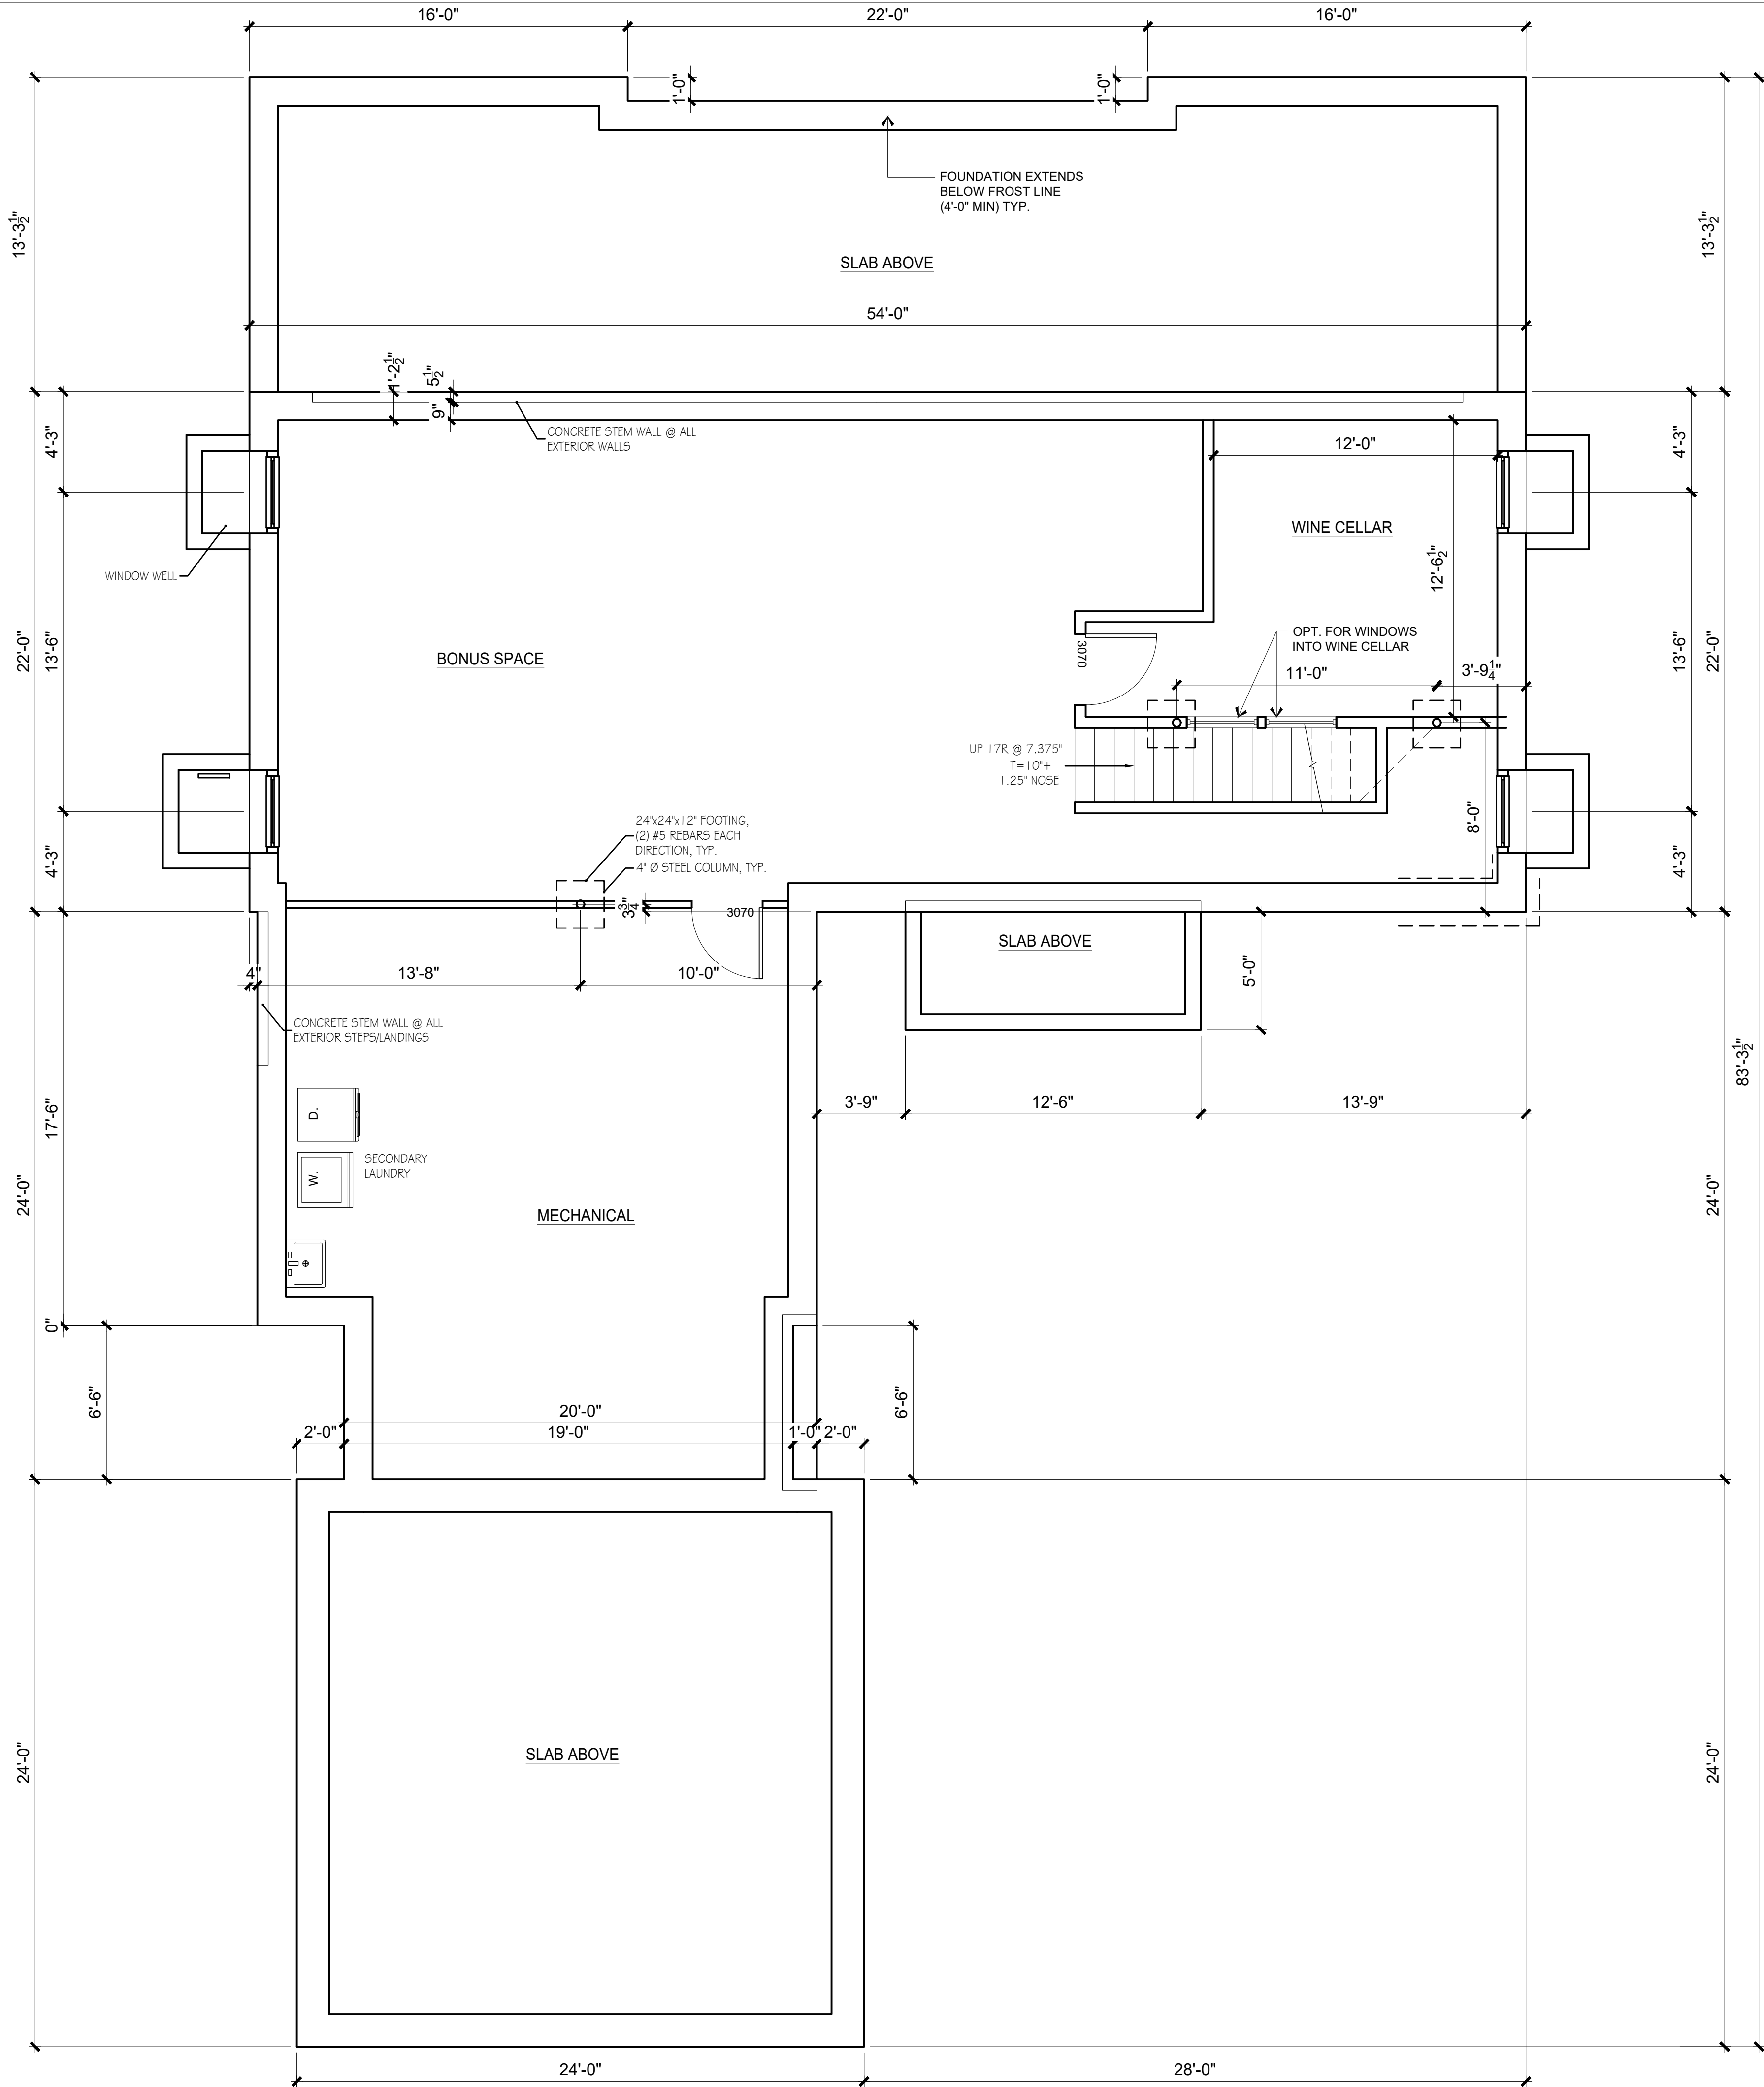

PROPOSED NEW CONSTRUCTION FOR:

CLIFTON CROSSING
7 WARE LANE
MARBLEHEAD, MA

FL REG. AR95938
NY REG. 031148

REVISIONS:


DATE:
3/11/2025
SCALE:
1/4" = 1'-0"

A-201

BASEMENT PLAN

917 647-2039

NEW

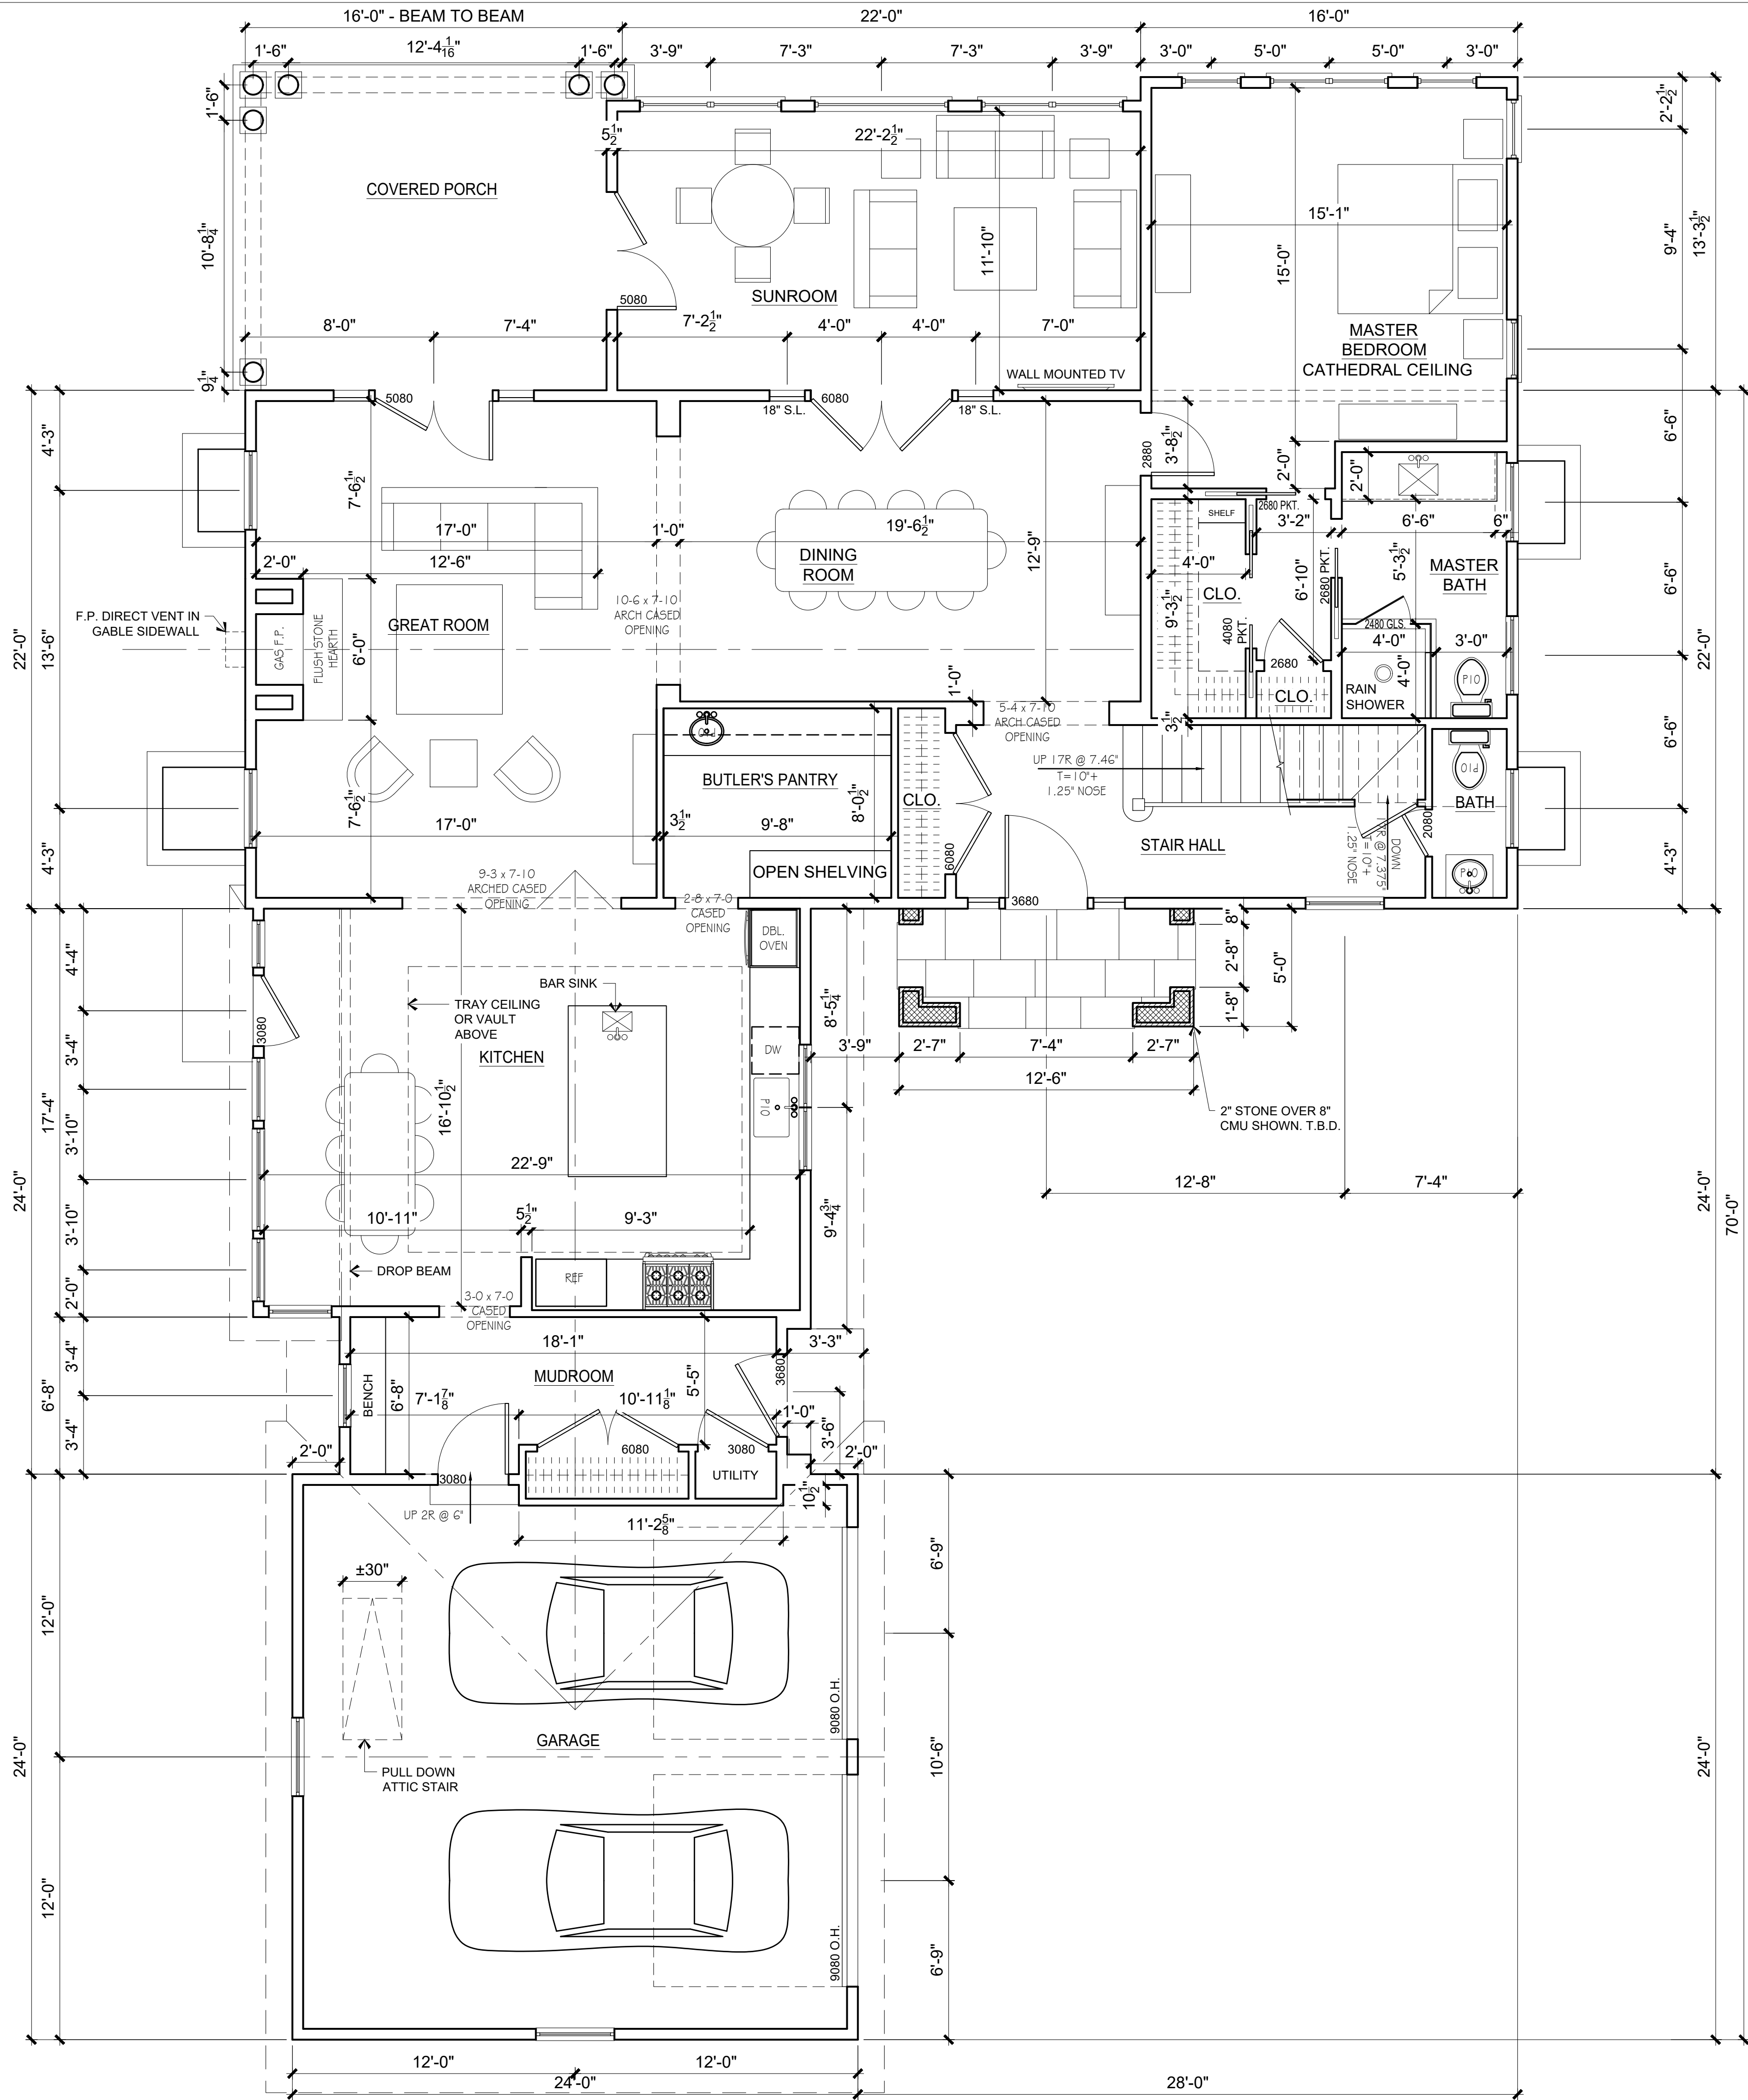

AREA CALCULATIONS		
ORIGINAL DESIGN		
FIRST FLOOR		1,675 S.F.
SECOND FLOOR		2,150 S.F.
TOTAL		3,825 S.F.
NEW DESIGN		
FIRST FLOOR (540 S.F. ADDED)		2,215 S.F.
490 S.F. ADD FOR MASTER BEDROOM/SUNROOM		
30 S.F. ADD FOR KITCHEN		
20 S.F. ADD FOR MUDROOM		
SECOND FLOOR (1,040 S.F. REMOVED)		1,155 S.F.
TOTAL		3,370 S.F.
455 S.F. REMOVED		
+ 205 S.F. COVERED PORCH ADDED		
*GARAGE SIZE UNCHANGED		576 S.F.

NOTE: INTERIOR DOOR HEIGHTS T.B.D.

PROPOSED NEW CONSTRUCTION FOR:
CLIFTON CROSSING
7 WARE LANE
MARBLEHEAD, MA


FL REG. AR95938
NY REG. 031148

REVISIONS:

DATE:
3/11/2025
SCALE:
1/4" = 1'-0"

A-211
1st FLOOR PLAN

NEW

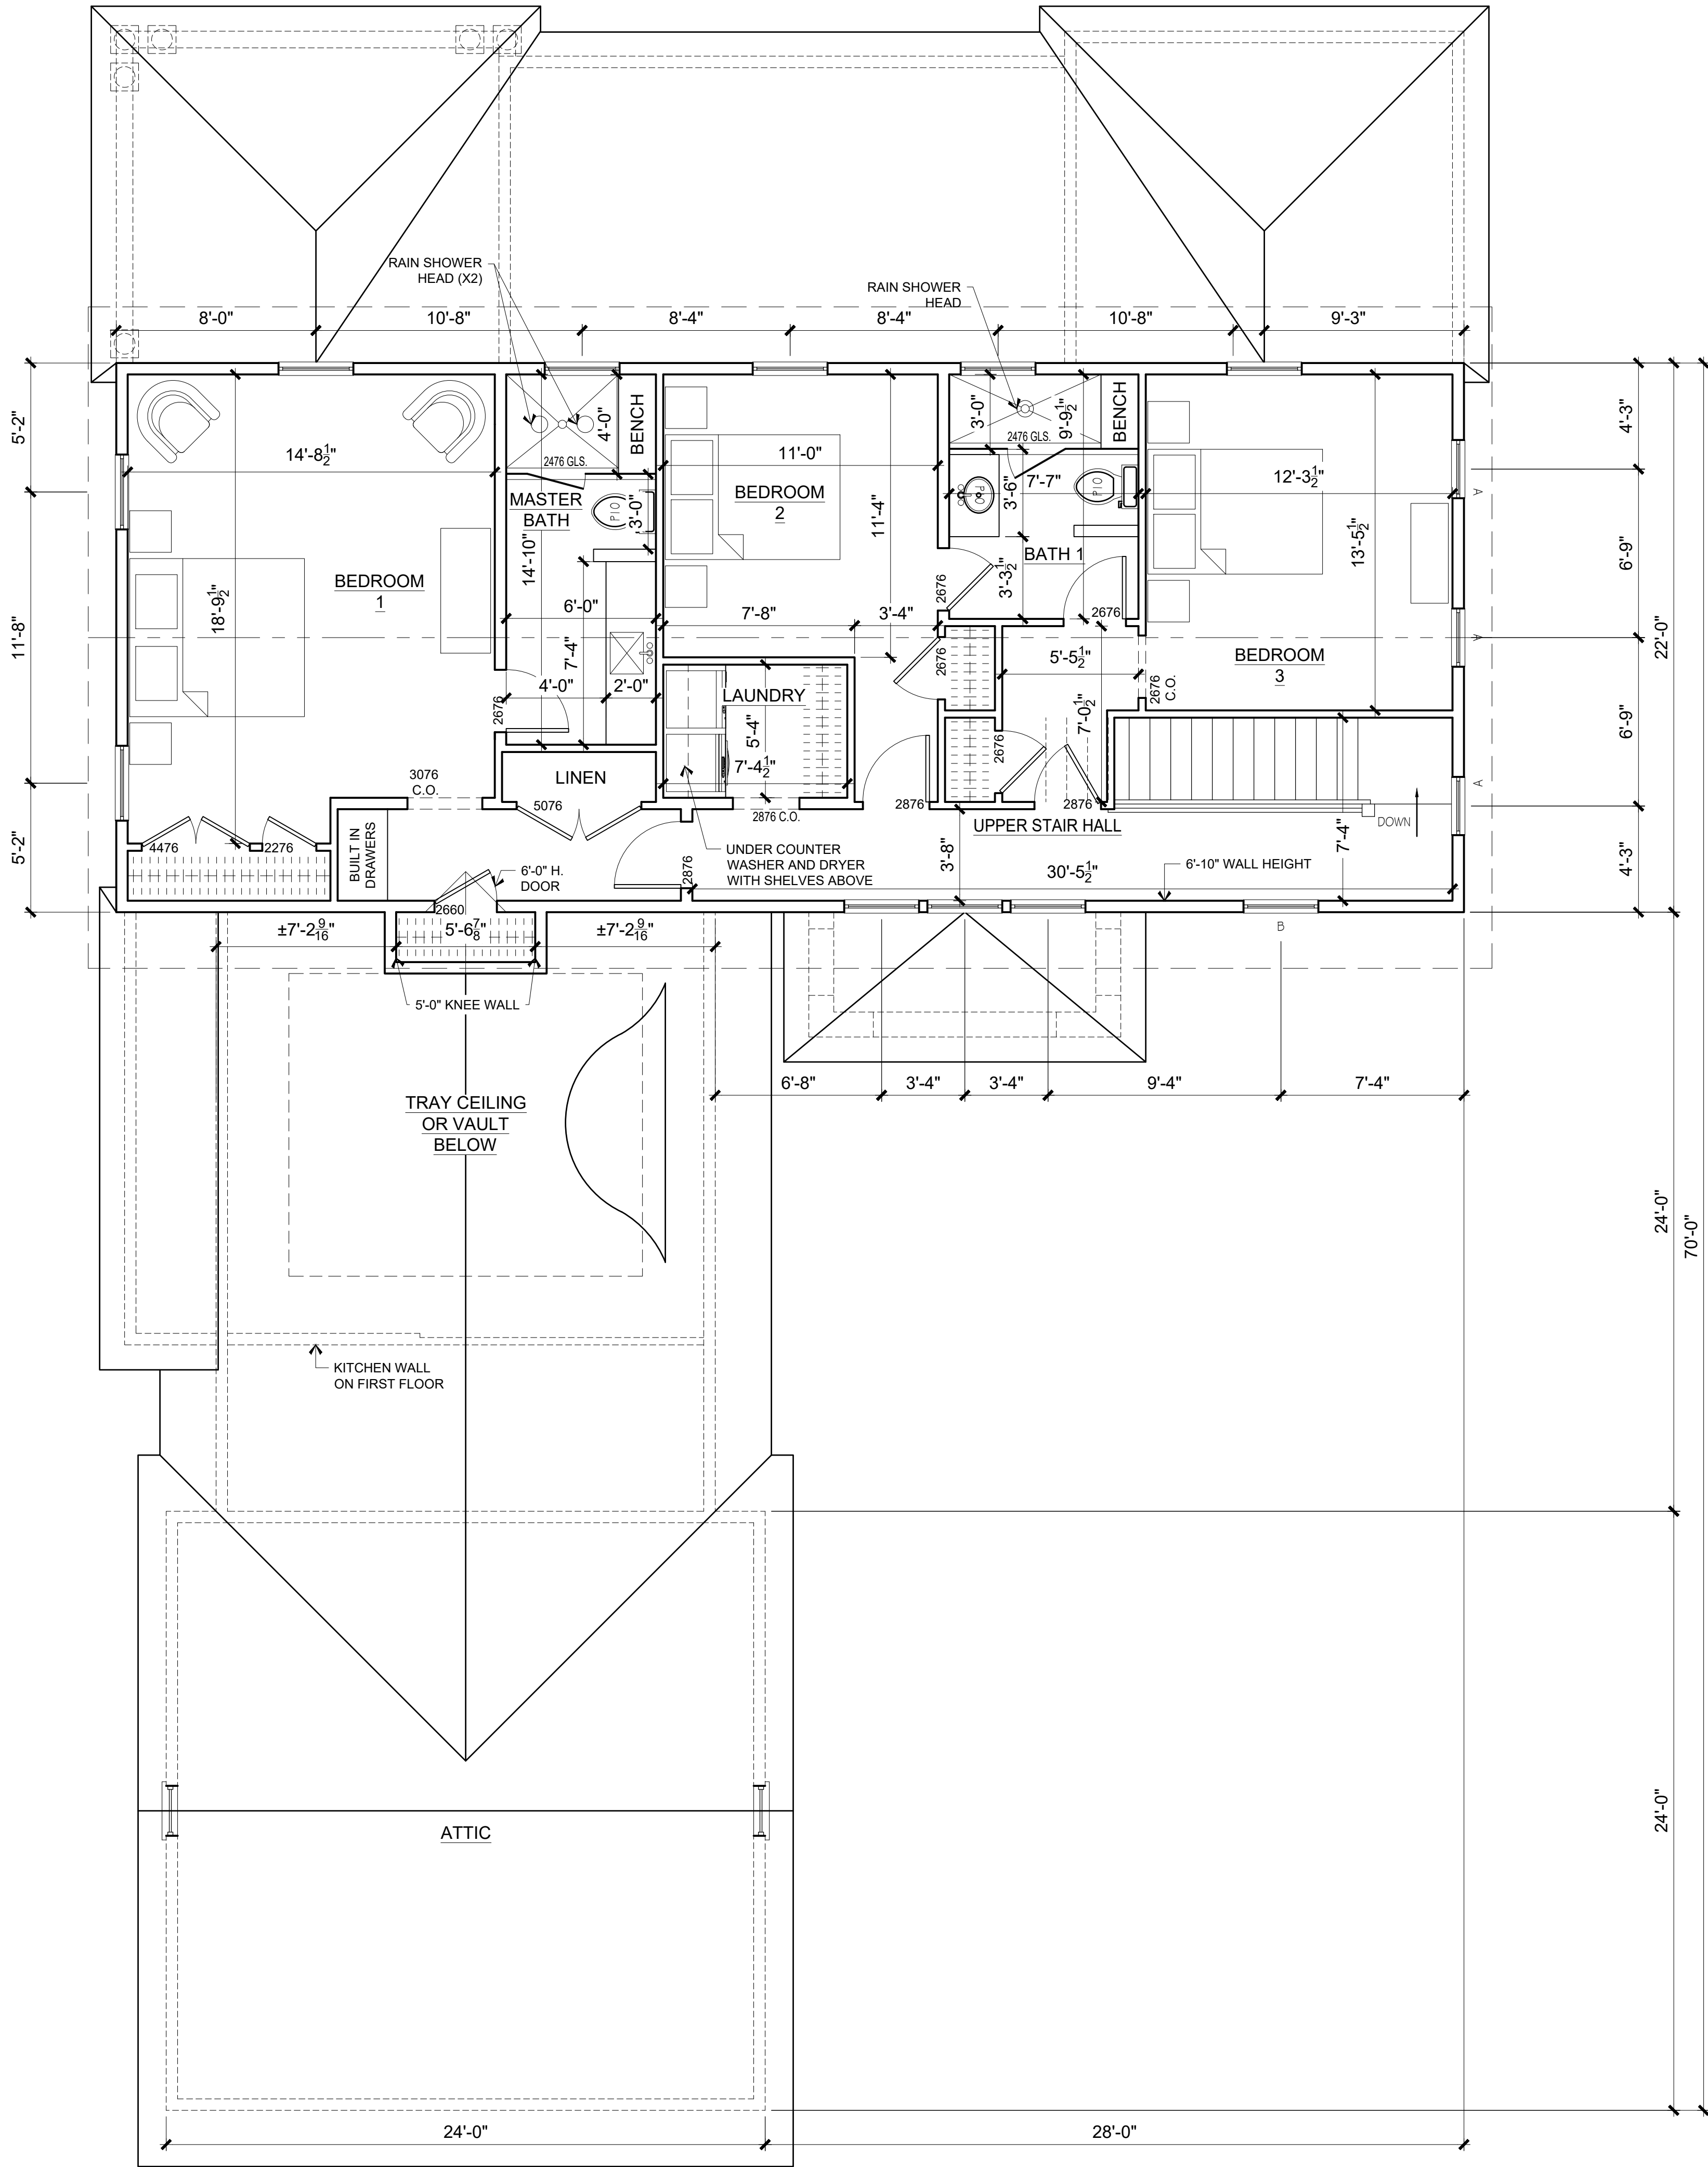

AREA CALCULATIONS	
ORIGINAL DESIGN	
FIRST FLOOR	1,675 S.F.
SECOND FLOOR	2,150 S.F.
TOTAL	3,825 S.F.
NEW DESIGN	
FIRST FLOOR (540 S.F. ADDED)	2,215 S.F.
490 S.F. ADD FOR MASTER BEDROOM/SUNROOM	
30 S.F. ADD FOR KITCHEN	
20 S.F. ADD FOR MUDROOM	
SECOND FLOOR (1,040 S.F. REMOVED)	1,155 S.F.
TOTAL	3,370 S.F.
455 S.F. REMOVED	
+ 205 S.F. COVERED PORCH ADDED	
*GARAGE SIZE UNCHANGED	576 S.F.

NOTE: INTERIOR DOOR HEIGHTS T.B.D.


PROPOSED NEW CONSTRUCTION FOR:
CLIFTON CROSSING
7 WARE LANE
MARBLEHEAD, MA

FL REG. AR95938
NY REG. 031148

REVISIONS:

DATE:
3/11/2025
SCALE:
1/4" = 1'-0"

A-221
2nd FLOOR PLAN

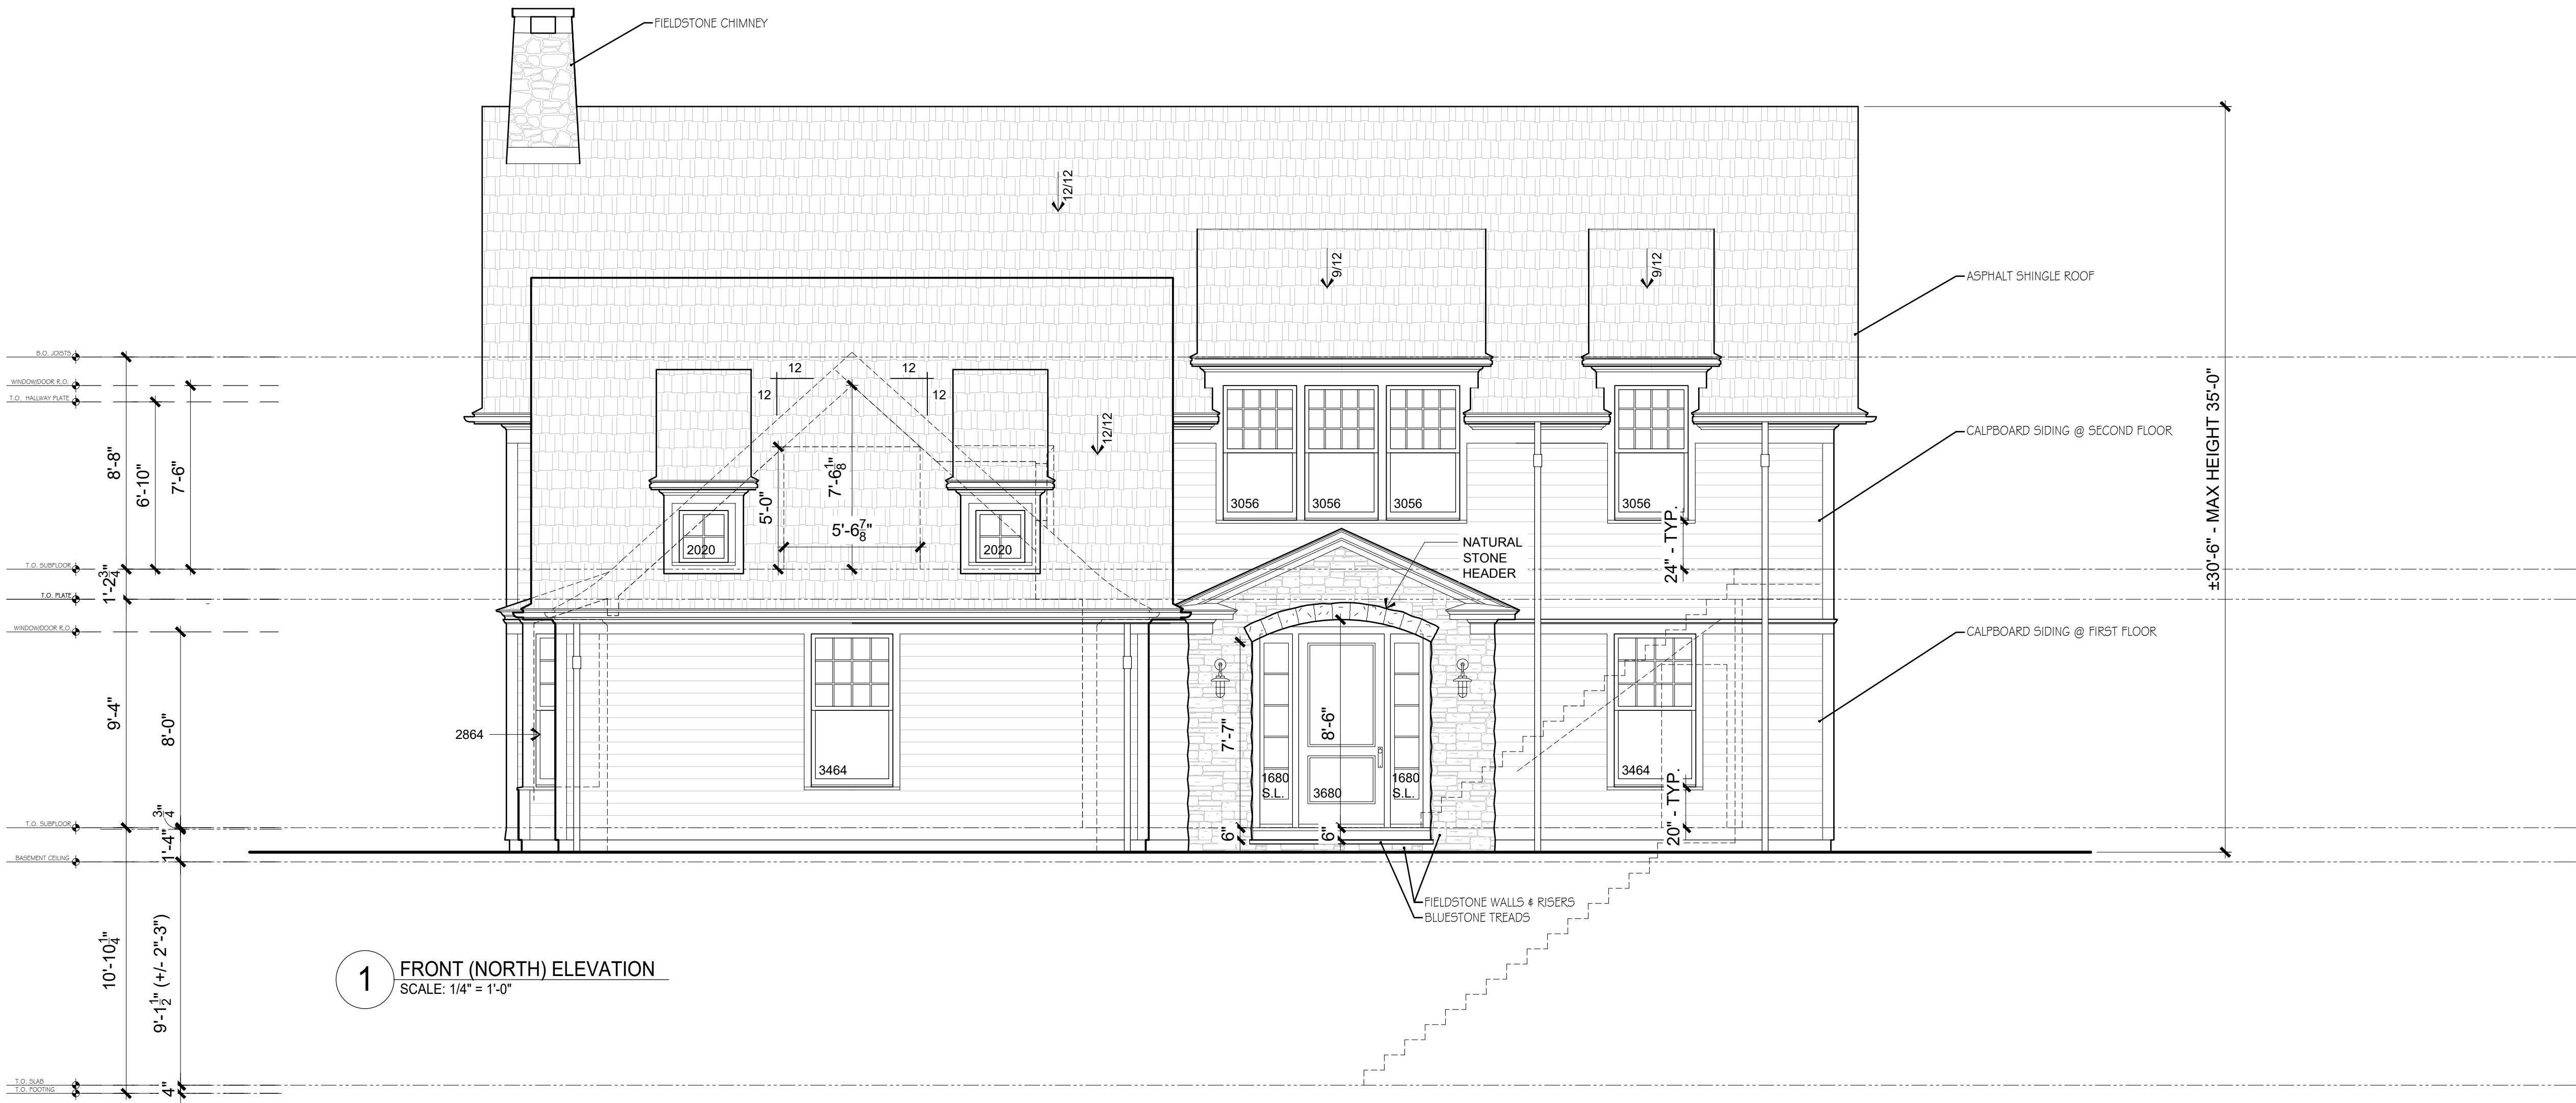

1 FRONT (NORTH) ELEVATION
SCALE: 1/4" = 1'-0"



2 FRONT (NORTH) ELEVATION
SCALE: 1/4" = 1'-0"

NEW

ORIGINAL

PROPOSED NEW CONSTRUCTION FOR:

CLIFTON CROSSING
7 WARE LANE
MARBLEHEAD, MA

FL REG. AR95938
NY REG. 031148

REVISIONS:

DATE:
3/11/2025
SCALE:
1/4" = 1'-0"

A-401
EXTERIOR ELEVATIONS

917 647-2039



1 RIGHT (EAST) ELEVATION
SCALE: 1/4" = 1'-0"

ORIGINAL



2 RIGHT (EAST) ELEVATION
SCALE: 1/4" = 1'-0"

NEW

PROPOSED NEW CONSTRUCTION FOR:

CLIFTON CROSSING
7 WARE LANE
MARBLEHEAD, MA

FL REG. AR95938
NY REG. 031148

REVISIONS:

DATE:
3/11/2025
SCALE:
1/4" = 1'-0"

A-402

EXTERIOR ELEVATIONS

917 647-2039



1 REAR (SOUTH) ELEVATION
SCALE: 1/4" = 1'-0"



2 REAR (SOUTH) ELEVATION
SCALE: 1/4" = 1'-0"

NEW

ORIGINAL

PROPOSED NEW CONSTRUCTION FOR:

CLIFTON CROSSING
7 WARE LANE
MARBLEHEAD, MA

FL REG. AR95938
NY REG. 031148

REVISIONS:

DATE:
3/11/2025
SCALE:
1/4" = 1'-0"

A-403

EXTERIOR ELEVATIONS

917 647-2039



1 LEFT (WEST) ELEVATION
SCALE: 1/4" = 1'-0"



2 LEFT (WEST) ELEVATION
SCALE: 1/4" = 1'-0"

NEW

ORIGINAL

PROPOSED NEW CONSTRUCTION FOR:
CLIFTON CROSSING
7 WARE LANE
MARBLEHEAD, MA

FL REG. AR95938
NY REG. 031148

REVISIONS:

DATE:
3/11/2025
SCALE:
1/4" = 1'-0"

A-404
EXTERIOR ELEVATIONS