


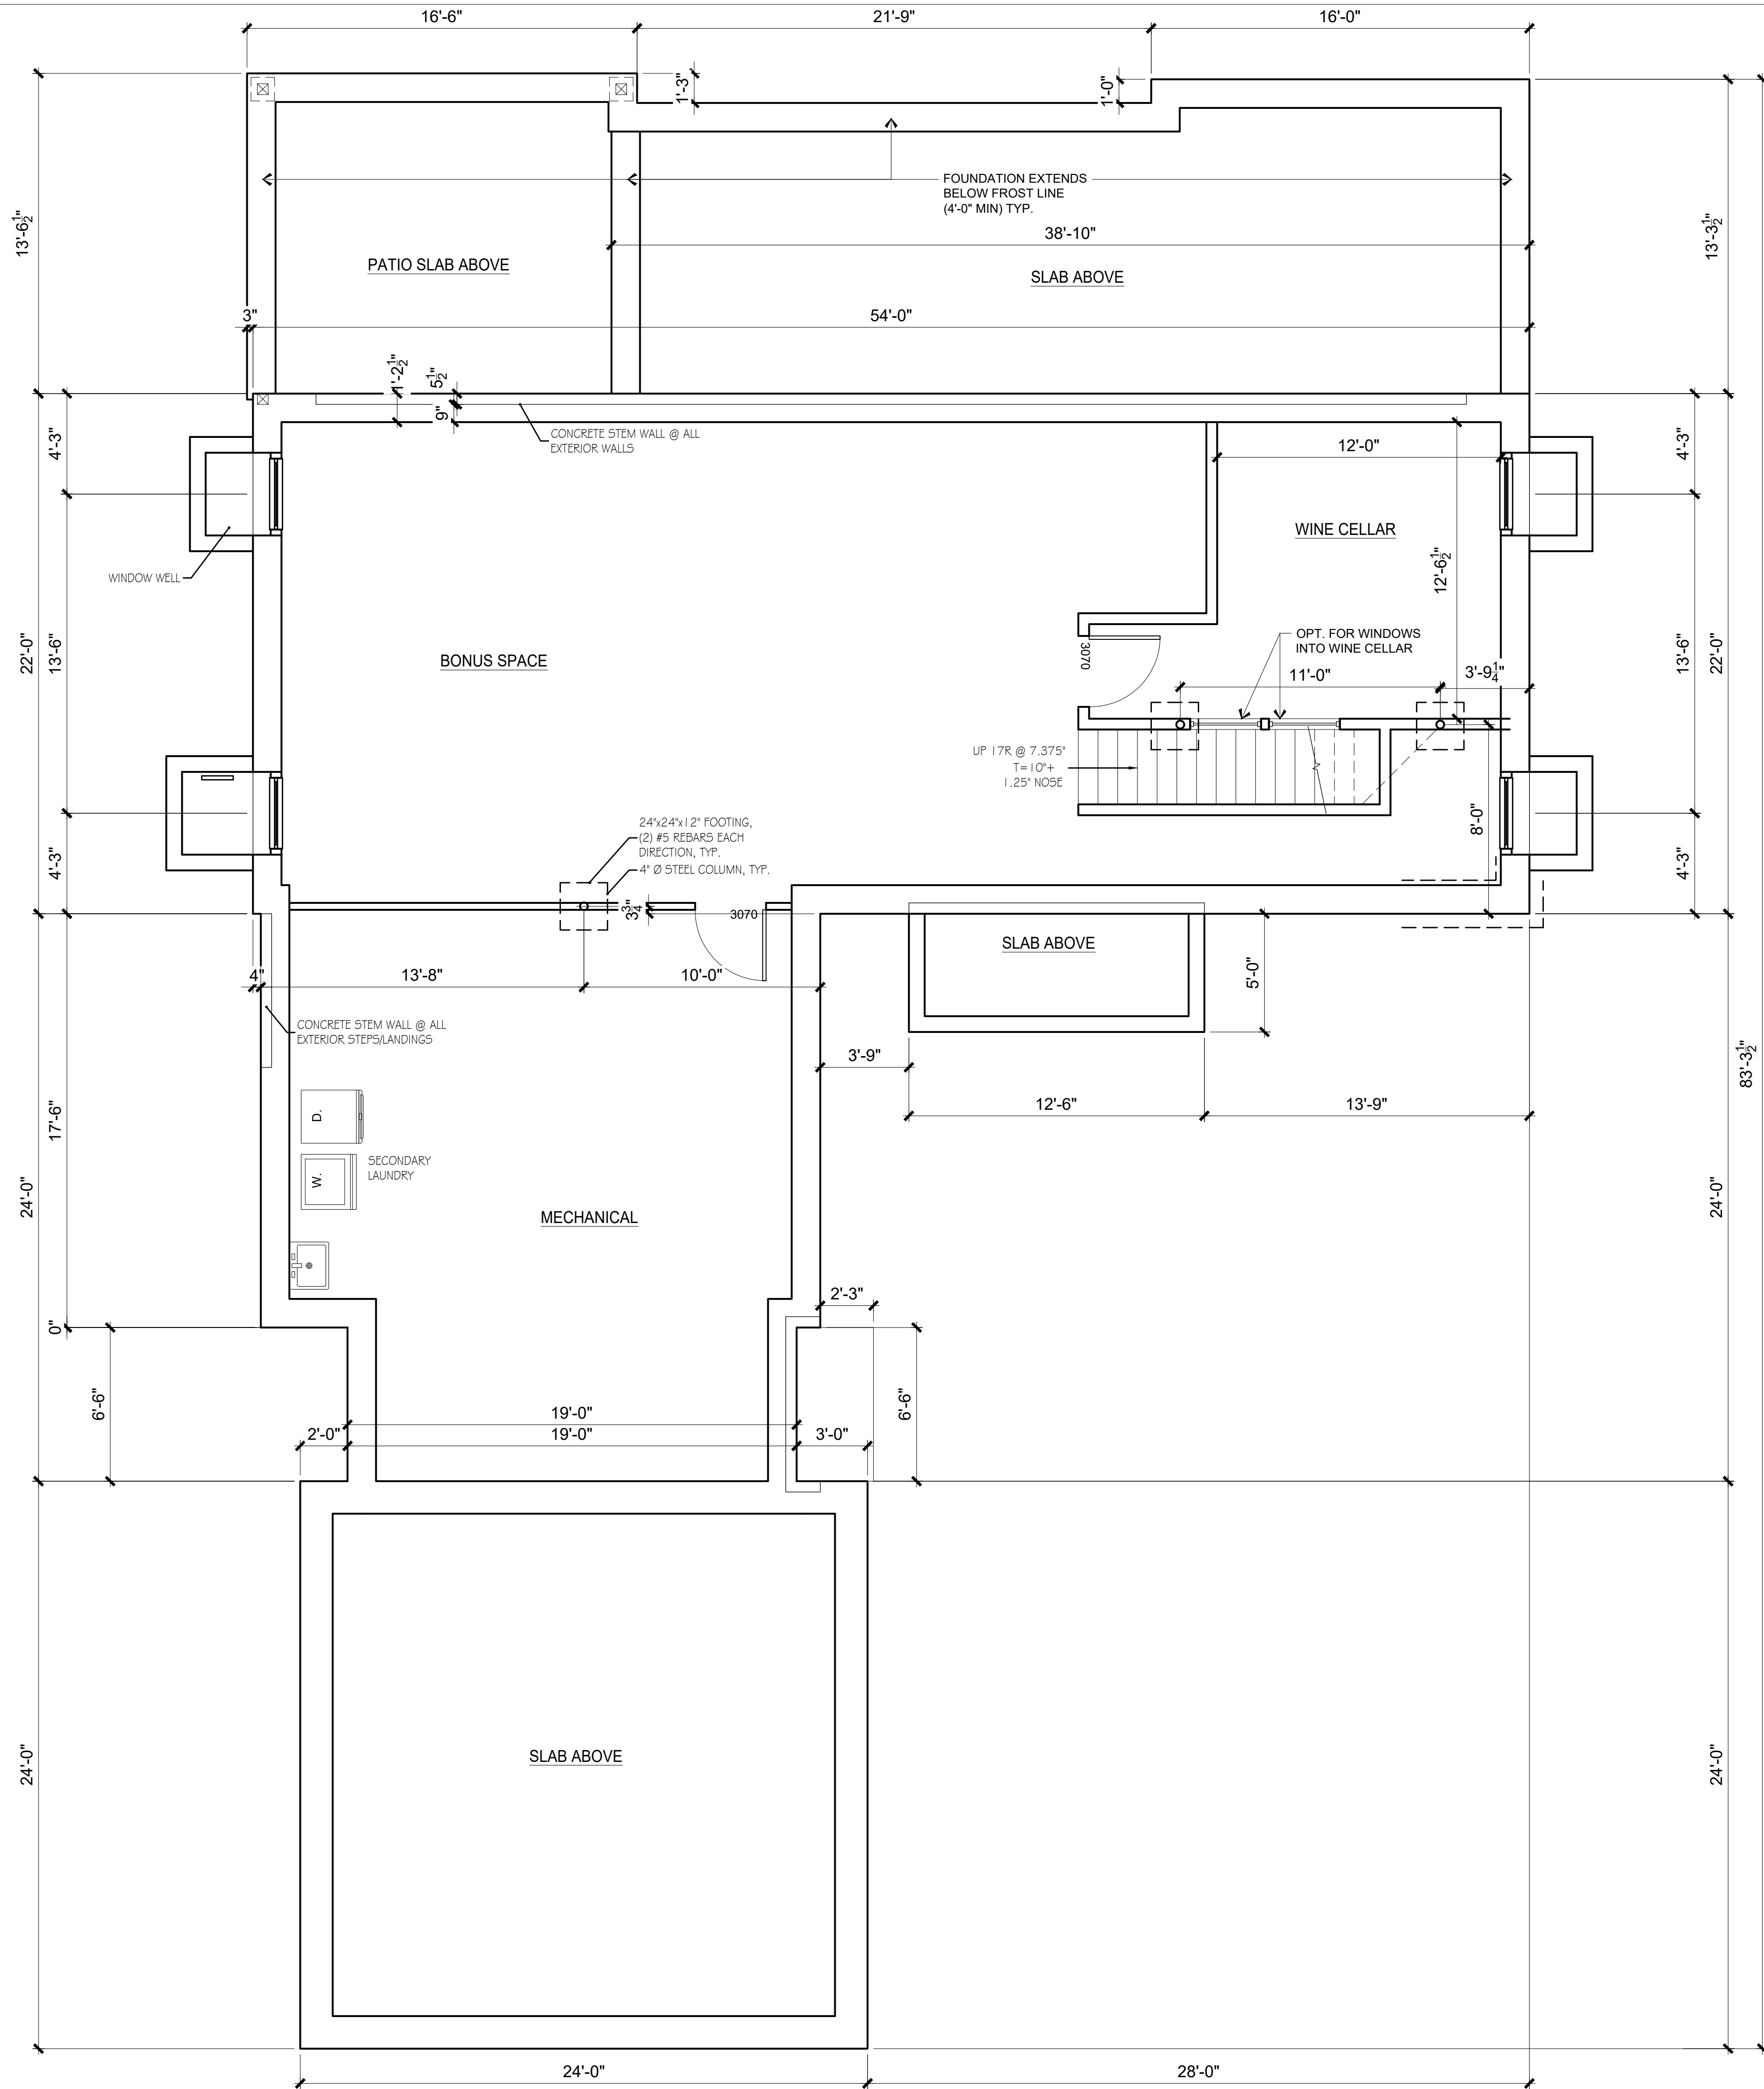

PROPOSED NEW CONSTRUCTION FOR:

**CLIFTON CROSSING**  
7 WARE LANE  
MARBLEHEAD, MA

FL REG. AR95938  
NY REG. 031148


REVISIONS:

DATE:  
5/24/2025  
SCALE:  
1/4" = 1'-0"

**A-201**

BASEMENT PLAN



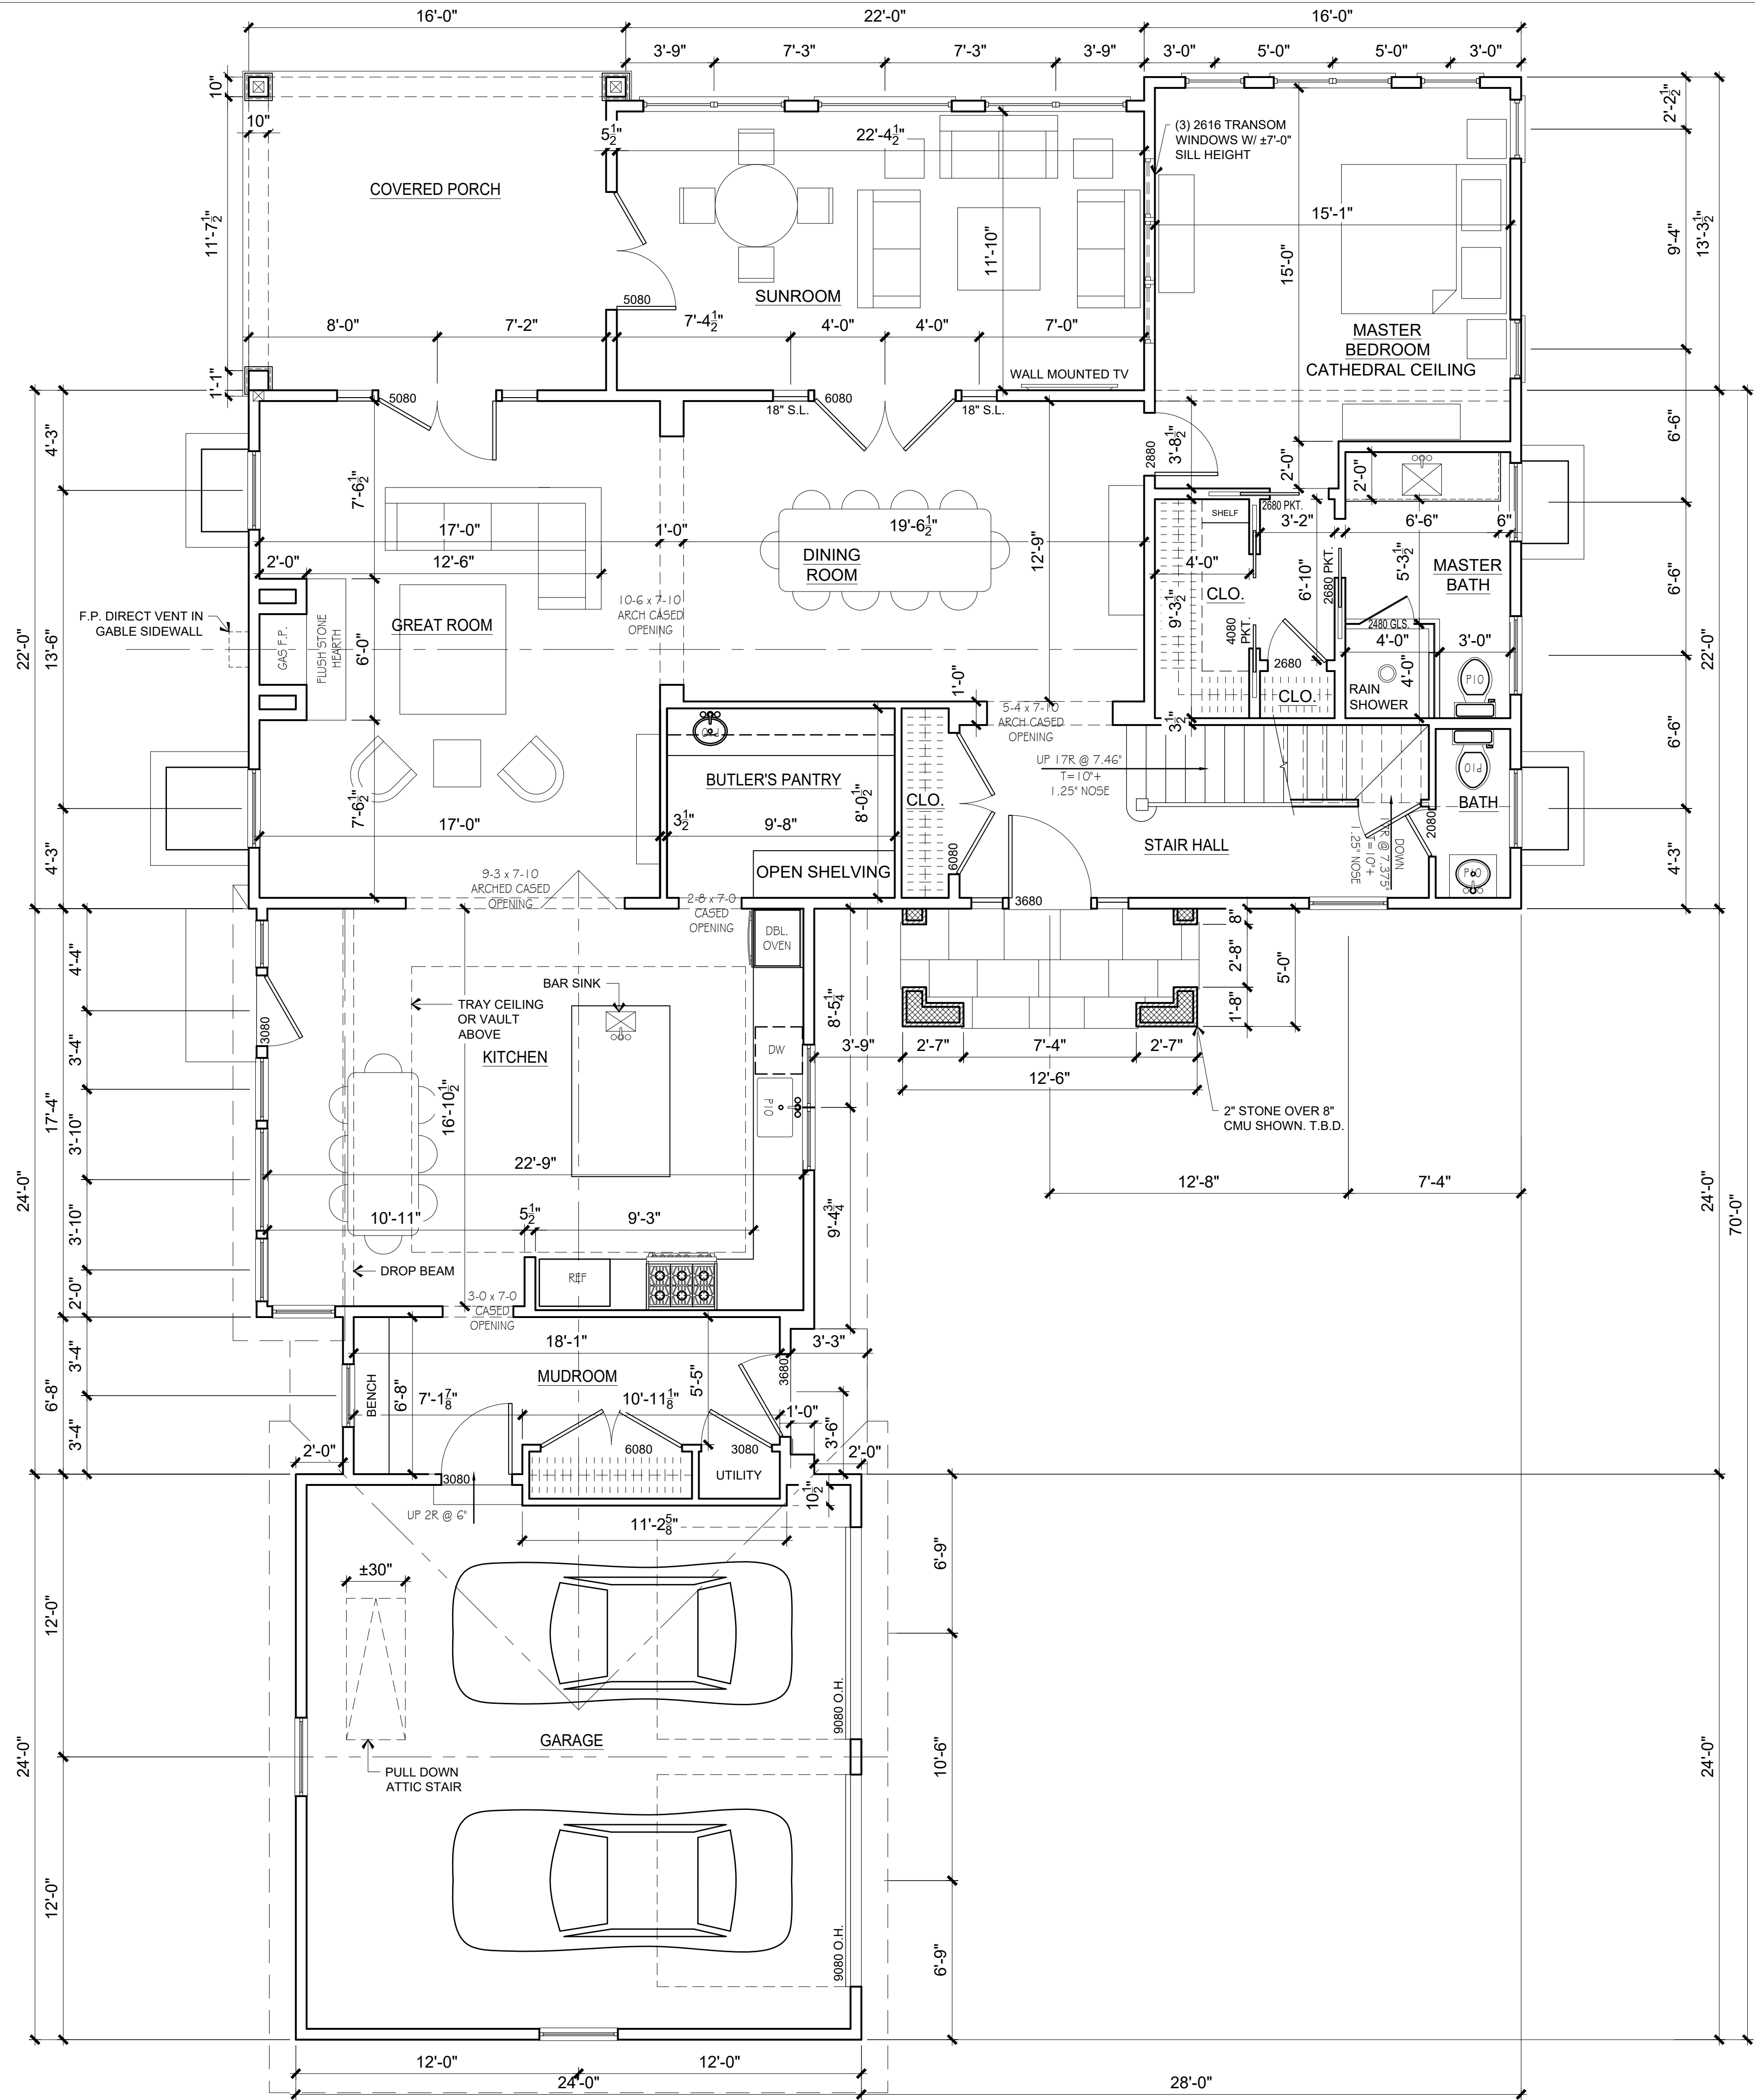

| AREA CALCULATIONS          |                   |
|----------------------------|-------------------|
| <b>CONDITIONED SPACE</b>   |                   |
| FIRST FLOOR                | 2,215 S.F.        |
| SECOND FLOOR               | 1,155 S.F.        |
| <b>TOTAL</b>               | <b>3,370 S.F.</b> |
| <b>UNCONDITIONED SPACE</b> |                   |
| FRONT COVERED PORCH        | 63 S.F.           |
| REAR COVERED PORCH         | 205 S.F.          |
| GARAGE                     | 576 S.F.          |

NOTE: INTERIOR DOOR HEIGHTS T.B.D.

PROPOSED NEW CONSTRUCTION FOR:

CLIFTON CROSSING  
7 WARE LANE  
MARBLEHEAD, MA

FL REG. AR95938  
NY REG. 031148


|            |
|------------|
| REVISIONS: |
|            |
|            |
|            |
|            |
|            |

DATE:  
5/24/2025  
SCALE:  
1/4" = 1'-0"

A-211

1st FLOOR PLAN



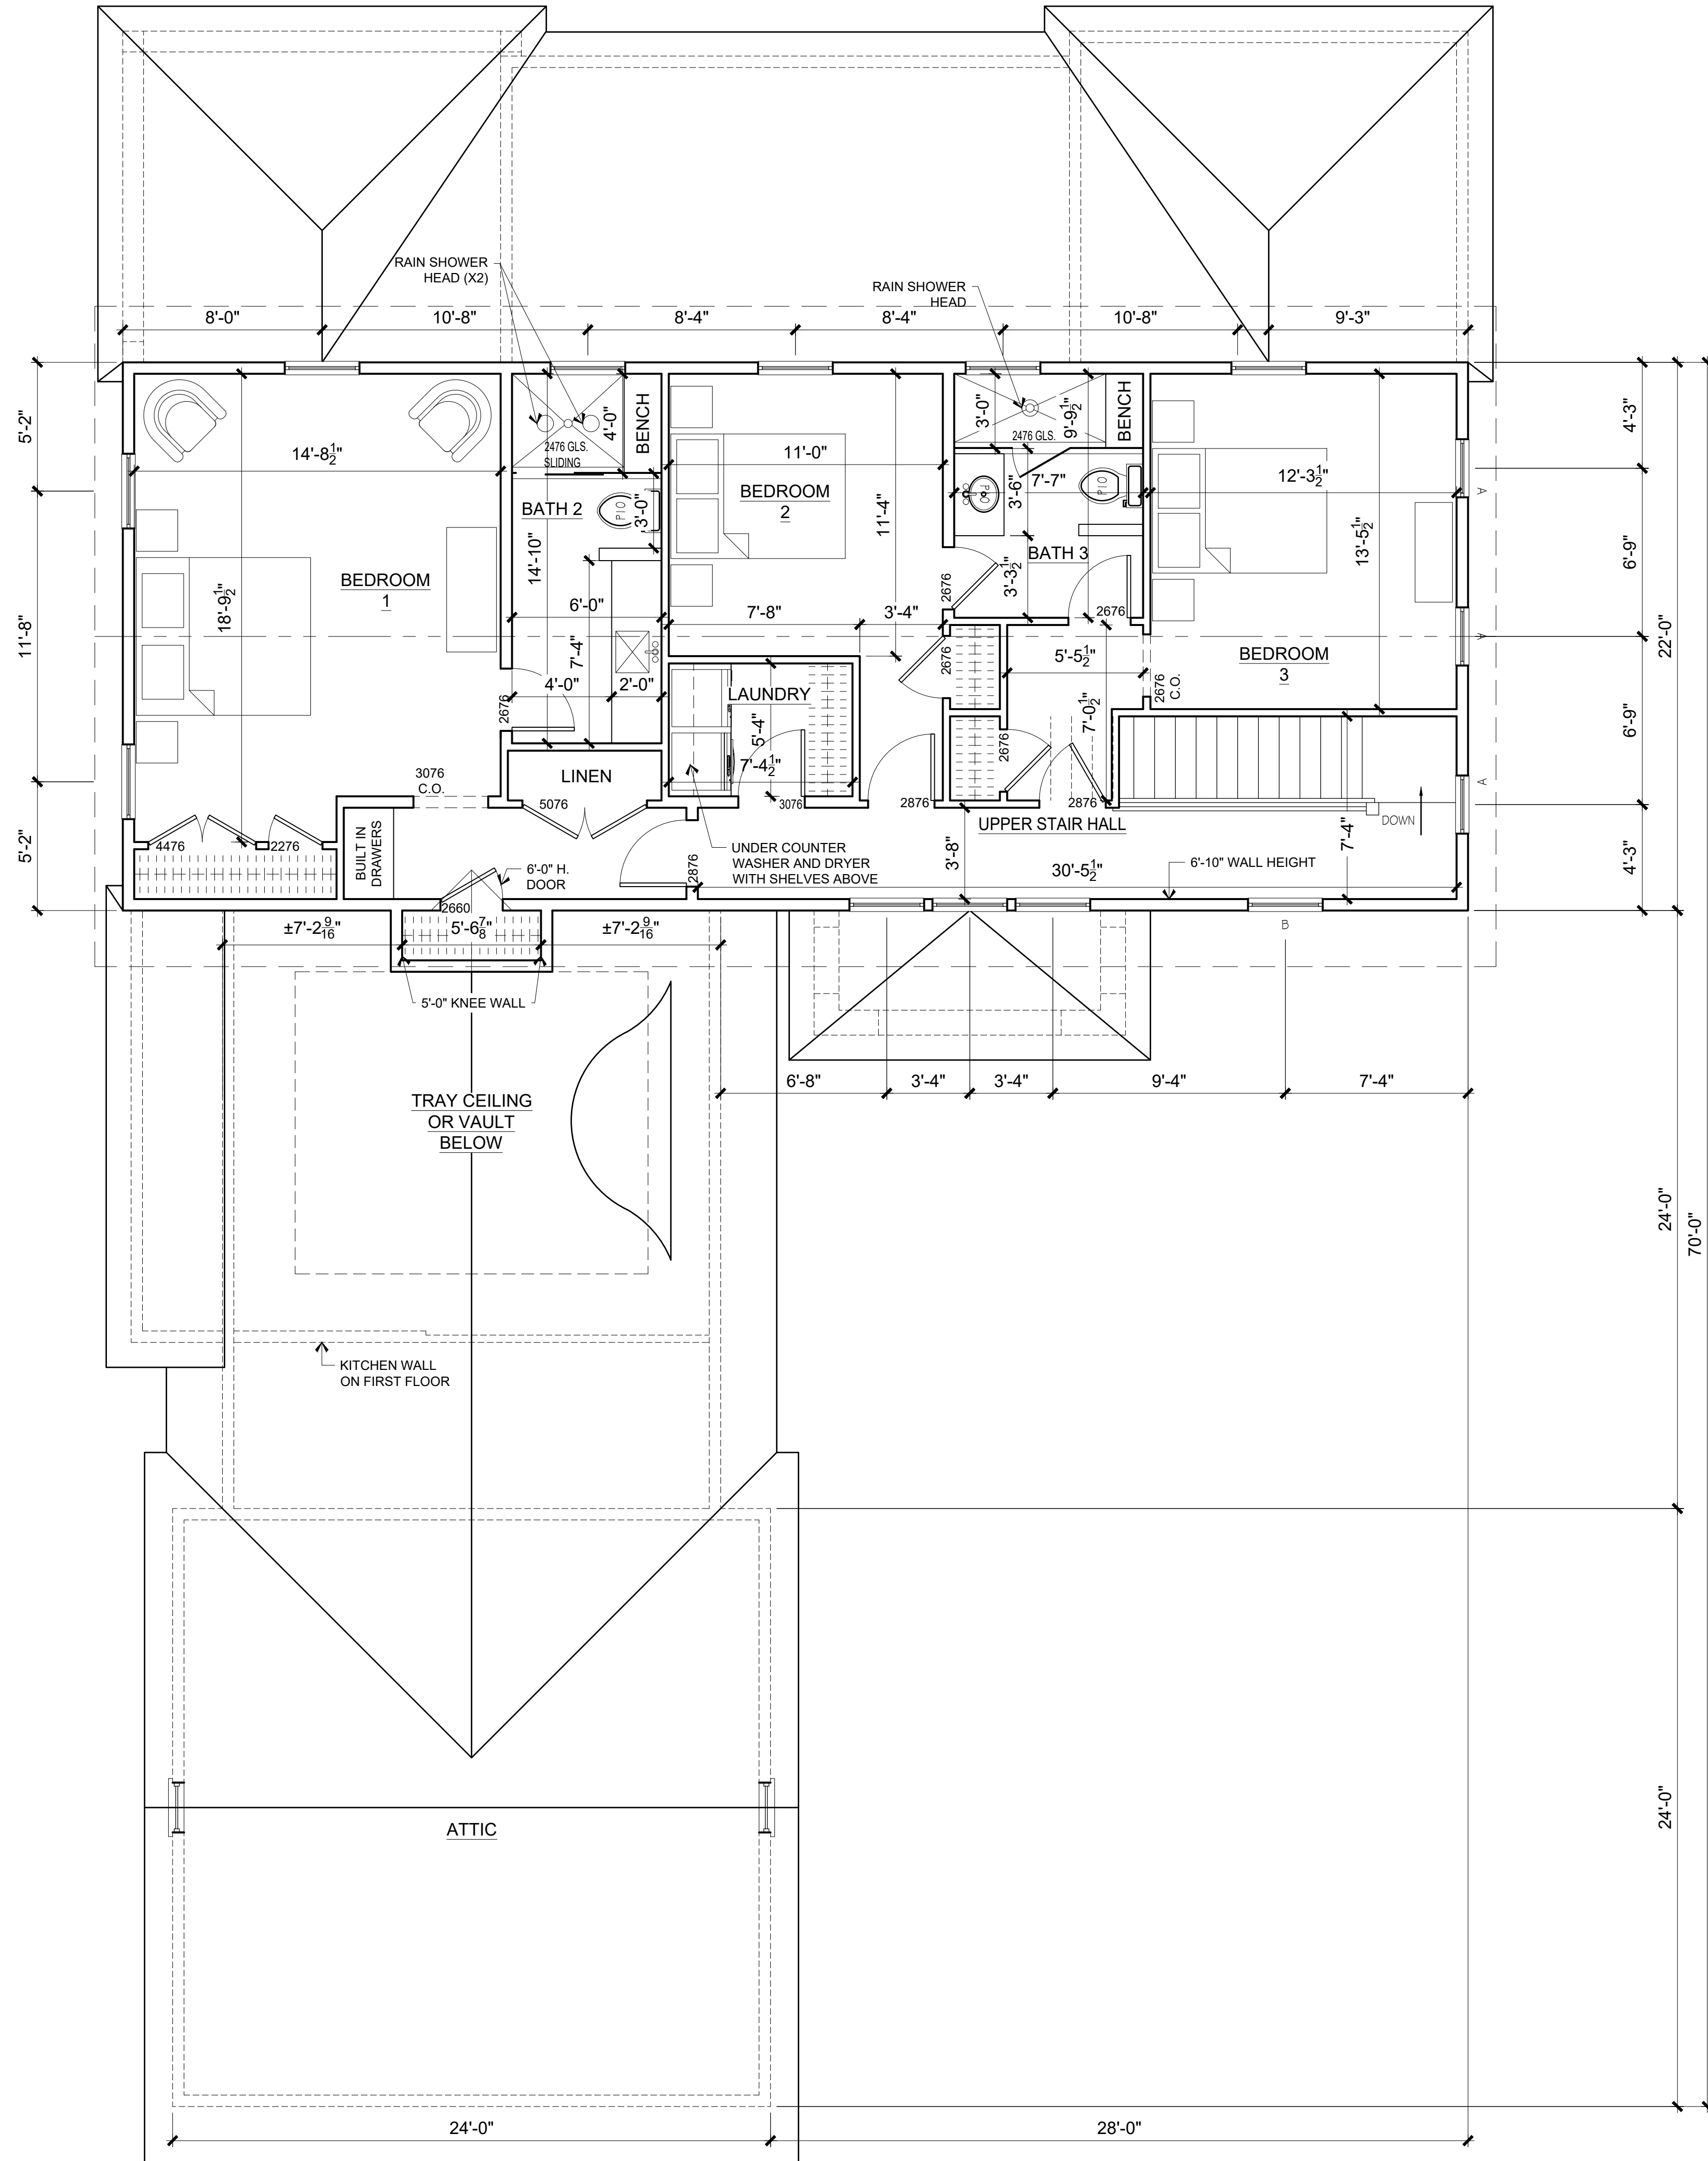

| AREA CALCULATIONS          |                   |
|----------------------------|-------------------|
| <b>CONDITIONED SPACE</b>   |                   |
| FIRST FLOOR                | 2,215 S.F.        |
| SECOND FLOOR               | 1,155 S.F.        |
| <b>TOTAL</b>               | <b>3,370 S.F.</b> |
| <b>UNCONDITIONED SPACE</b> |                   |
| FRONT COVERED PORCH        | 63 S.F.           |
| REAR COVERED PORCH         | 205 S.F.          |
| GARAGE                     | 576 S.F.          |

NOTE: INTERIOR DOOR HEIGHTS T.B.D.

PROPOSED NEW CONSTRUCTION FOR:

CLIFTON CROSSING  
7 WARE LANE  
MARBLEHEAD, MA

FL REG. AR95938  
NY REG. 031148


REVISIONS:

DATE:  
5/24/2025  
SCALE:  
1/4" = 1'-0"

A-221

2nd FLOOR PLAN



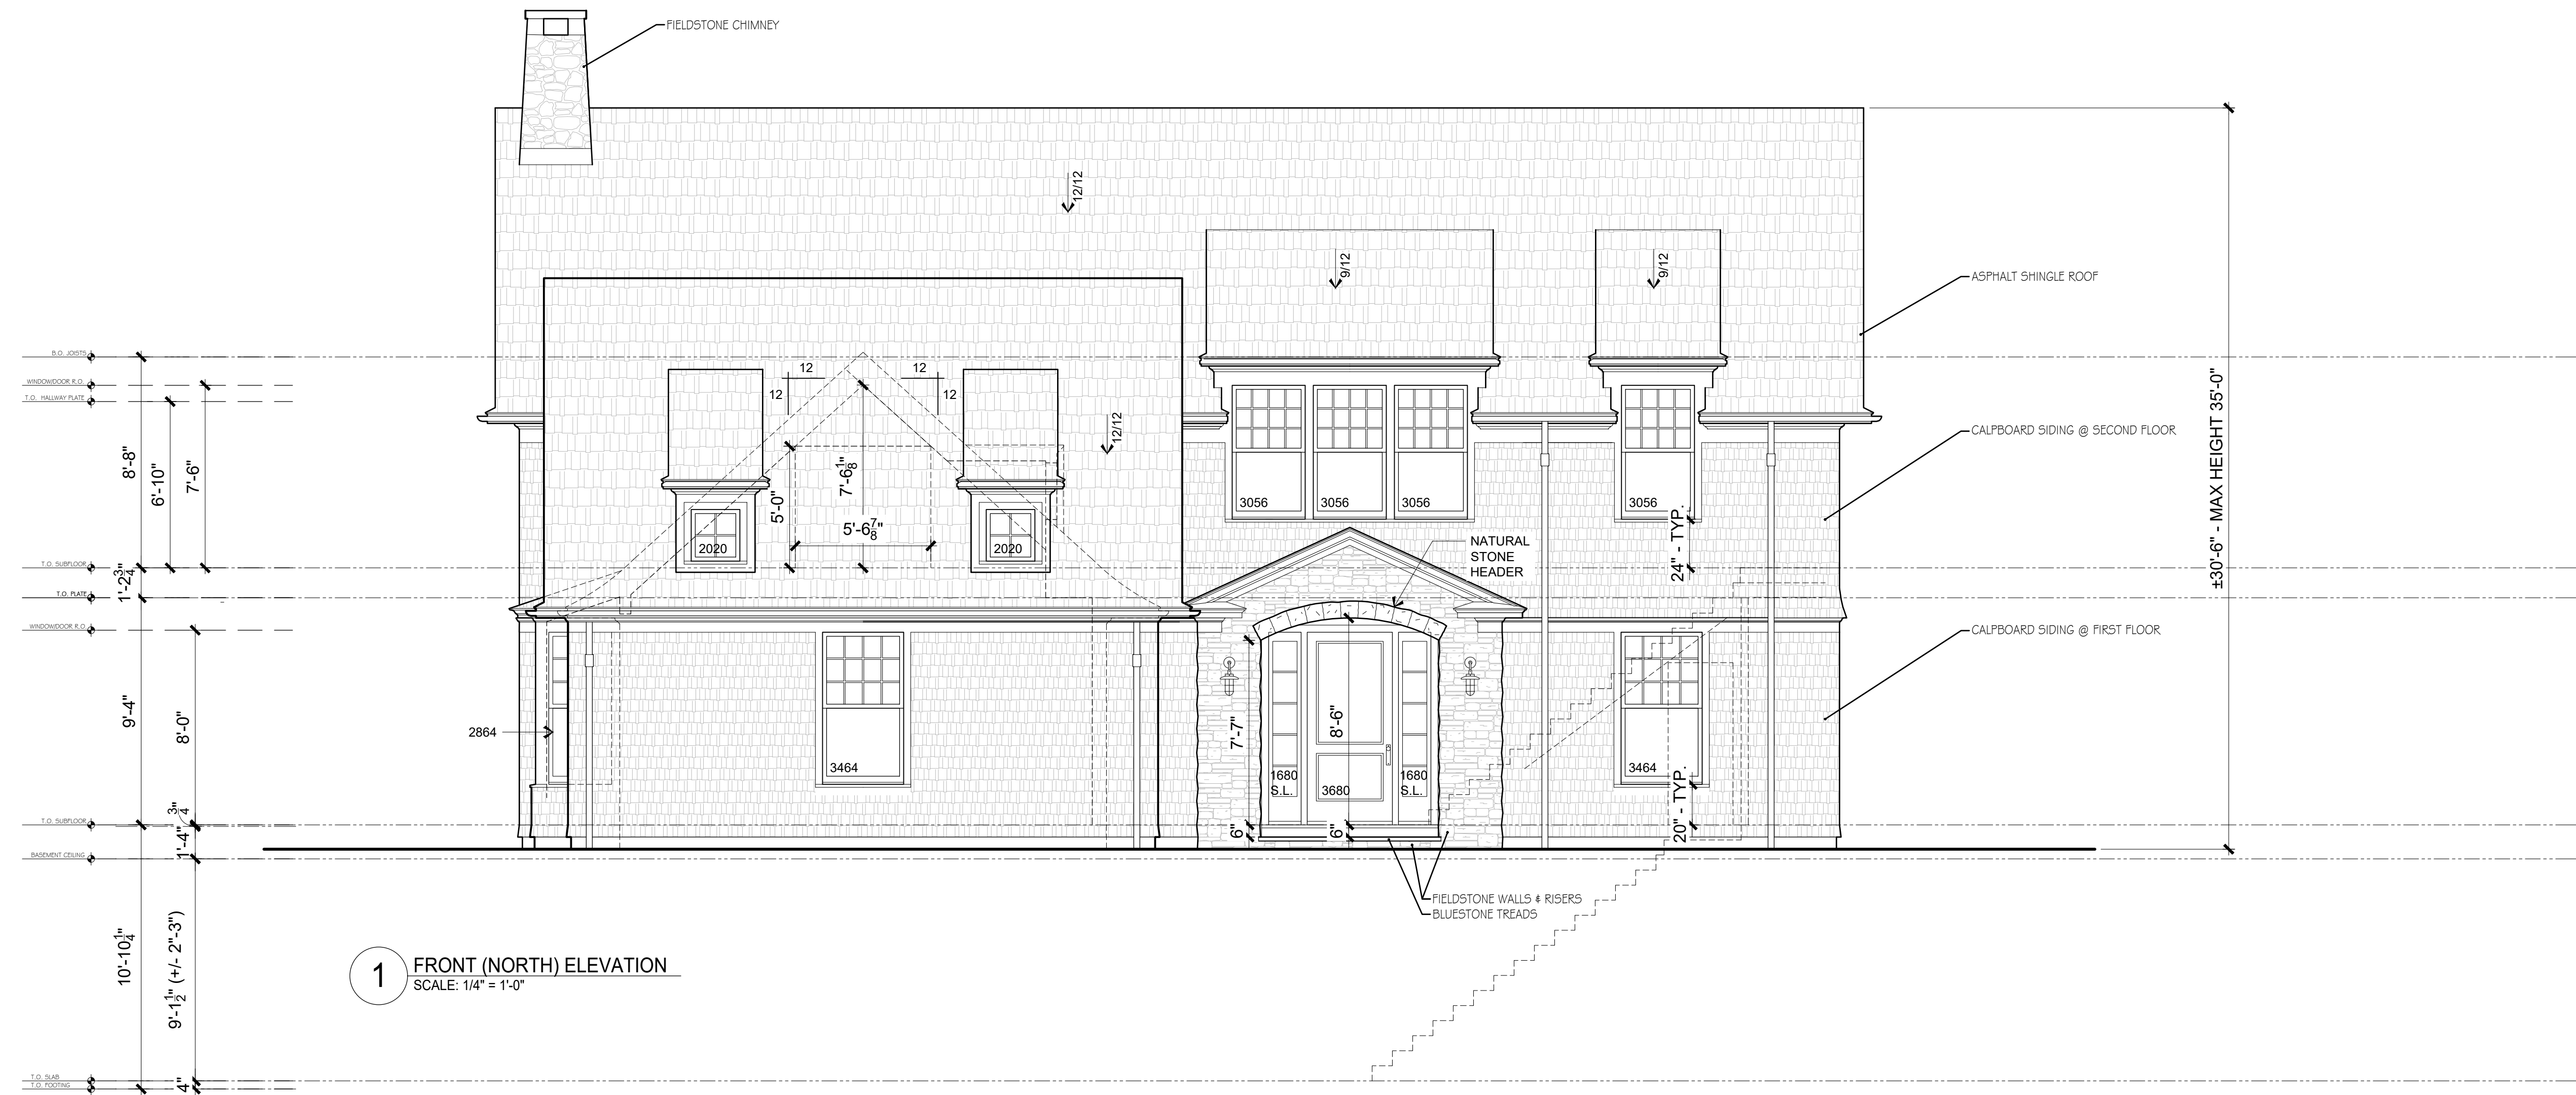

PROPOSED NEW CONSTRUCTION FOR:

**CLIFTON CROSSING**  
7 WARE LANE  
MARBLEHEAD, MA

FL REG. AR95938  
NY REG. 031148

REVISIONS:

1/4" = 1'-0"

DATE:  
5/24/2025  
SCALE:

**A-401**

EXTERIOR ELEVATIONS

917 647-2039



# CLIFTON CROSSING

7 WARE LANE  
MARBLEHEAD, MA

## REVISIONS

$$1/4'' = 1'-0''$$

DATE:  
3/24/2023

SCALE:

A-402

## EXTERIOR ELEVATIONS



1 RIGHT (EAST) ELEVATION  
SCALE: 1/4" = 1'-0"





1 REAR (SOUTH) ELEVATION  
SCALE: 1/4" = 1'-0"

PROPOSED NEW CONSTRUCTION FOR:

CLIFTON CROSSING  
7 WARE LANE  
MARBLEHEAD, MA

FL REG. AR95938  
NY REG. 031148

REVISIONS:

1/4" = 1'-0"

DATE:  
3/24/2025  
SCALE:

A-403

EXTERIOR ELEVATIONS





1 LEFT (WEST) ELEVATION  
SCALE: 1/4" = 1'-0"

PROPOSED NEW CONSTRUCTION FOR:

**CLIFTON CROSSING**  
7 WARE LANE  
MARBLEHEAD, MA

FL REG. AR95938  
NY REG. 031148

REVISIONS:

1/4" = 1'-0"

DATE:  
5/24/2025  
SCALE:

**A-404**

EXTERIOR ELEVATIONS