

7 Ware Lane, Marblehead MA




Design Meeting #2 - Ronna & Mitch Sauerhoff
March 18, 2023



Floor Plans

[illegible]

kitchen & pantry detail

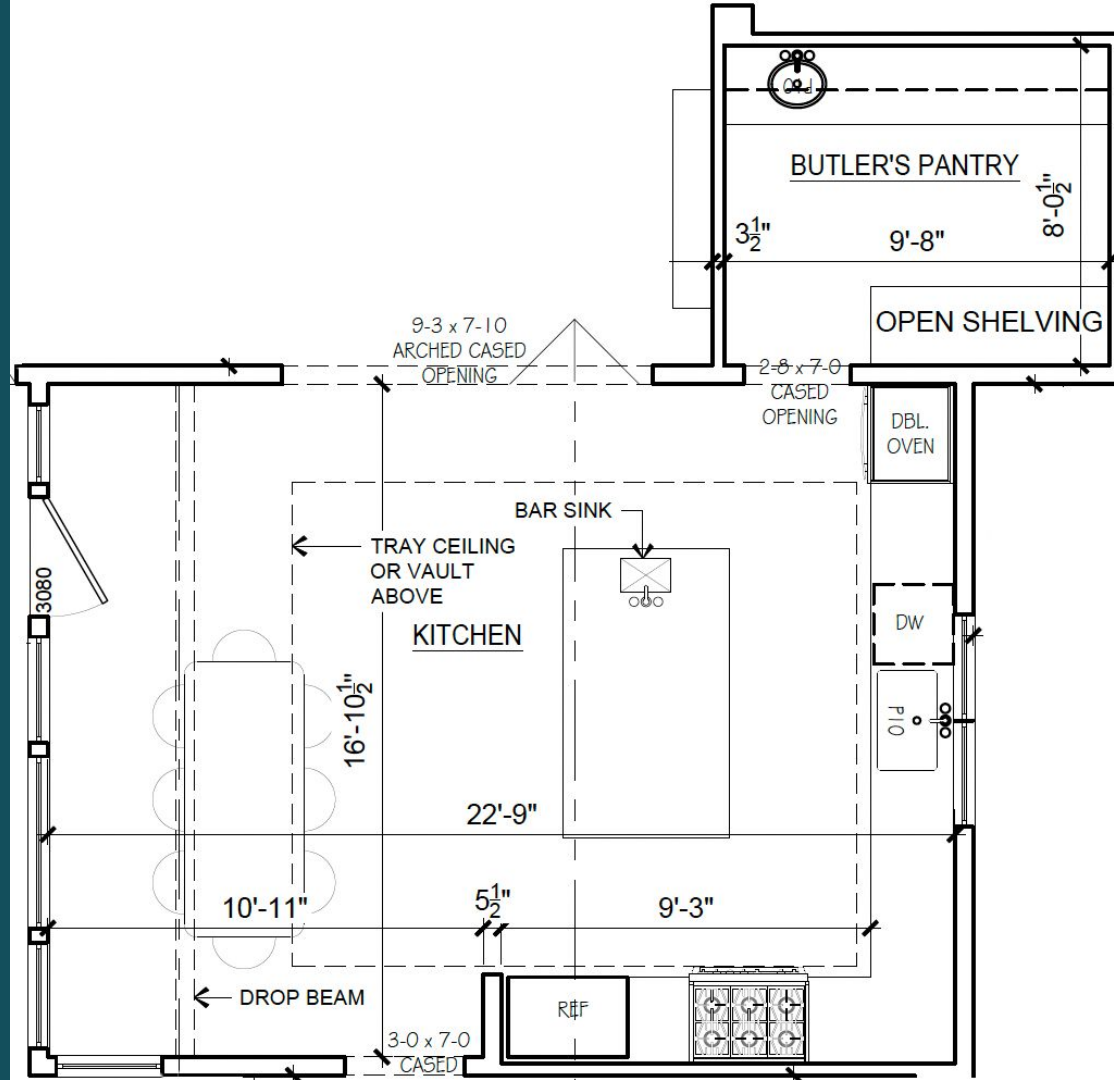

Architectural floor plan of the second floor, showing rooms, dimensions, and structural details.

Rooms and Dimensions:

- Bedroom 1: 14'-0" x 16'-0"
- Bedroom 2: 11'-0" x 11'-4"
- Bedroom 3: 12'-3" x 13'-0"
- Master Bath: 14'-10" x 6'-7"
- Bath 1: 7'-7" x 5'-0"
- Linens: 4'-0" x 2'-0"
- Laundry: 7'-4" x 5'-0"
- Upper Stair Hall: 30'-0" x 5'-0"

Structural Details and Notes:

- RAIN SHOWER HEAD (S2)
- RAIN SHOWER HEAD
- BENCH
- UNDER COUNTER WASHER AND DRYER WITH SINKS ABOVE
- 6'-0" KNEE WALL
- TRAY CEILING OR VAULT BELOW
- KITCHEN WALL ON FIRST FLOOR
- ATTC

Dimensions:

- Overall Width: 28'-0"
- Overall Depth: 24'-0"
- Section Dimensions: 8'-0", 10'-8", 8'-4", 8'-4", 10'-8", 9'-3"
- Room Dimensions: 14'-0", 16'-0", 11'-0", 11'-4", 12'-3", 13'-0", 7'-8", 3'-4", 9'-5", 13'-0", 12'-0", 30'-0", 5'-0", 7'-4", 6'-8", 3'-4", 3'-4", 9'-4", 7'-4"

square footage


AREA CALCULATIONS	
ORIGINAL DESIGN	
FIRST FLOOR	1,675 S.F.
SECOND FLOOR	2,150 S.F.
TOTAL	3,825 S.F.
NEW DESIGN	
FIRST FLOOR (540 S.F. ADDED)	2,215 S.F.
490 S.F. ADD FOR MASTER BEDROOM/SUNROOM	
30 S.F. ADD FOR KITCHEN	
20 S.F. ADD FOR MUDROOM	
SECOND FLOOR (1,040 S.F. REMOVED)	1,155 S.F.
TOTAL	3,370 S.F.
455 S.F. REMOVED	
+ 205 S.F. COVERED PORCH ADDED	
*GARAGE SIZE UNCHANGED	576 S.F.



Kitchen Design






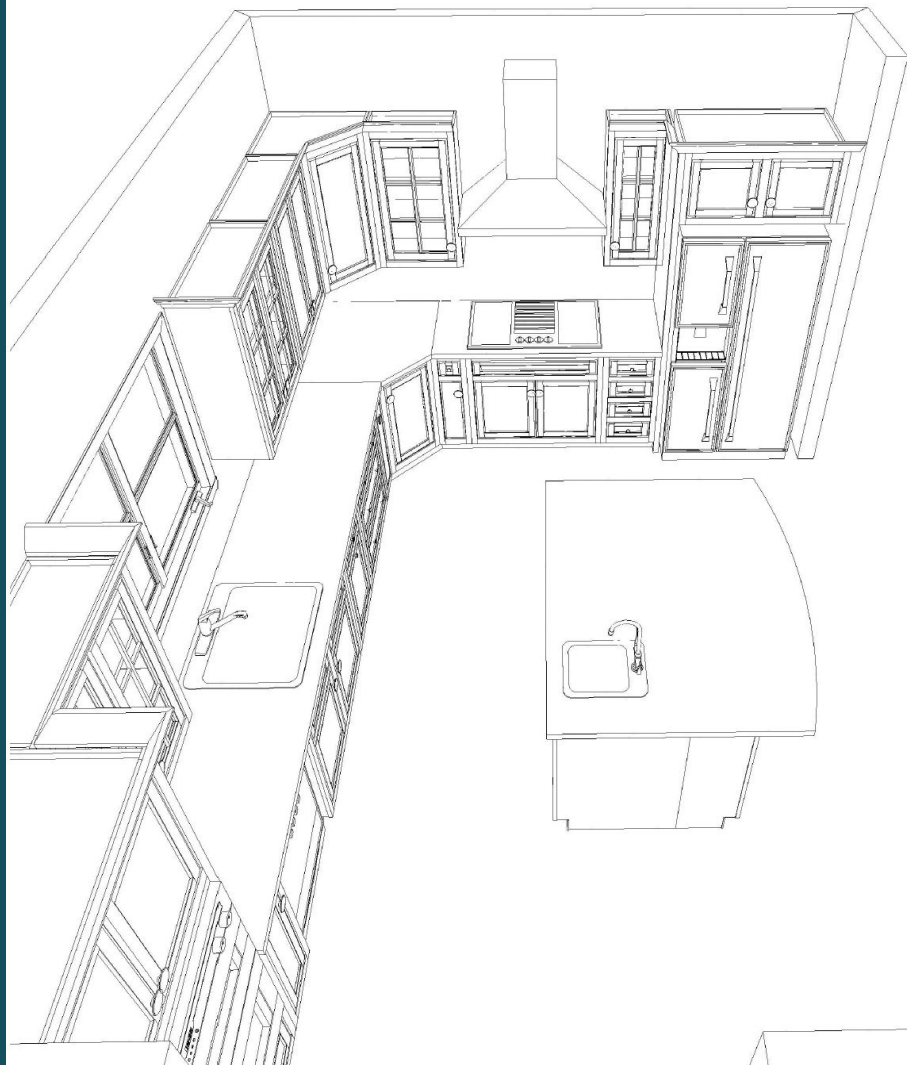






Pantry Layout

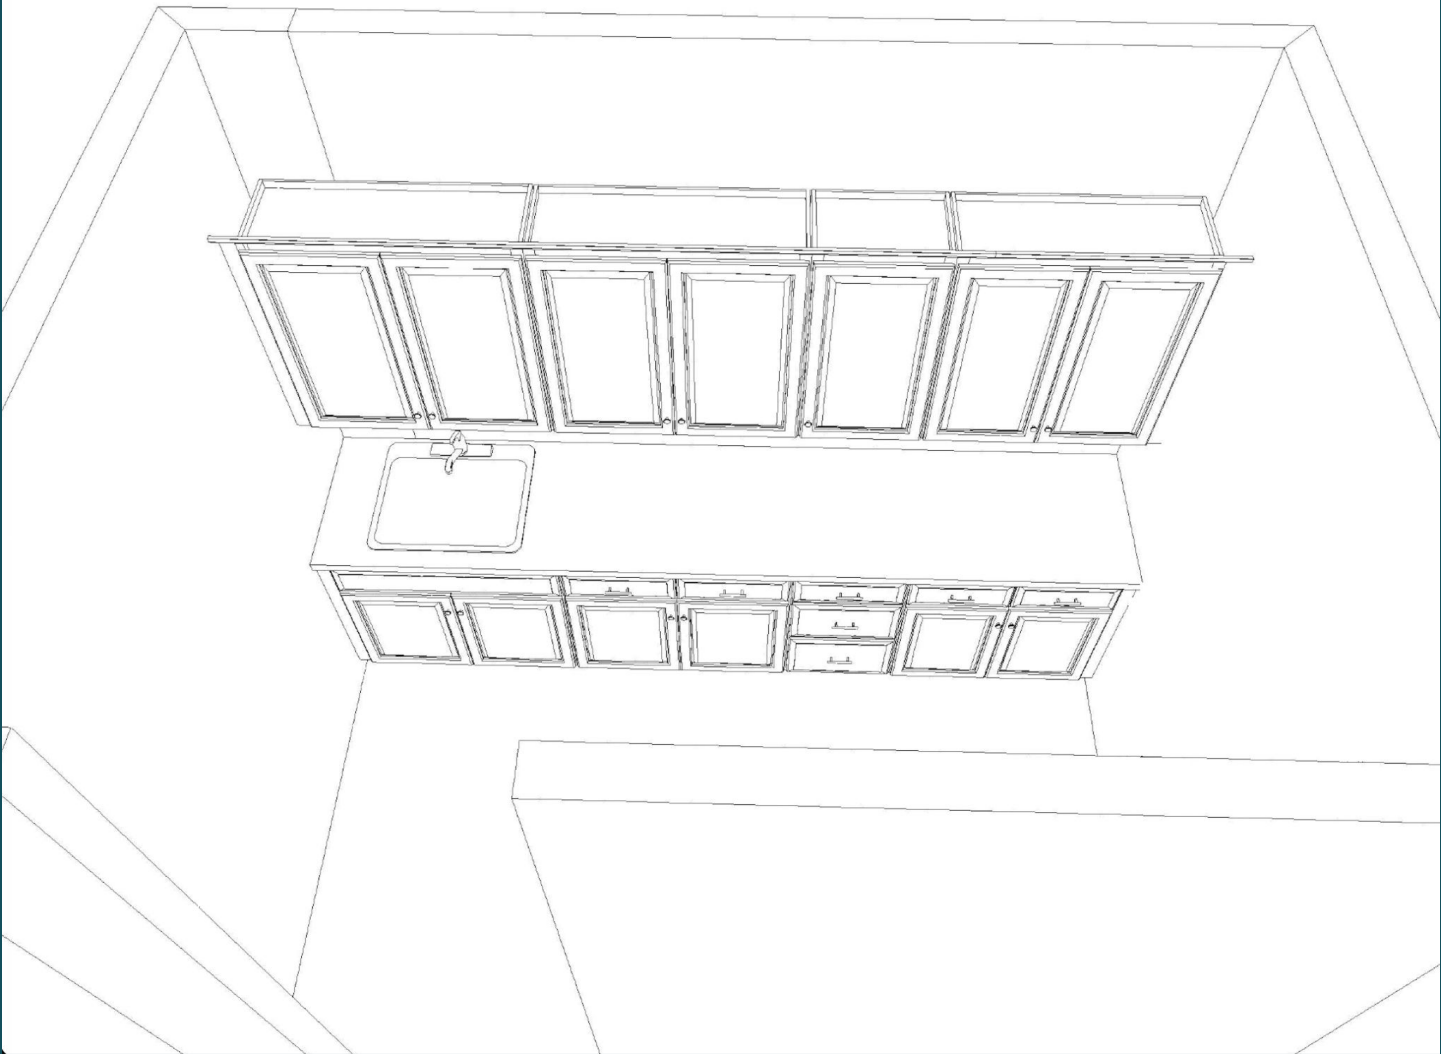



Elevations

north

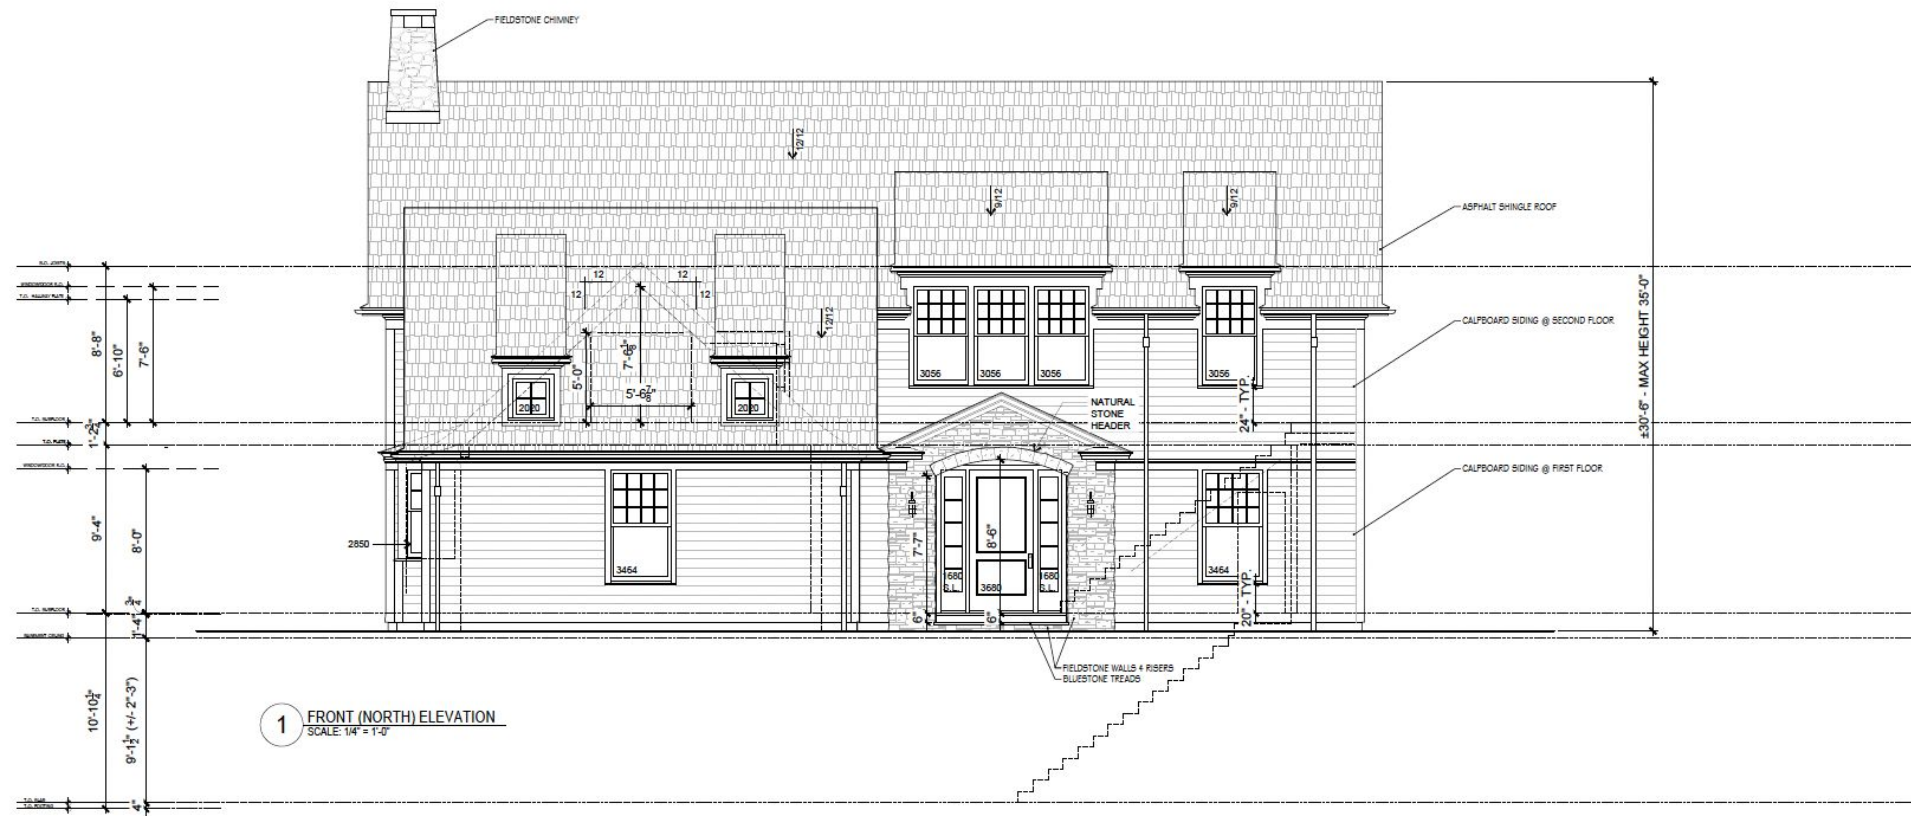



1 FRONT (NORTH) ELEVATION
SCALE: 1/4" = 1'-0"

south



1 LEFT (WEST) ELEVATION
SCALE: 1/4" = 1'-0"

1 LEFT (WEST) ELEVATION
SCALE: 1/4" = 1'-0"



Clifton Crossing



Misc. Inspiration



built-in dresser



wine cellar

