



NEW CONSTRUCTION
for
CLIFTON CROSSING
7 WARE LANE
MARBLEHEAD, MA

ARCHITECT
DAVID NEFF, ARCHITECT

300 GRAHAM AVE #2L
BROOKLYN, NY 11211
917.647.2039

david@davidneffarchitect.com

LIST OF DRAWINGS

A-001 TITLE PAGE
A-201 BASEMENT PLAN
A-211 1st FLOOR PLAN
A-221 2nd FLOOR PLAN
A-231 ROOF PLAN
A-401 EXTERIOR ELEVATIONS
A-402 EXTERIOR ELEVATIONS
A-501 SECTIONS
A-502 SECTIONS
A-503 SECTIONS
A-504 SECTIONS
A-901 DOOR & WINDOW SCHEDULES

S-101 FIRST FLOOR FRAMING
S-102 SECOND FLOOR FRAMING
S-103 ROOF FRAMING

GENERAL NOTES

- THESE DOCUMENTS PREPARED BY DAVID NEFF, ARCHITECT ARE INSTRUMENTS OF SERVICE FOR USE SOLELY WITH RESPECT TO THIS PROJECT. THE ARCHITECT AS AUTHOR SHALL RETAIN ALL COMMON LAW, STATUTORY, AND OTHER RESERVED RIGHTS, INCLUDING THE COPYRIGHT.
- IT IS THE INTENT OF THE ARCHITECT THAT THIS PROJECT BE IN CONFORMANCE WITH THE MASSACHUSETTS STATE BUILDING CODE AND ALL OTHER APPLICABLE CODES IN THIS JURISDICTION. THESE CODES SHALL TAKE PRECEDENCE OVER THE DRAWINGS AND SPECIFICATIONS.
- ALL WORK SHALL BE PERFORMED BY A LICENSED GENERAL CONTRACTOR WHO SHALL COORDINATE AND SUPERVISE HIS OWN WORK AND THE WORK OF HIS SUBCONTRACTORS.
- THE CONTRACTOR SHALL VERIFY ALL CONDITIONS AND DIMENSIONS AND SHALL REPORT ANY INCONSISTENCIES WITH THE CONSTRUCTION DOCUMENTS TO THE ARCHITECT BEFORE CONTINUING WORK.
- THE OWNER SHALL NOT BE HELD RESPONSIBLE FOR VERIFIABLE EXISTING CONDITIONS AFTER THE CONTRACT IS AWARDED
- DO NOT SCALE DRAWINGS UNLESS AUTHORIZED BY THE ARCHITECT
- THE GENERAL CONDITIONS OF AMERICAN INSTITUTE OF ARCHITECTS' DOCUMENT A107-2007 ARE HEREBY MADE PART OF THE CONTRACT DOCUMENTS TO THE SAME EXTENT AS IF WRITTEN OUT IN FULL.
- RELEVANT SECTIONS OF THE WRITTEN SPECIFICATIONS SHALL BE DISTRIBUTED TO EACH SUBCONTRACTOR.

LEGEND

	EXISTING CONSTRUCTION
	DEMOLISH EXISTING
	NEW 2x WALL
	NEW CONCRETE WALL
	BRICK VENEER
	STONE WALL
	PLUMBING HOOKUP
	SMOKE DETECTOR
	CARBON MONOXIDE DETECTOR
	HOSE BIBB
	CENTER LINE
	NEW DOOR SYMBOL
	NEW WINDOW SYMBOL
	INTERIOR ELEVATION REFERENCES
	DETAIL REFERENCES

ABBREVIATIONS

AFF	ABOVE FINISH FLOOR	SQ	SQUARE
BOT	BOTTOM	TOS	TOP OF SLAB
CLG	CEILING	TOB	TOP OF BEAM
CLR	CLEAR	T&G	TONQUE AND GROOVE
CO	CASED OPENING	TYP	TYPICAL
COL	COLUMN	WWF	WELDED WIRE FABRIC
CONC	CONCRETE		
CMU	CONCRETE MASONRY UNIT		
CONT	CONTINUOUS		
DIAM	DIAMETER		
DIM	DIMENSION		
DS	DOWNSPOUT		
DWG	DRAWING		
ELEV	ELEVATION		
EQ	EQUAL		
EXT	EXTERIOR		
FLR	FLOOR		
FTG	FOOTING		
GA	GAUGE		
GWB	GYPSUM WALL BOARD		
HT	HEIGHT		
HB	HOSE BIBB		
HW	HOT WATER		
INT	INTERIOR		
MO	MASONRY OPENING		
MAX	MAXIMUM		
MIN	MINIMUM		
NIC	NOT IN CONTRACT		
NTS	NOT TO SCALE		
OC	ON CENTER		
PT	PRESSURE-TREATED		
RM	ROOM		
RO	ROUGH OPENING (HEAD HT ABOVE SUBFLOOR)		
SIM	SIMILAR		
SPEC	SPECIFICATIONS SECTION		

PROPOSED NEW CONSTRUCTION FOR:

CLIFTON CROSSING
7 WARE LANE
MARBLEHEAD, MA

DAVID NEFF, ARCHITECT

300 GRAHAM AVE. #2L
BROOKLYN, NY 11211

davidneffarchitect.com

917 647-2039


FL REG. AR95938
NY REG. 031148



REVISIONS:

DATE:
6/19/2019
SCALE:
1/4" = 1'-0"

A-001

TITLE PAGE

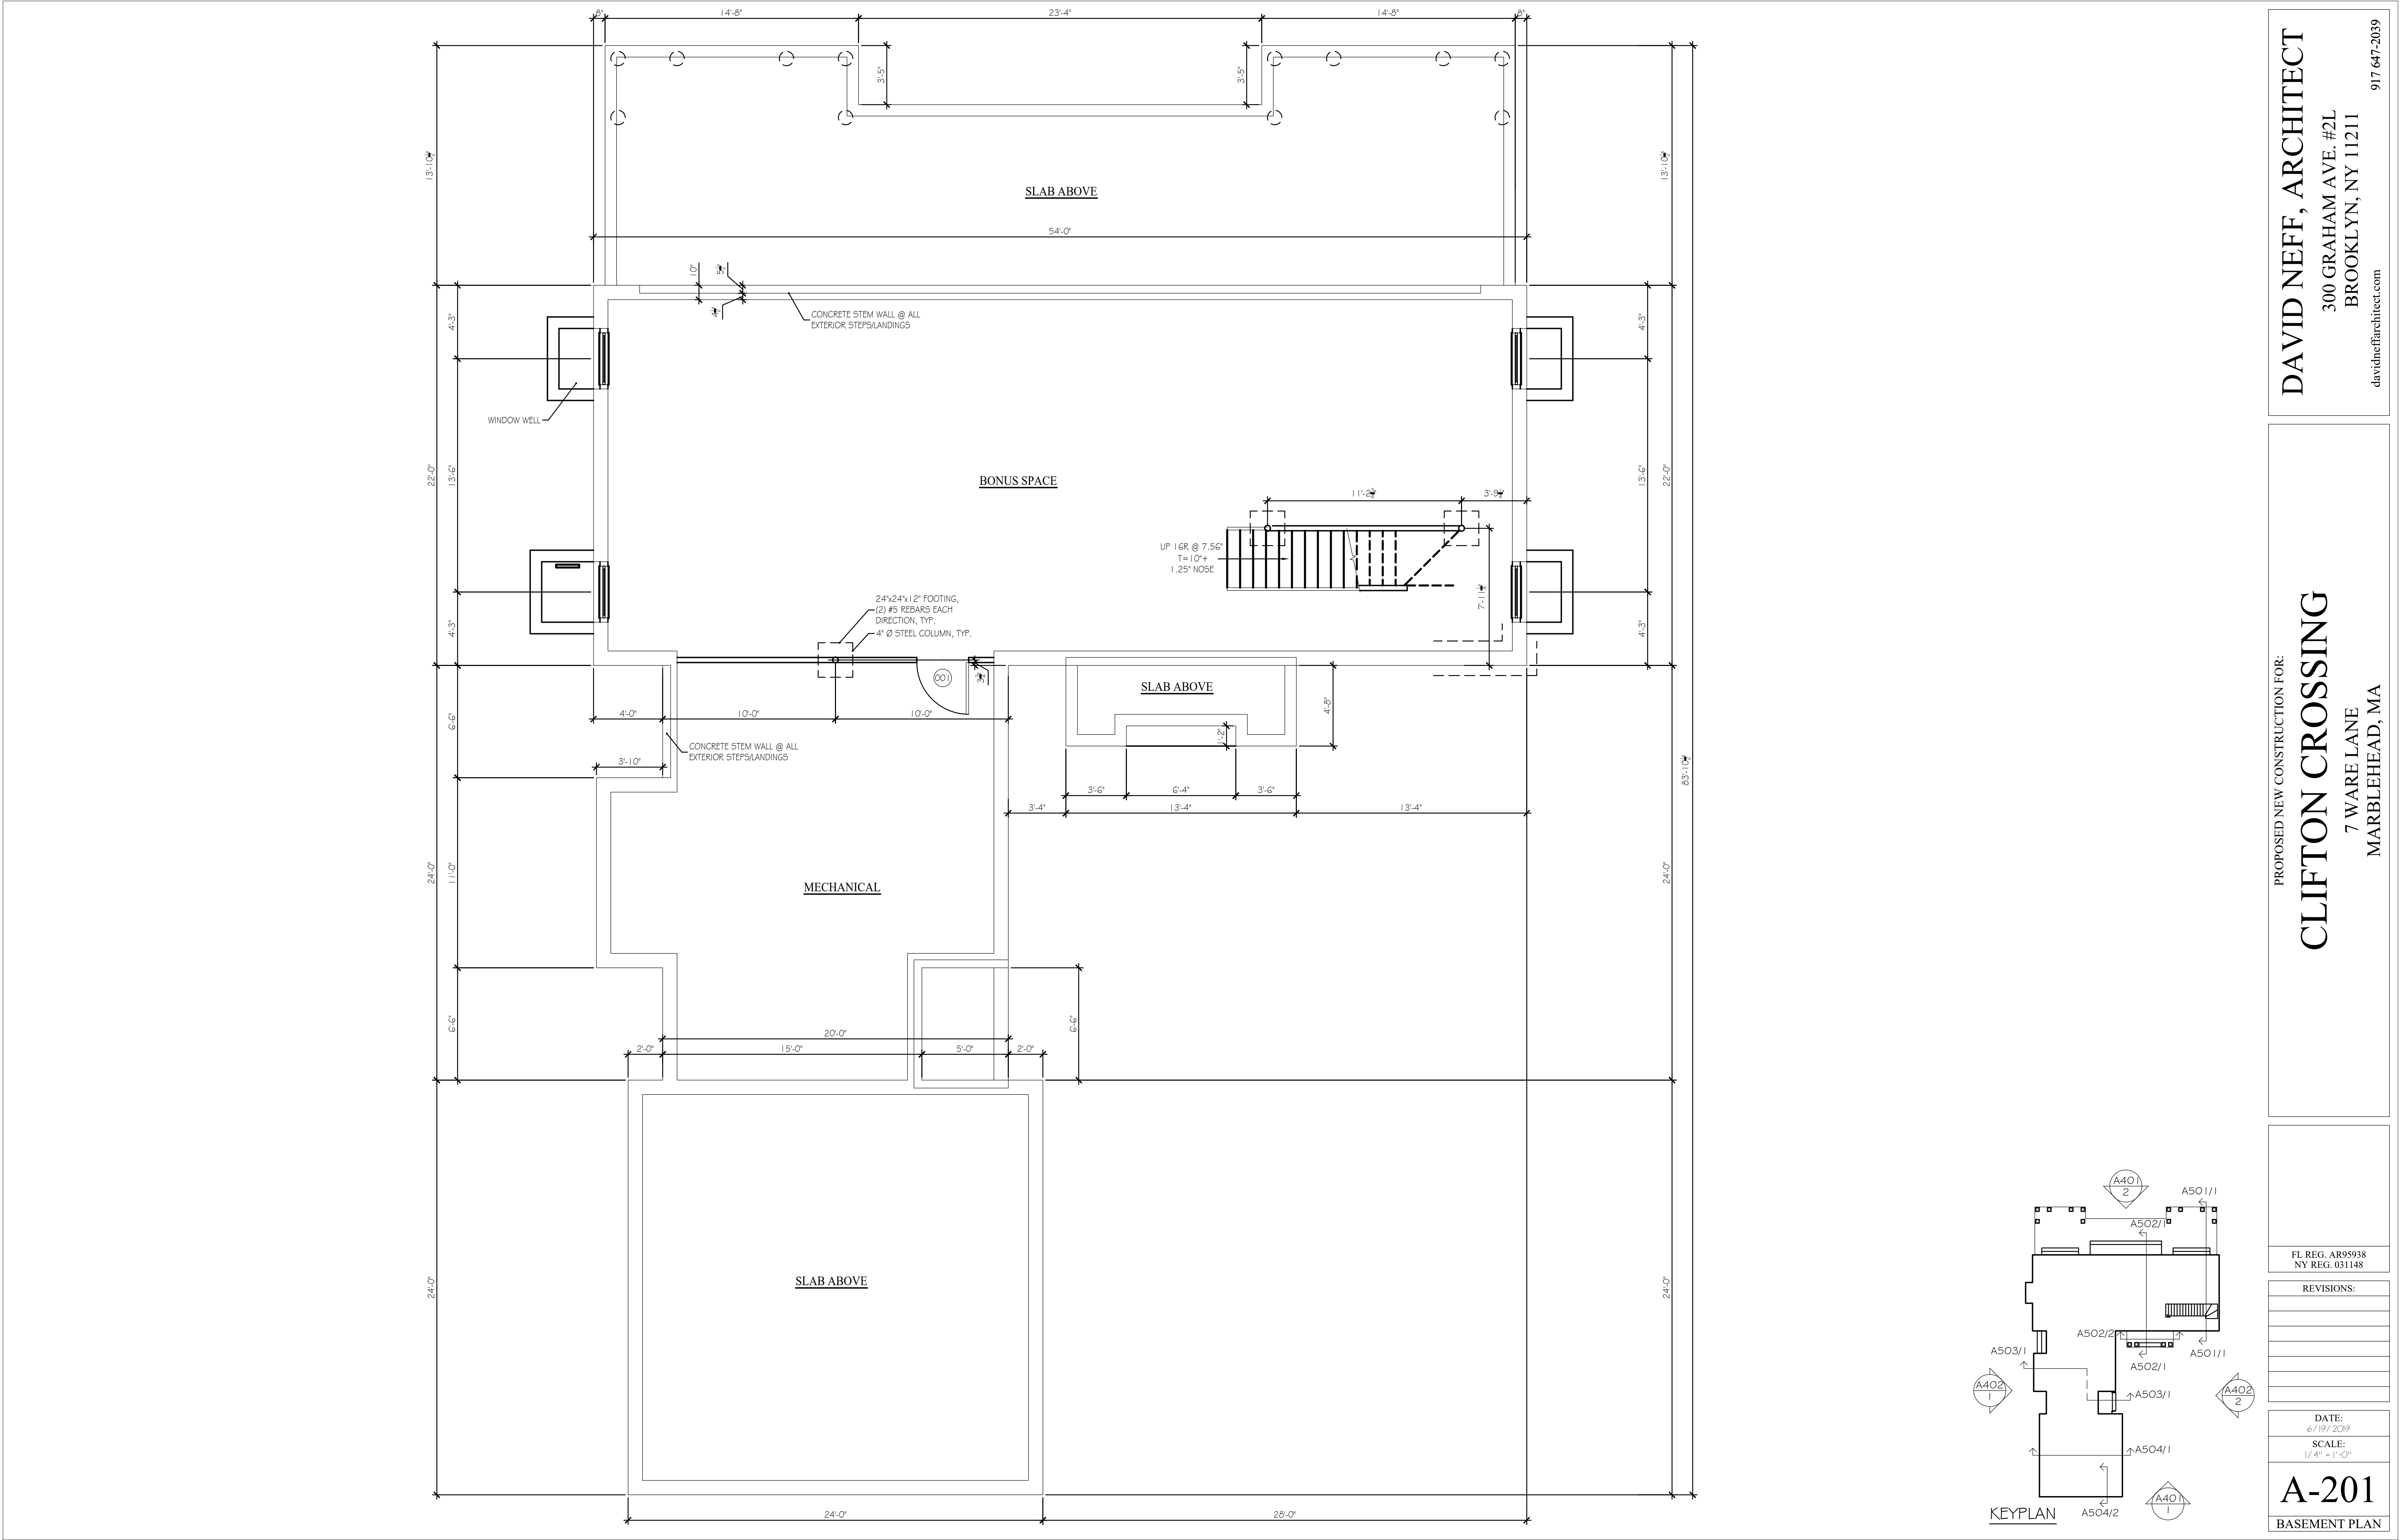

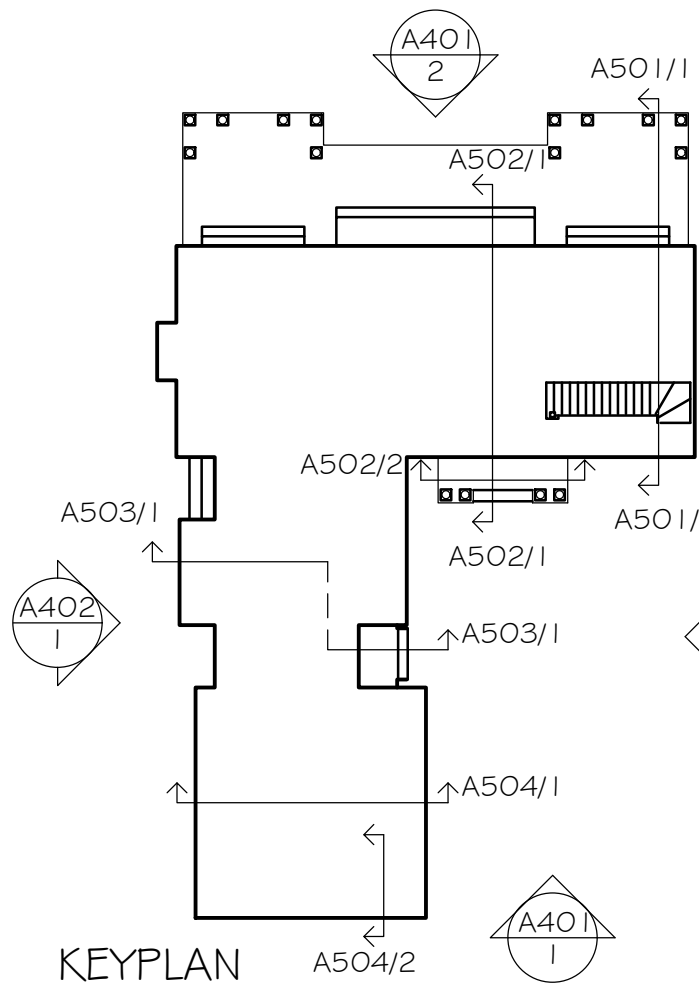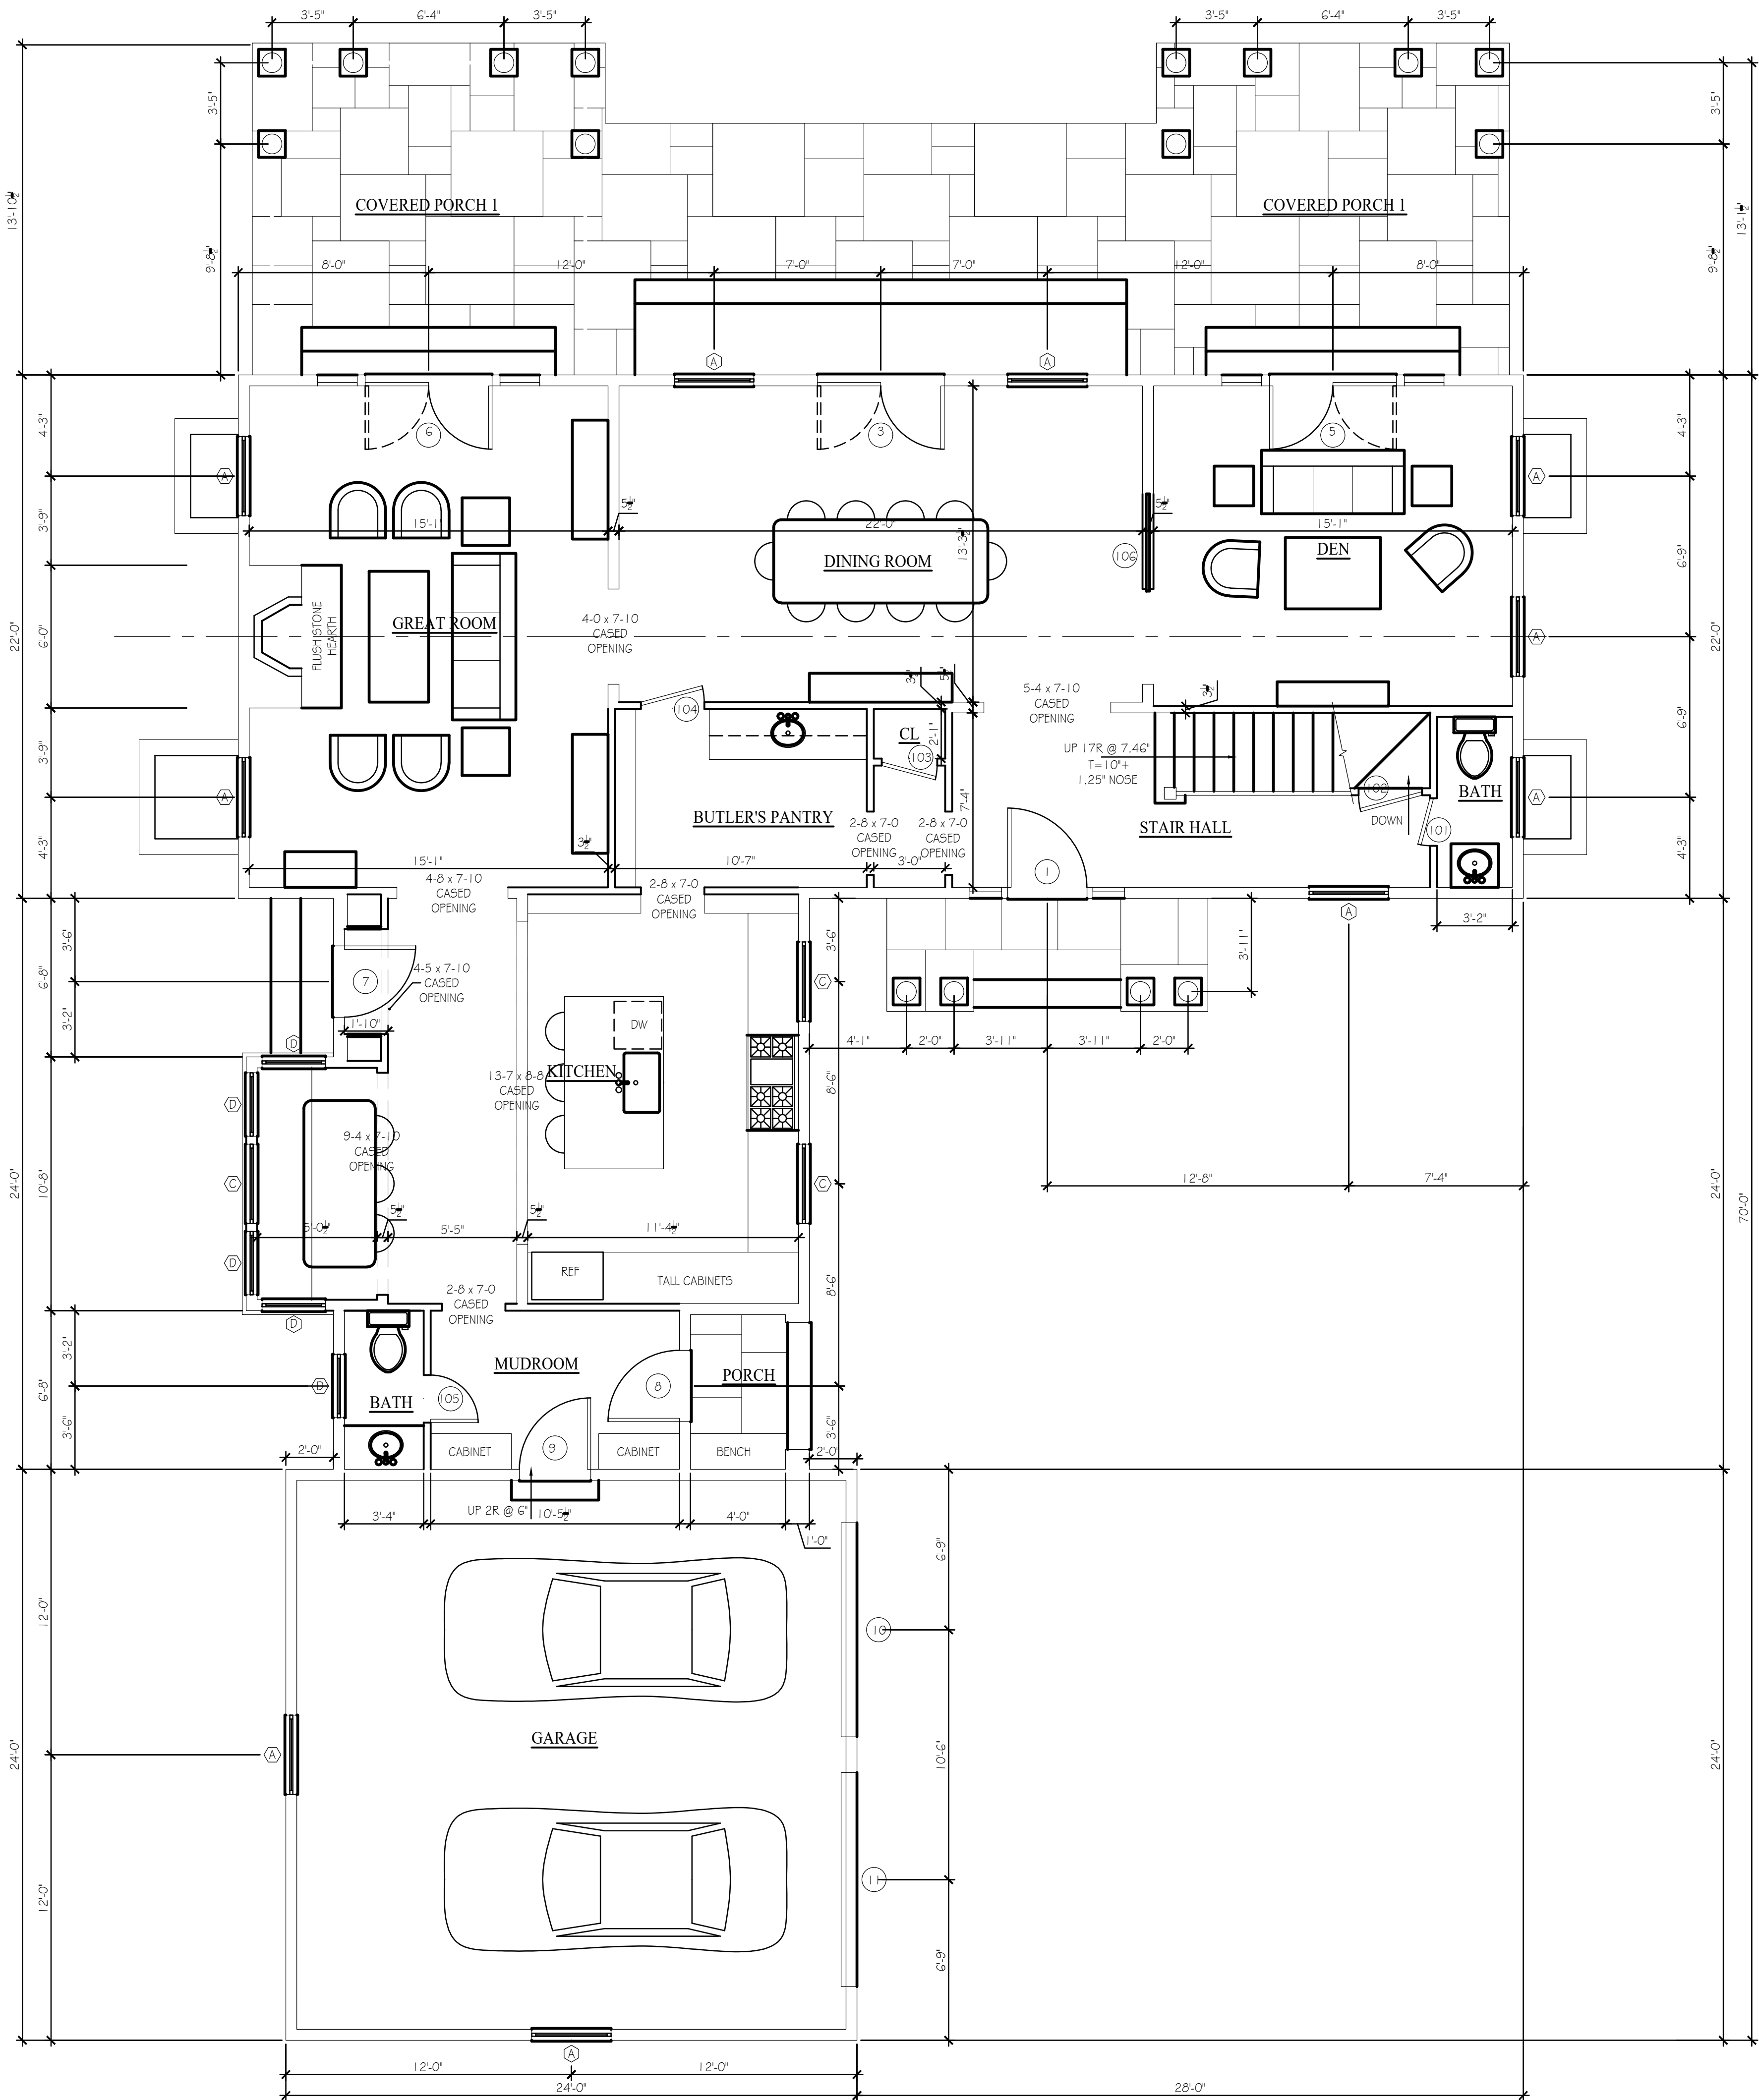

PROPOSED NEW CONSTRUCTION FOR:

CLIFTON CROSSING
7 WARE LANE
MARBLEHEAD, MA

DAVID NEFF, ARCHITECT

300 GRAHAM AVE. #2L
BROOKLYN, NY 11211

davidneffarchitect.com

917 647-2039



FL REG. AR95938
NY REG. 031148

REVISIONS:

DATE:
6/19/2019
SCALE:
1/4" = 1'-0"

A-211

1st FLOOR PLAN

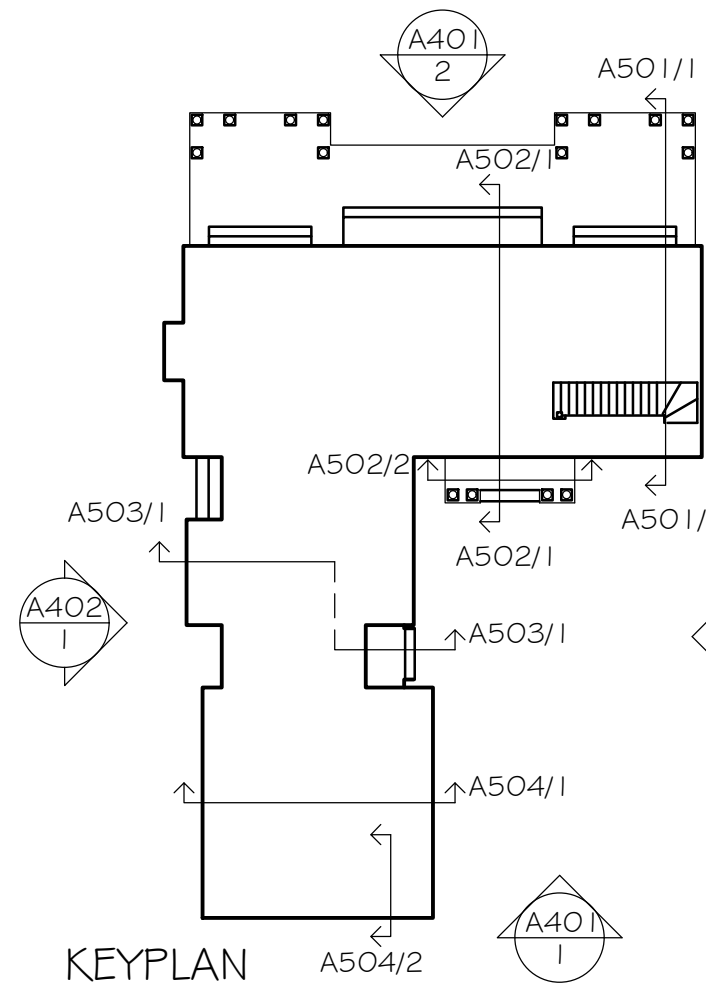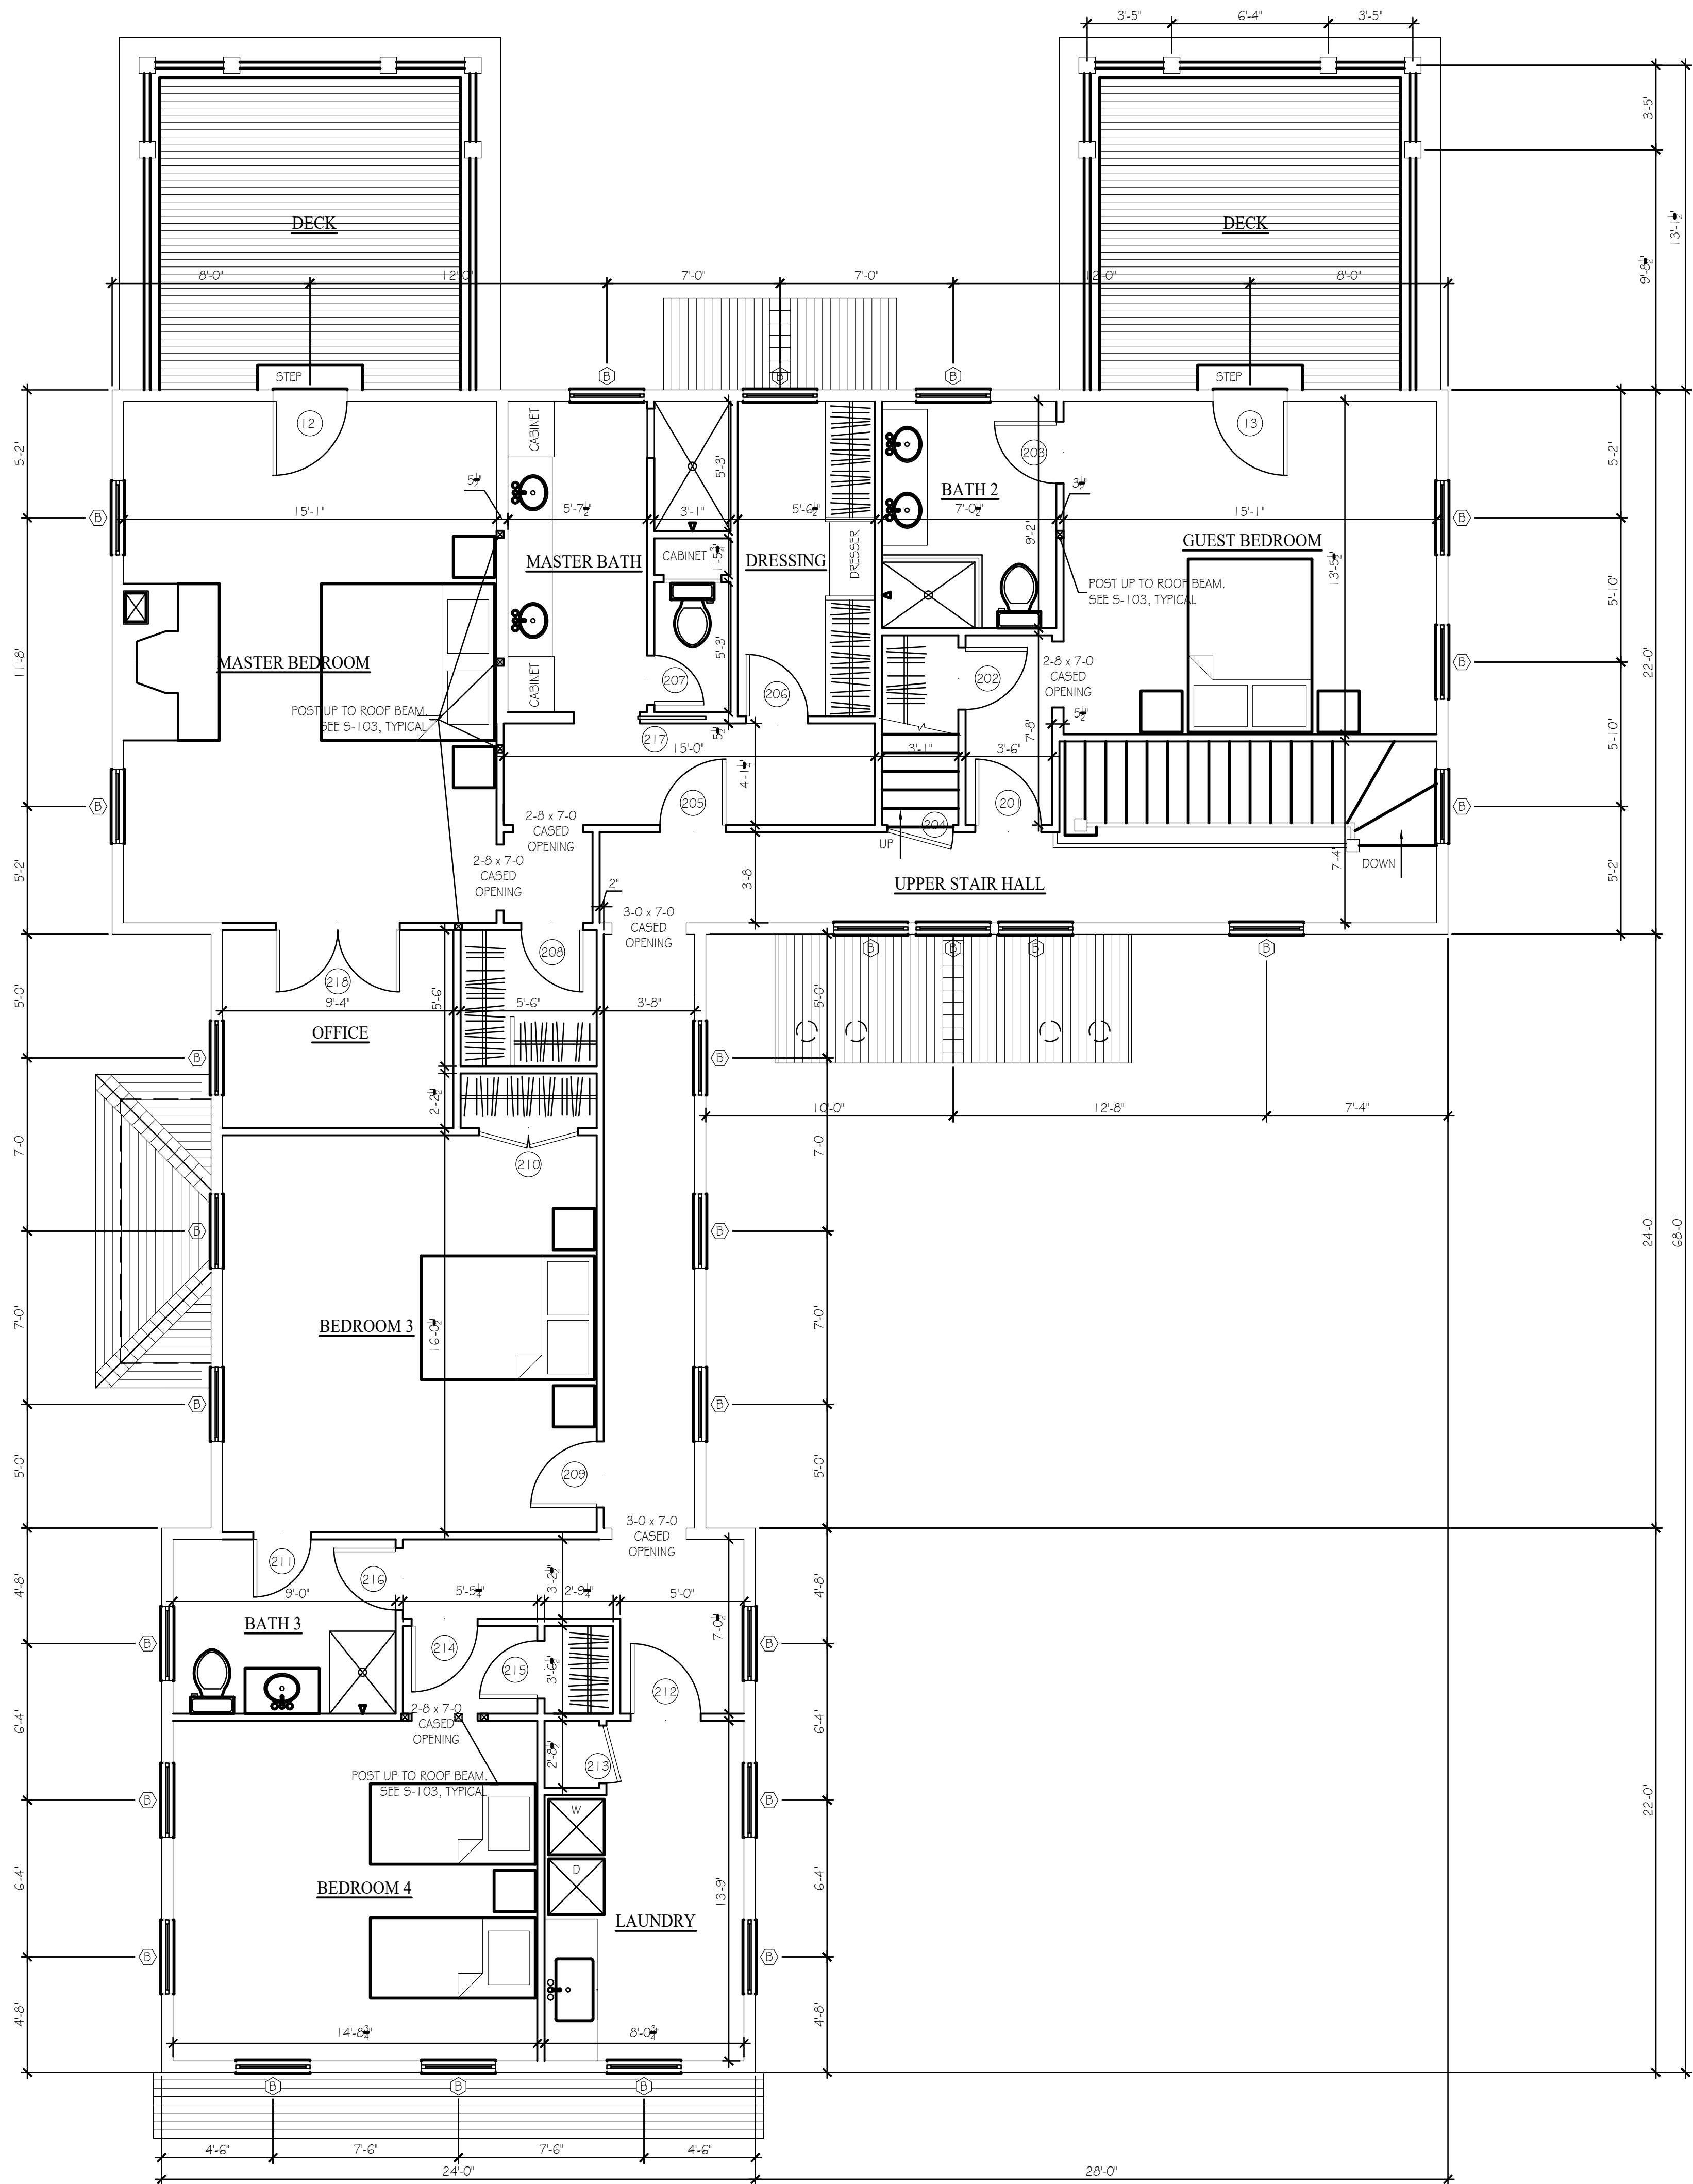

PROPOSED NEW CONSTRUCTION FOR:

CLIFTON CROSSING
7 WARE LANE
MARBLEHEAD, MA

DAVID NEFF, ARCHITECT

300 GRAHAM AVE. #2L
BROOKLYN, NY 11211

davidneffarchitect.com

917 647-2039



FL REG. AR95938
NY REG. 031148

REVISIONS:

DATE:
6/19/2019
SCALE:
1/4" = 1'-0"

A-221

2nd FLOOR PLAN

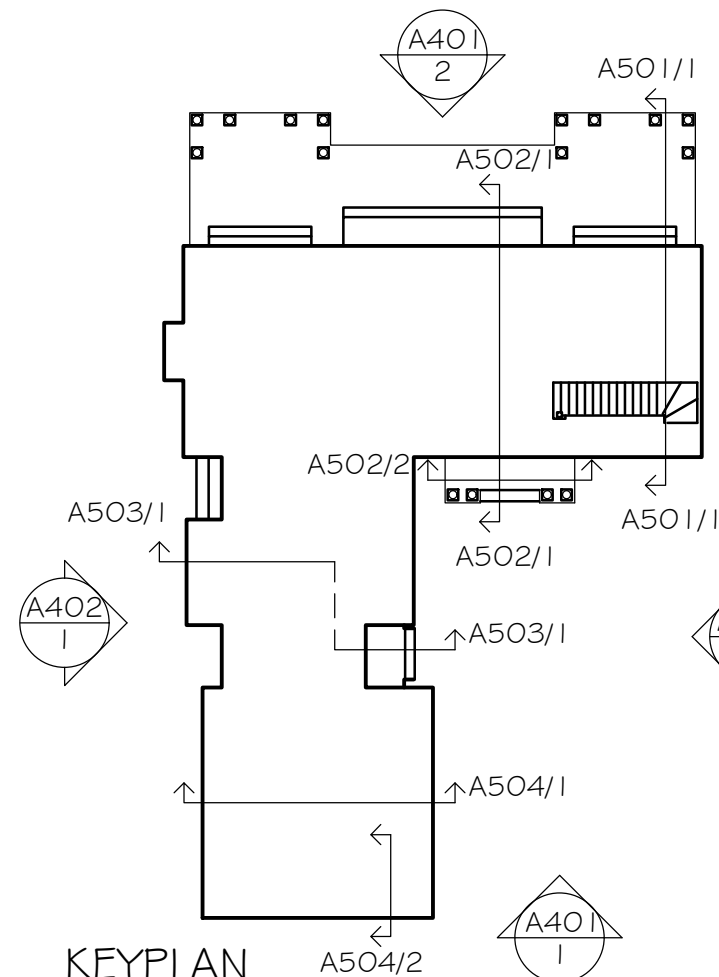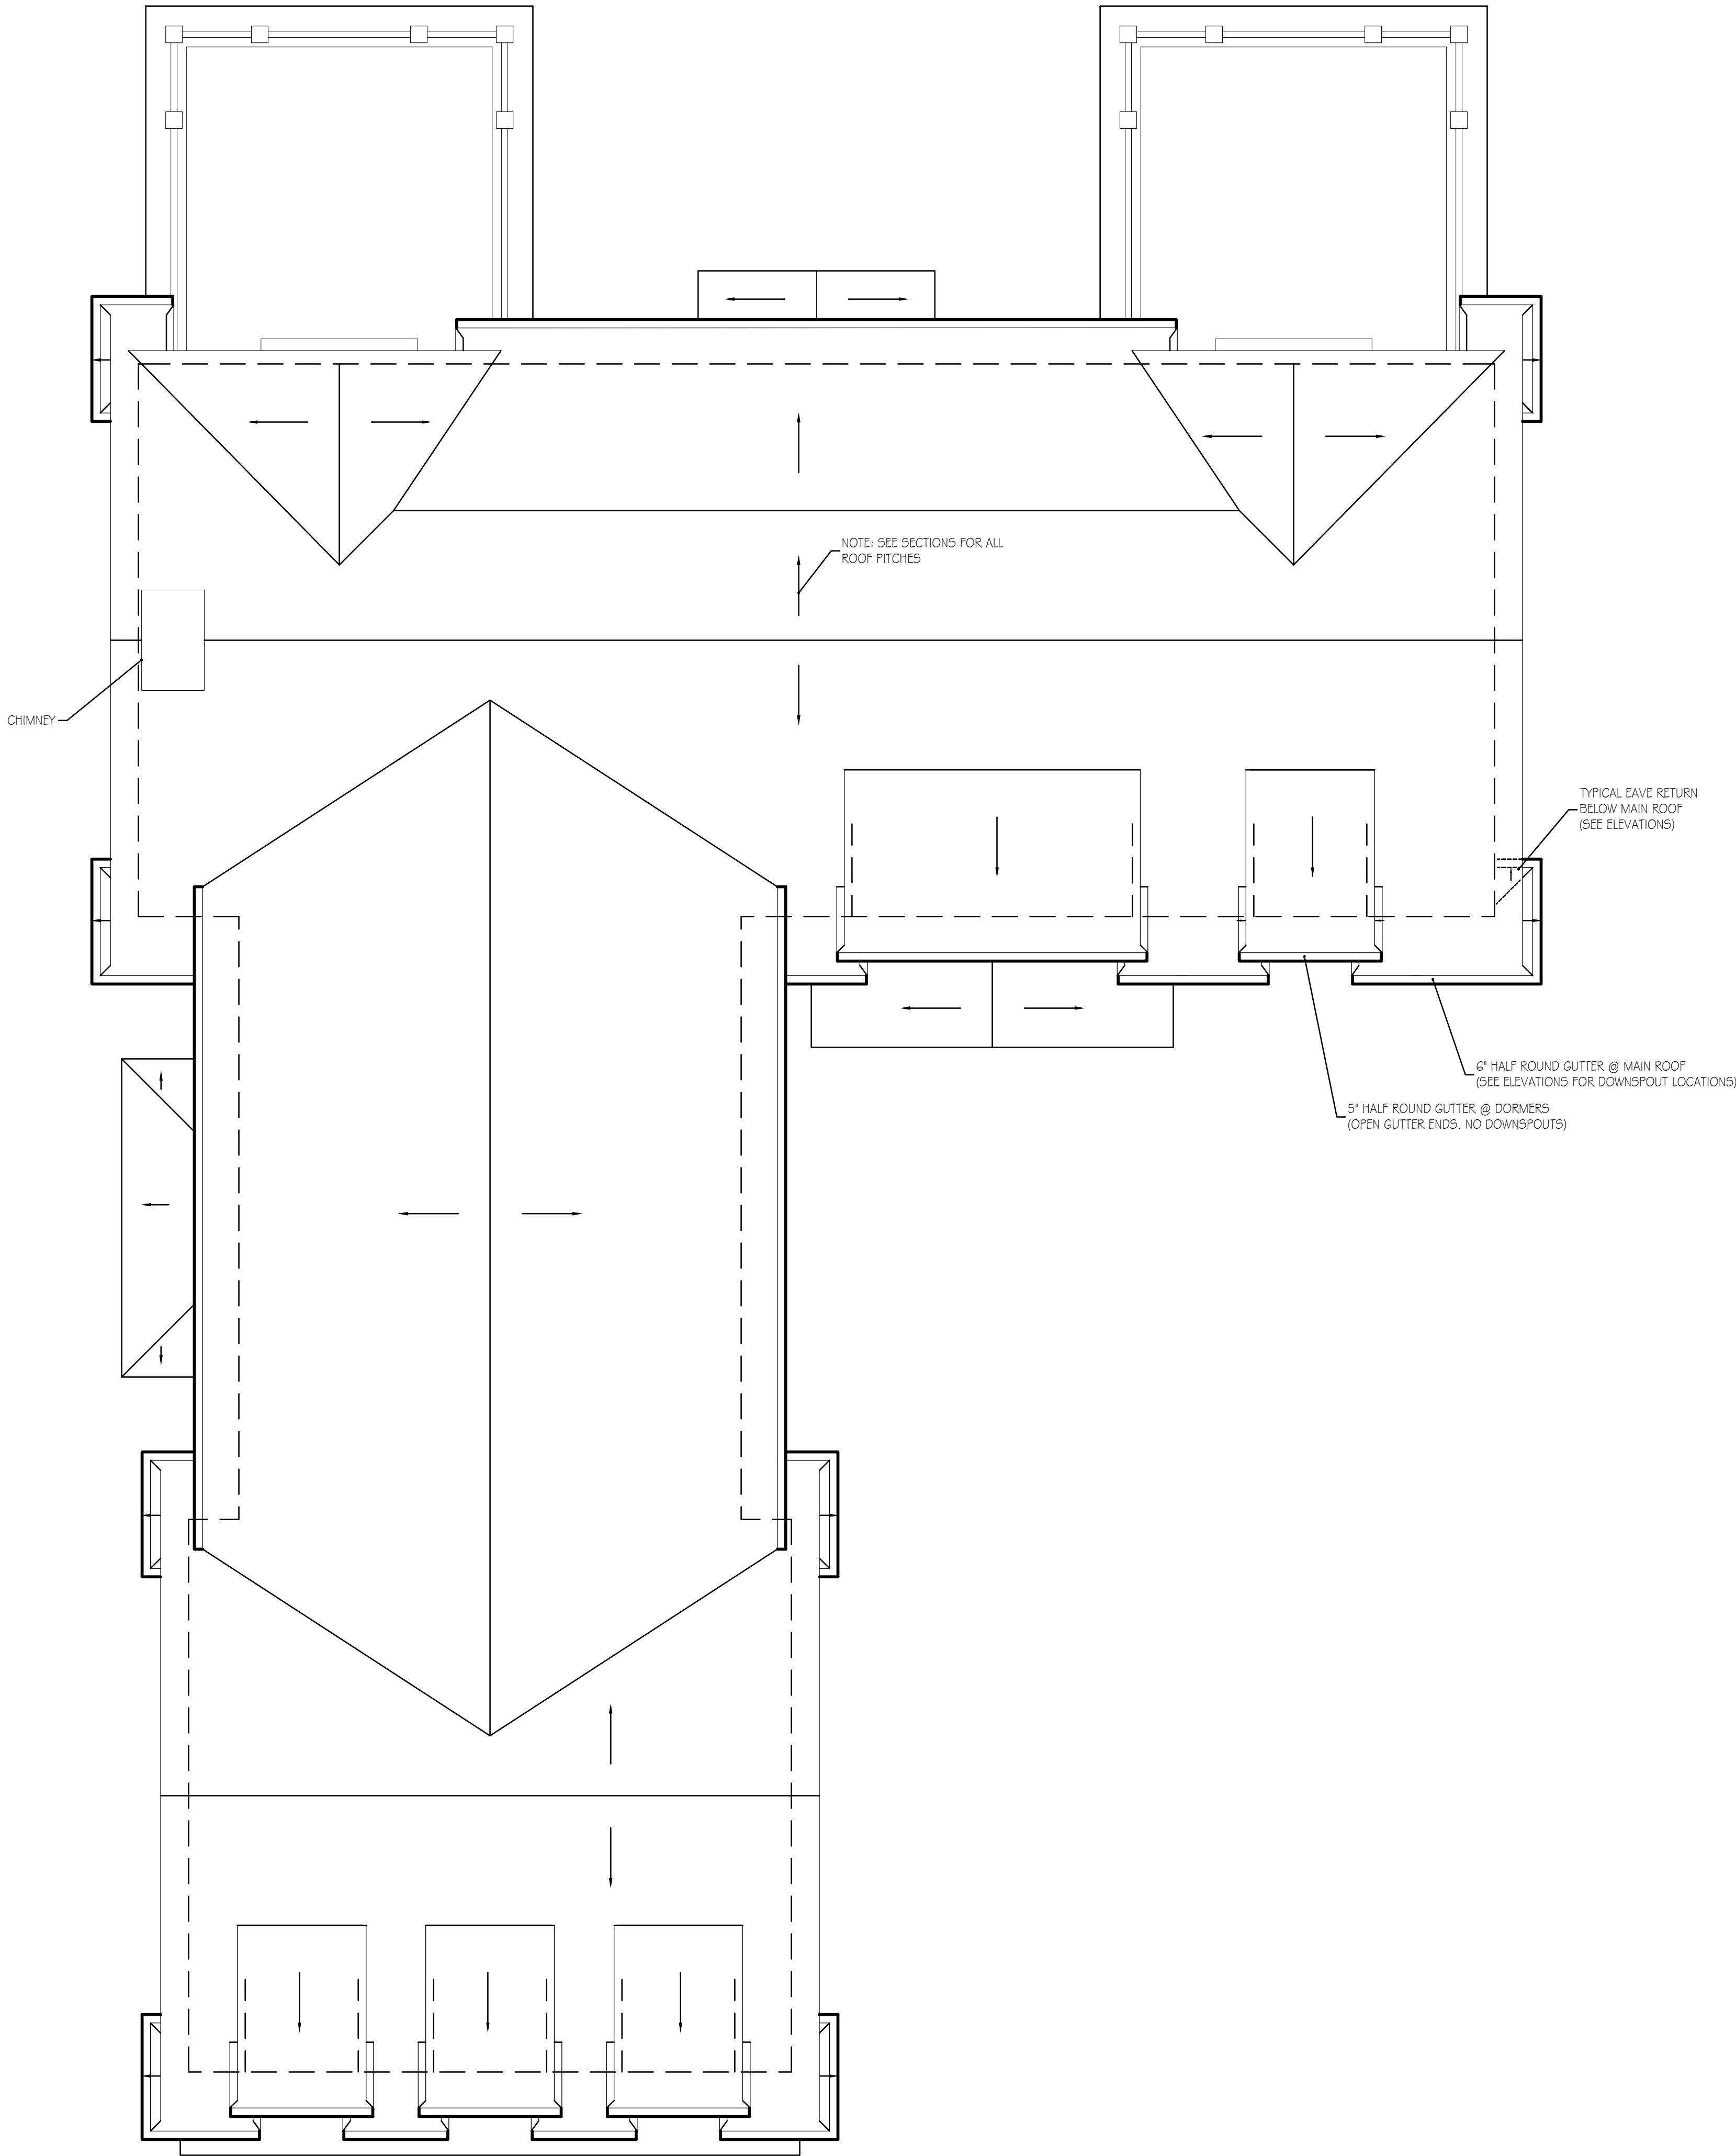

PROPOSED NEW CONSTRUCTION FOR:

CLIFTON CROSSING
7 WARE LANE
MARBLEHEAD, MA

DAVID NEFF, ARCHITECT

300 GRAHAM AVE. #2L
BROOKLYN, NY 11211

davidneffarchitect.com

917 647-2039

FL REG. AR95938
NY REG. 031148

REVISIONS:

DATE:
6/19/2019
SCALE:
1/4" = 1'-0"

A-231

3rd FL./ROOF PLAN



1 NORTH ELEVATION
SCALE: 1/4" = 1'-0"



2 SOUTH ELEVATION
SCALE: 1/4" = 1'-0"

DAVID NEFF, ARCHITECT
300 GRAHAM AVE. #2L
BROOKLYN, NY 11211
davidneffarchitect.com 917 647-2039

PROPOSED NEW CONSTRUCTION FOR:
CLIFTON CROSSING
7 WARE LANE
MARBLEHEAD, MA

FL REG. AR95938
NY REG. 031148

REVISIONS:

DATE:
6/19/2019
SCALE:
1/4" = 1'-0"

A-401

EXTERIOR ELEVATIONS



1 EAST ELEVATION
SCALE: 1/4" = 1'-0"



2 WEST ELEVATION
SCALE: 1/4" = 1'-0"

DAVID NEFF, ARCHITECT
300 GRAHAM AVE. #2L
BROOKLYN, NY 11211
davidneffarchitect.com 917 647-2039

PROPOSED NEW CONSTRUCTION FOR:
CLIFTON CROSSING
7 WARE LANE
MARBLEHEAD, MA


FL REG. AR95938
NY REG. 031148

REVISIONS:


DATE:
6/19/2019
SCALE:
1/4" = 1'-0"

A-402

EXTERIOR ELEVATIONS

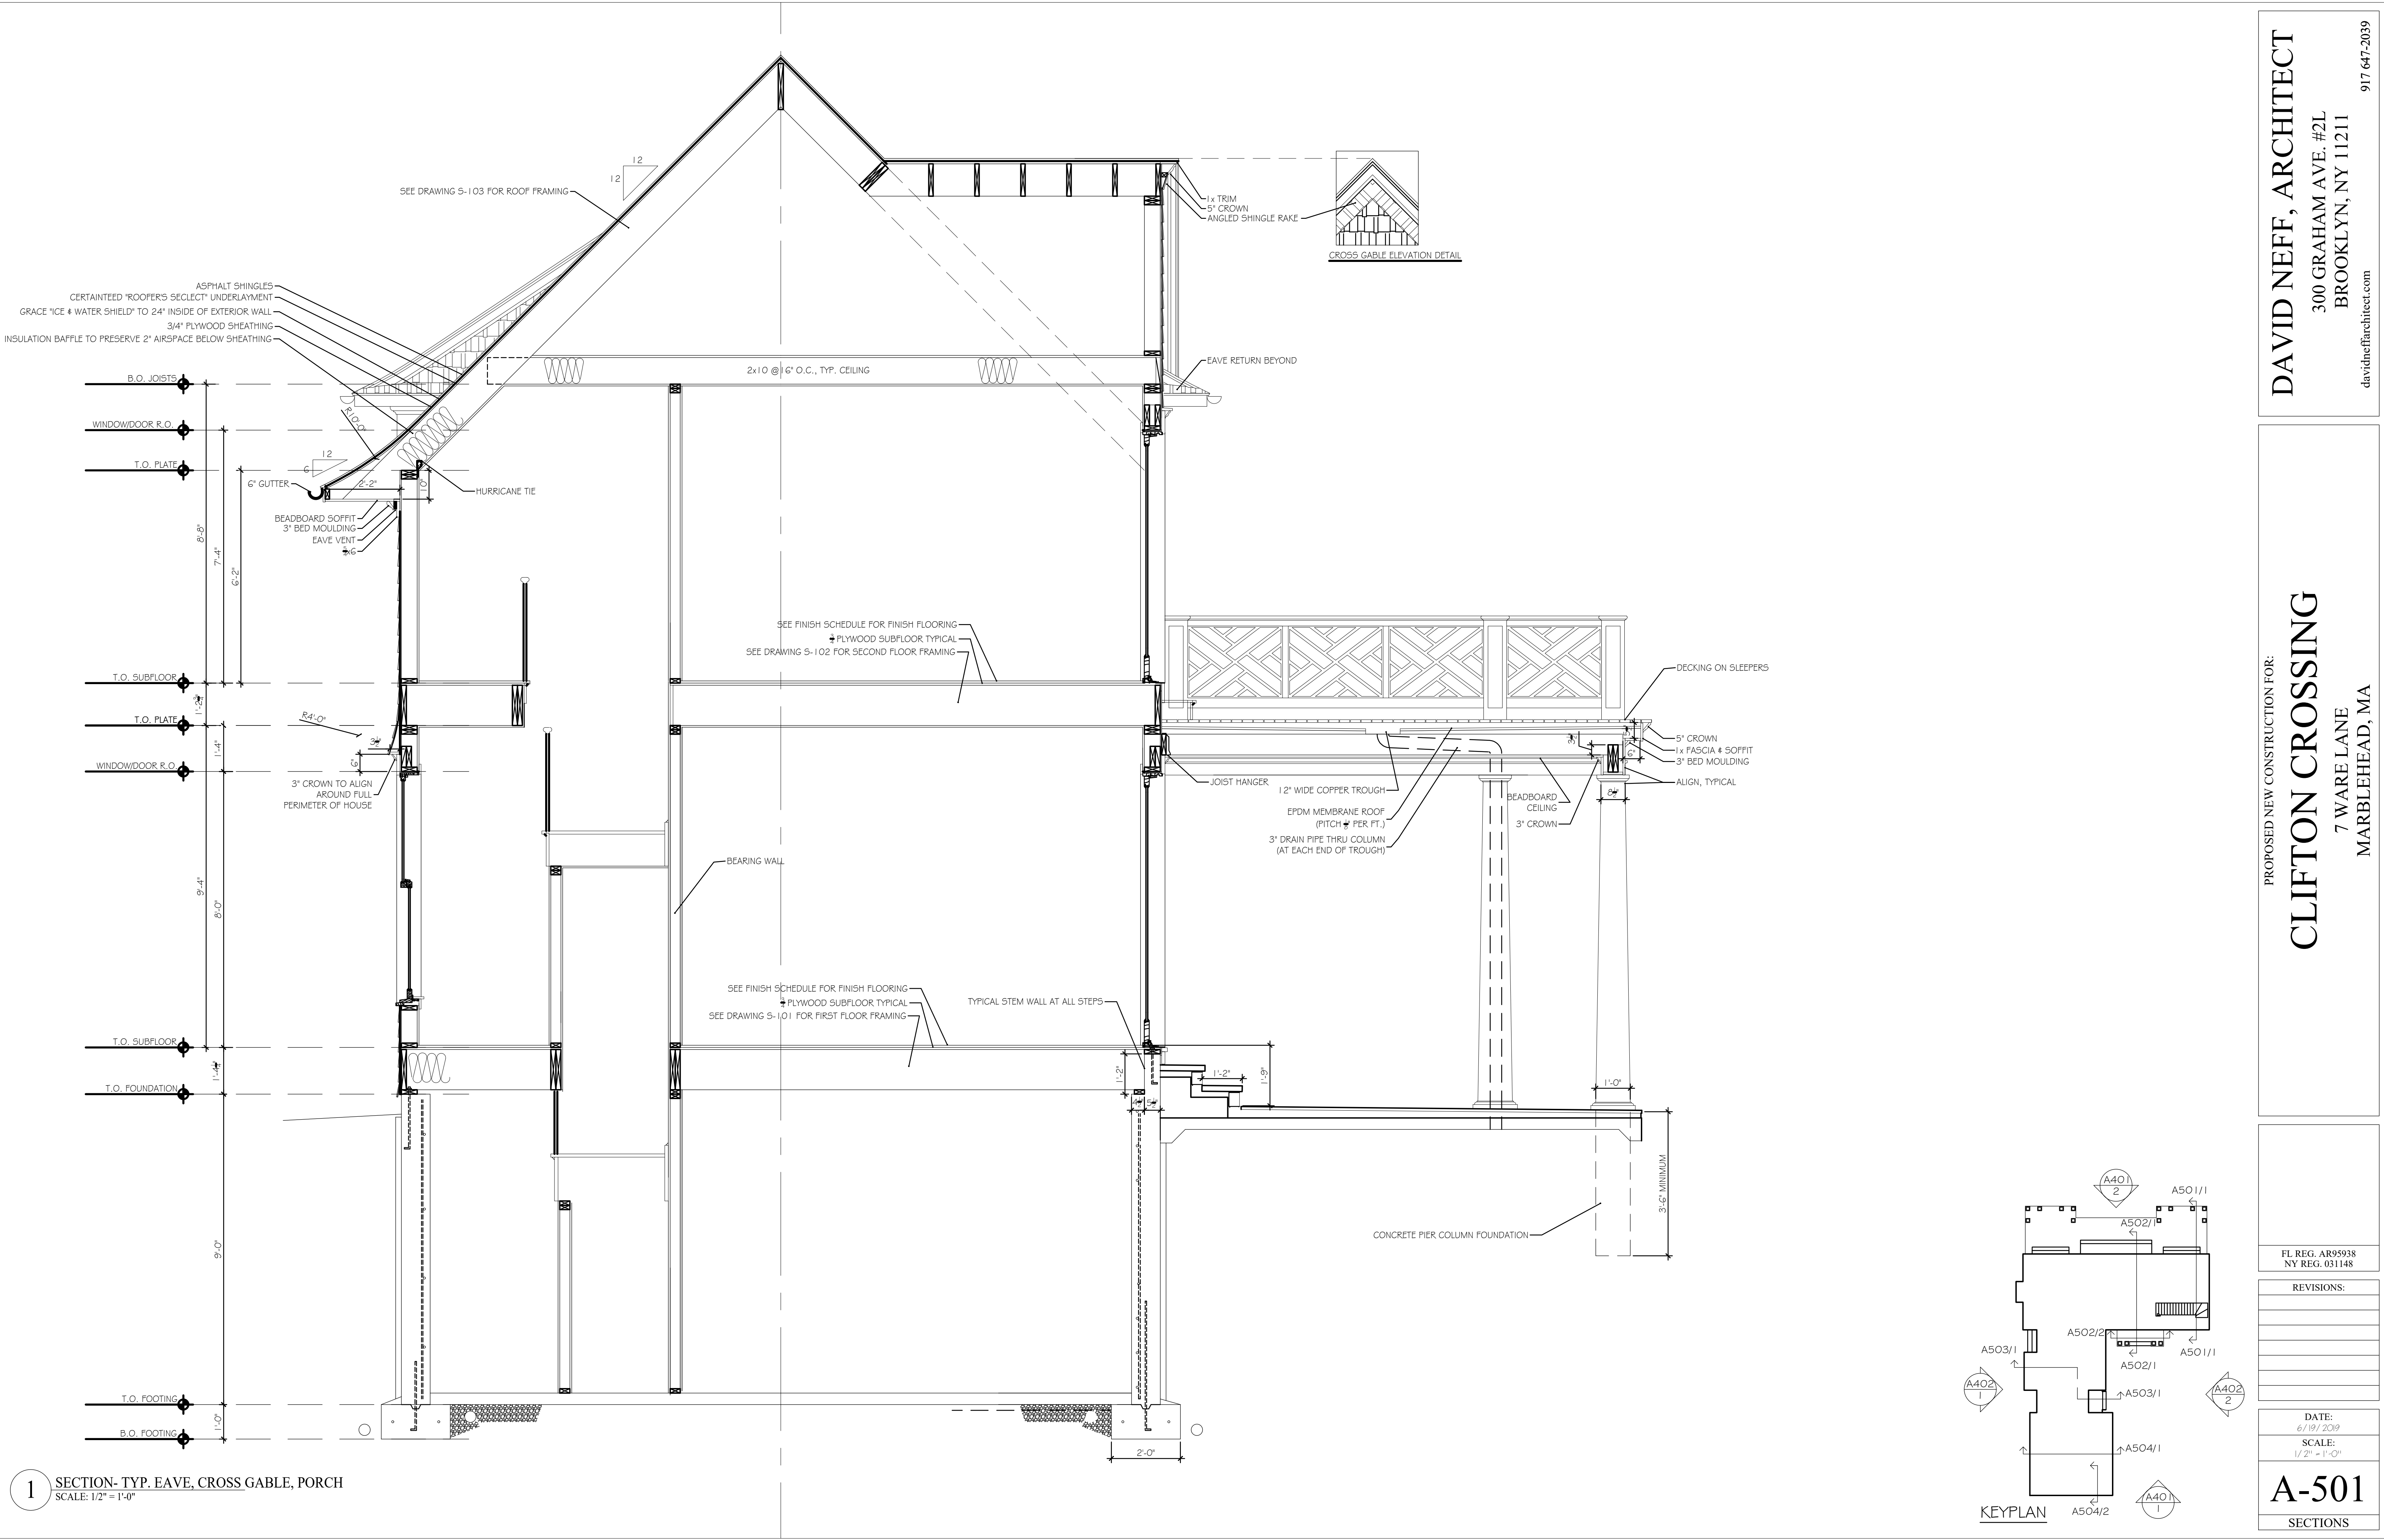

1 SECTION- TYP. EAVE, CROSS GABLE, PORCH
SCALE: 1/2" = 1'-0"

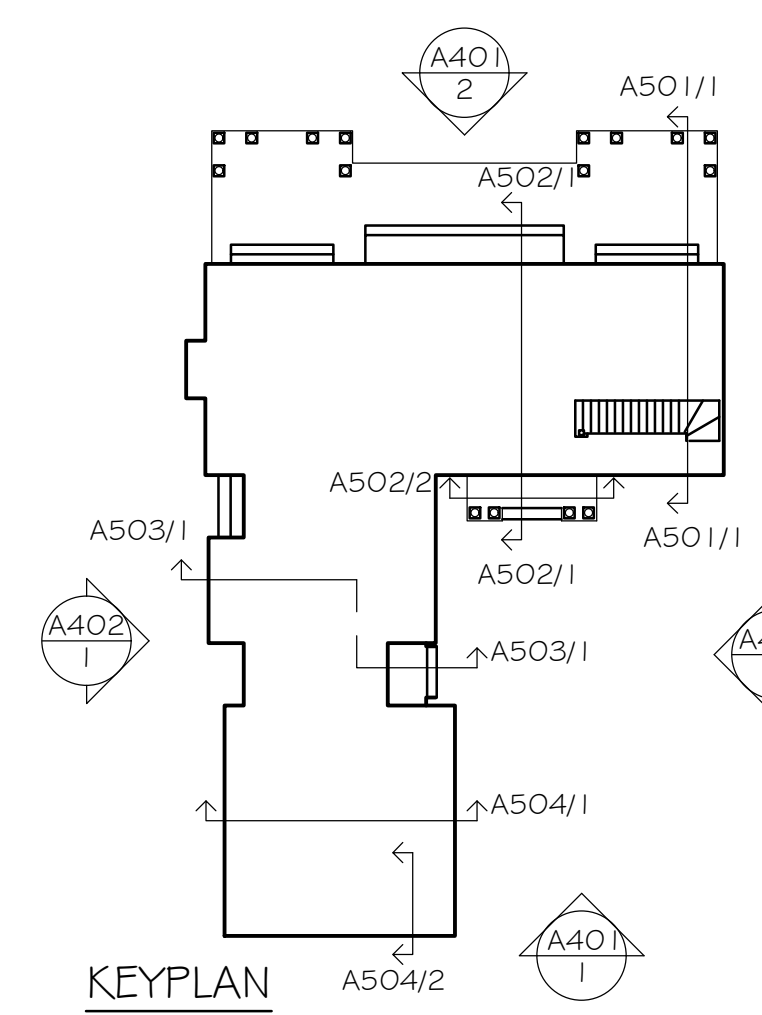

DAVID NEFF, ARCHITECT
300 GRAHAM AVE. #2L
BROOKLYN, NY 11211
davidneffarchitect.com
917 647-2039

PROPOSED NEW CONSTRUCTION FOR:
CLIFTON CROSSING
7 WARE LANE
MARBLEHEAD, MA

FL REG. AR95938
NY REG. 031148

REVISIONS:

DATE:
6/18/2019
SCALE:
1/2" = 1'-0"


A-501
SECTIONS


300 GRAHAM AVE. #2L
BROOKLYN, NY 11211
davidneffarchitect.com 917 647-2030

CLIFTON CROSSING


7 WARE LANE
MARBLEHEAD, MA

SECTIONS

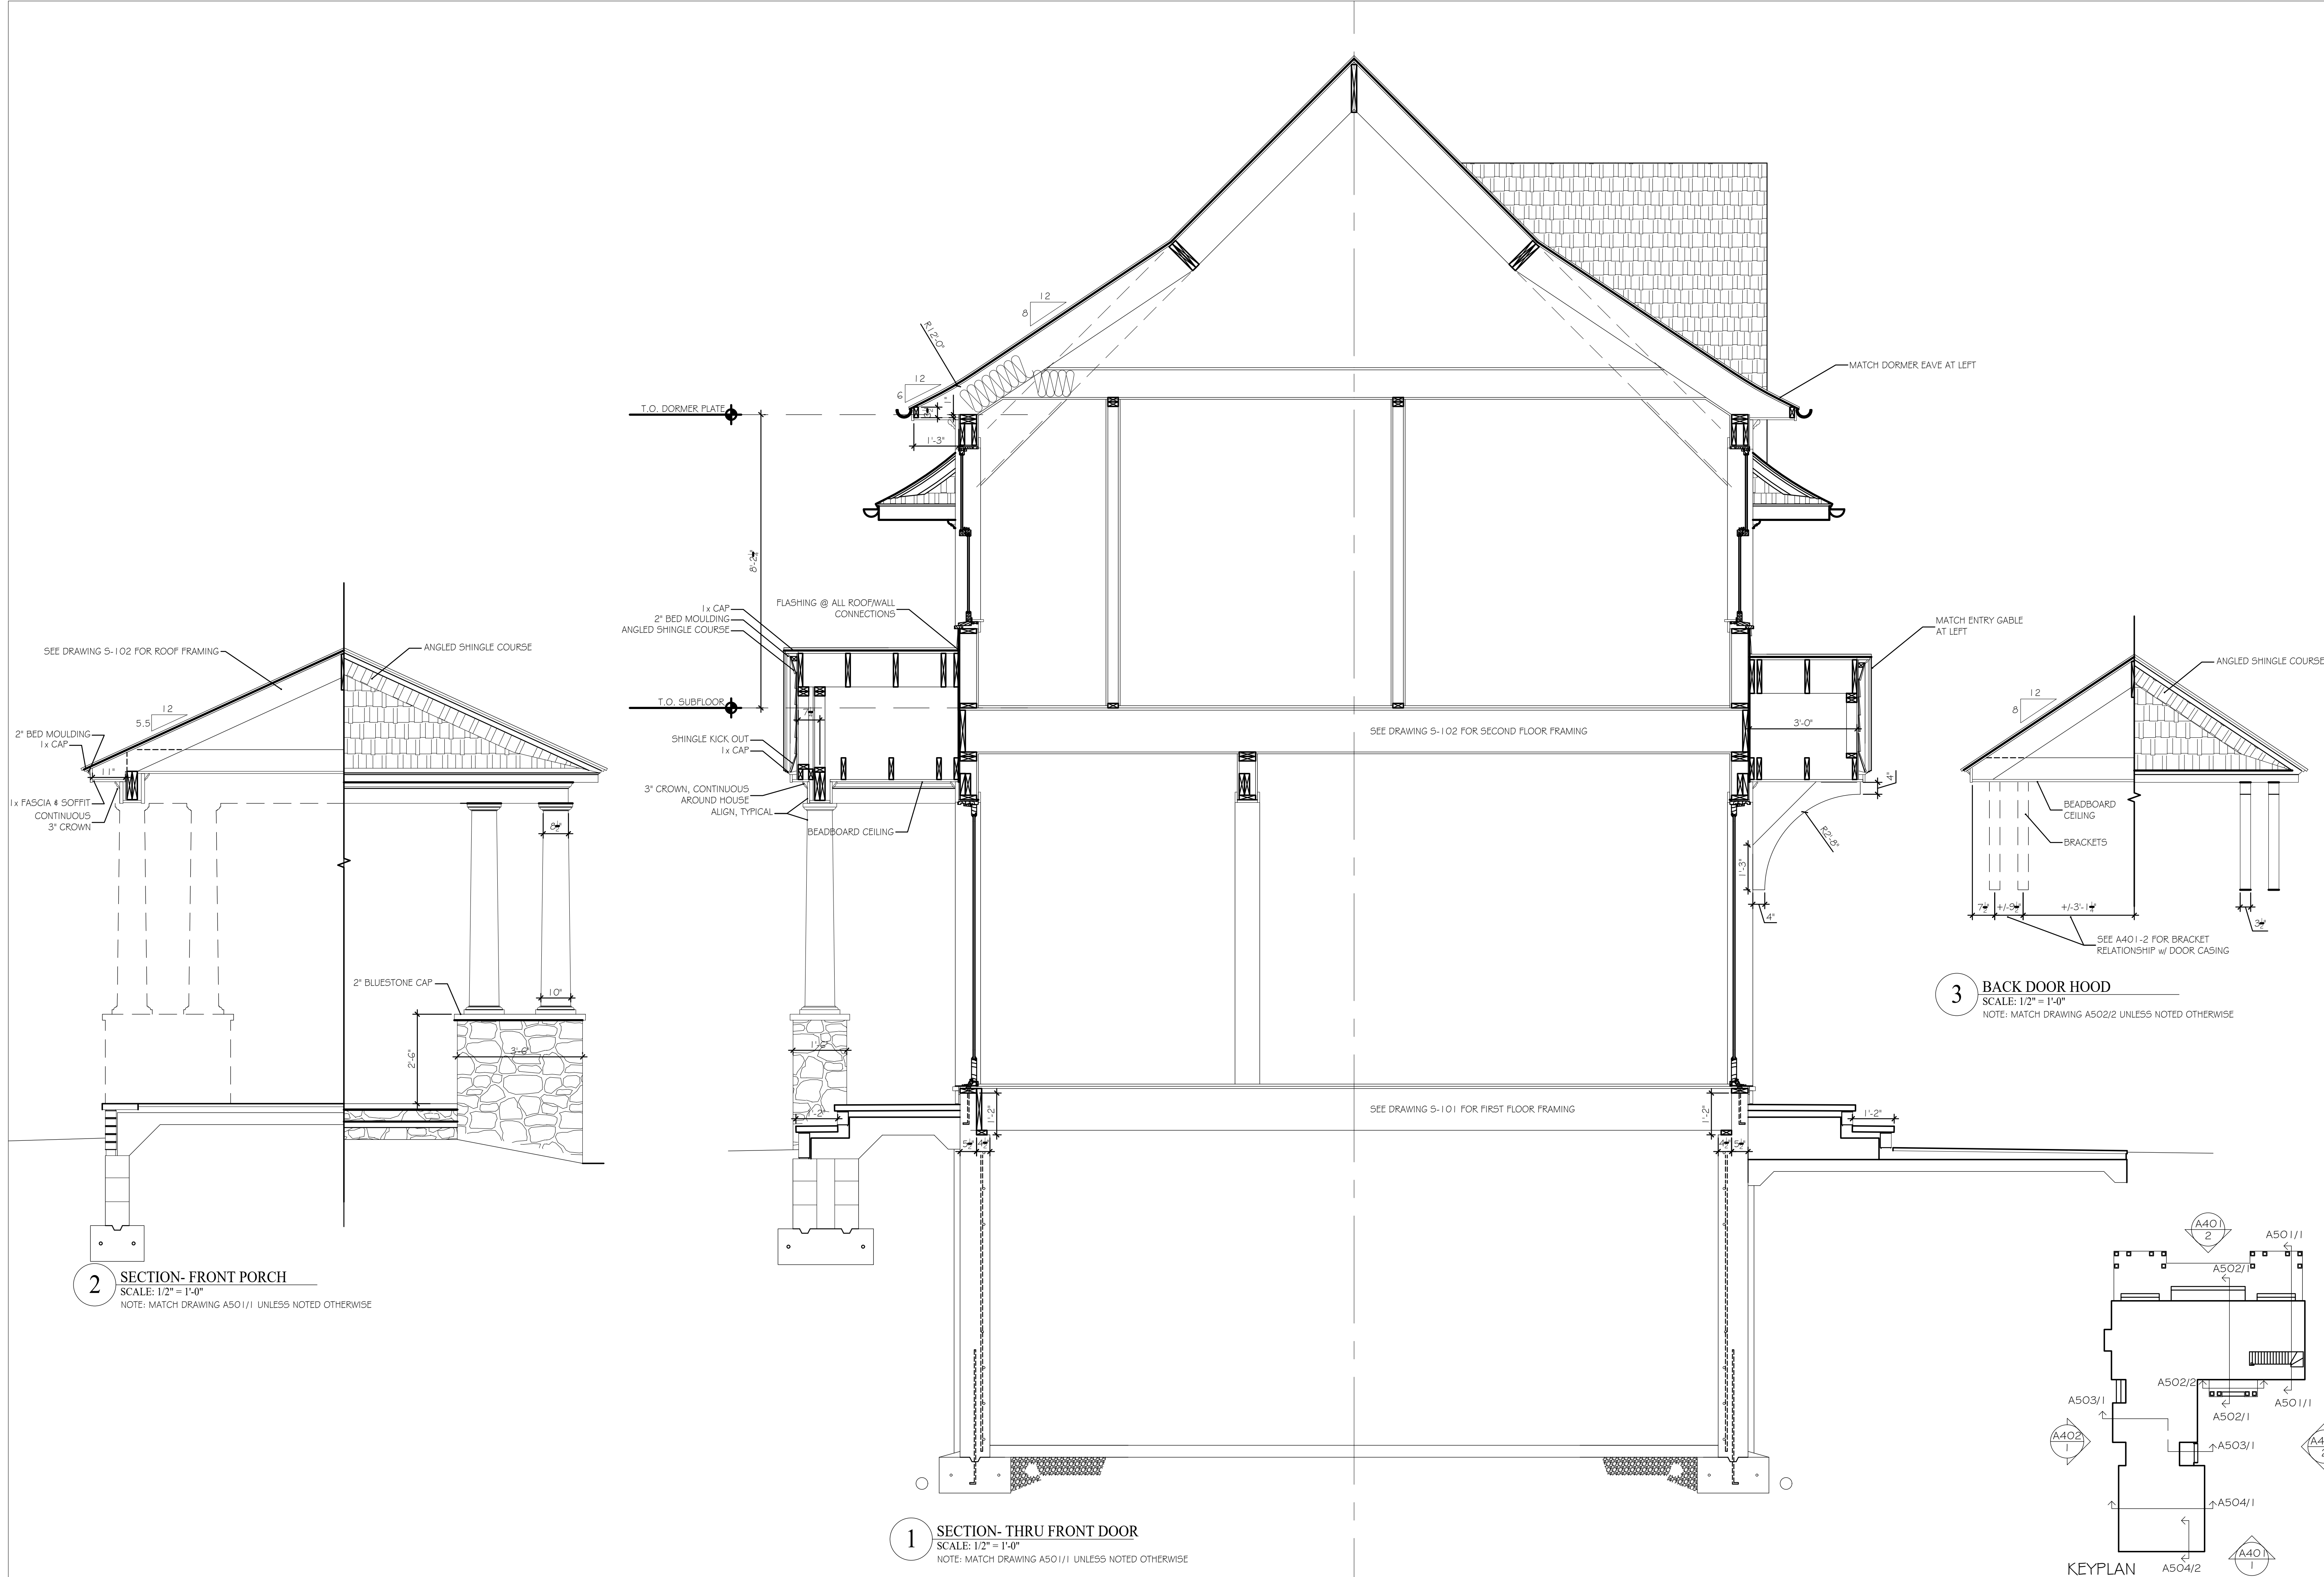

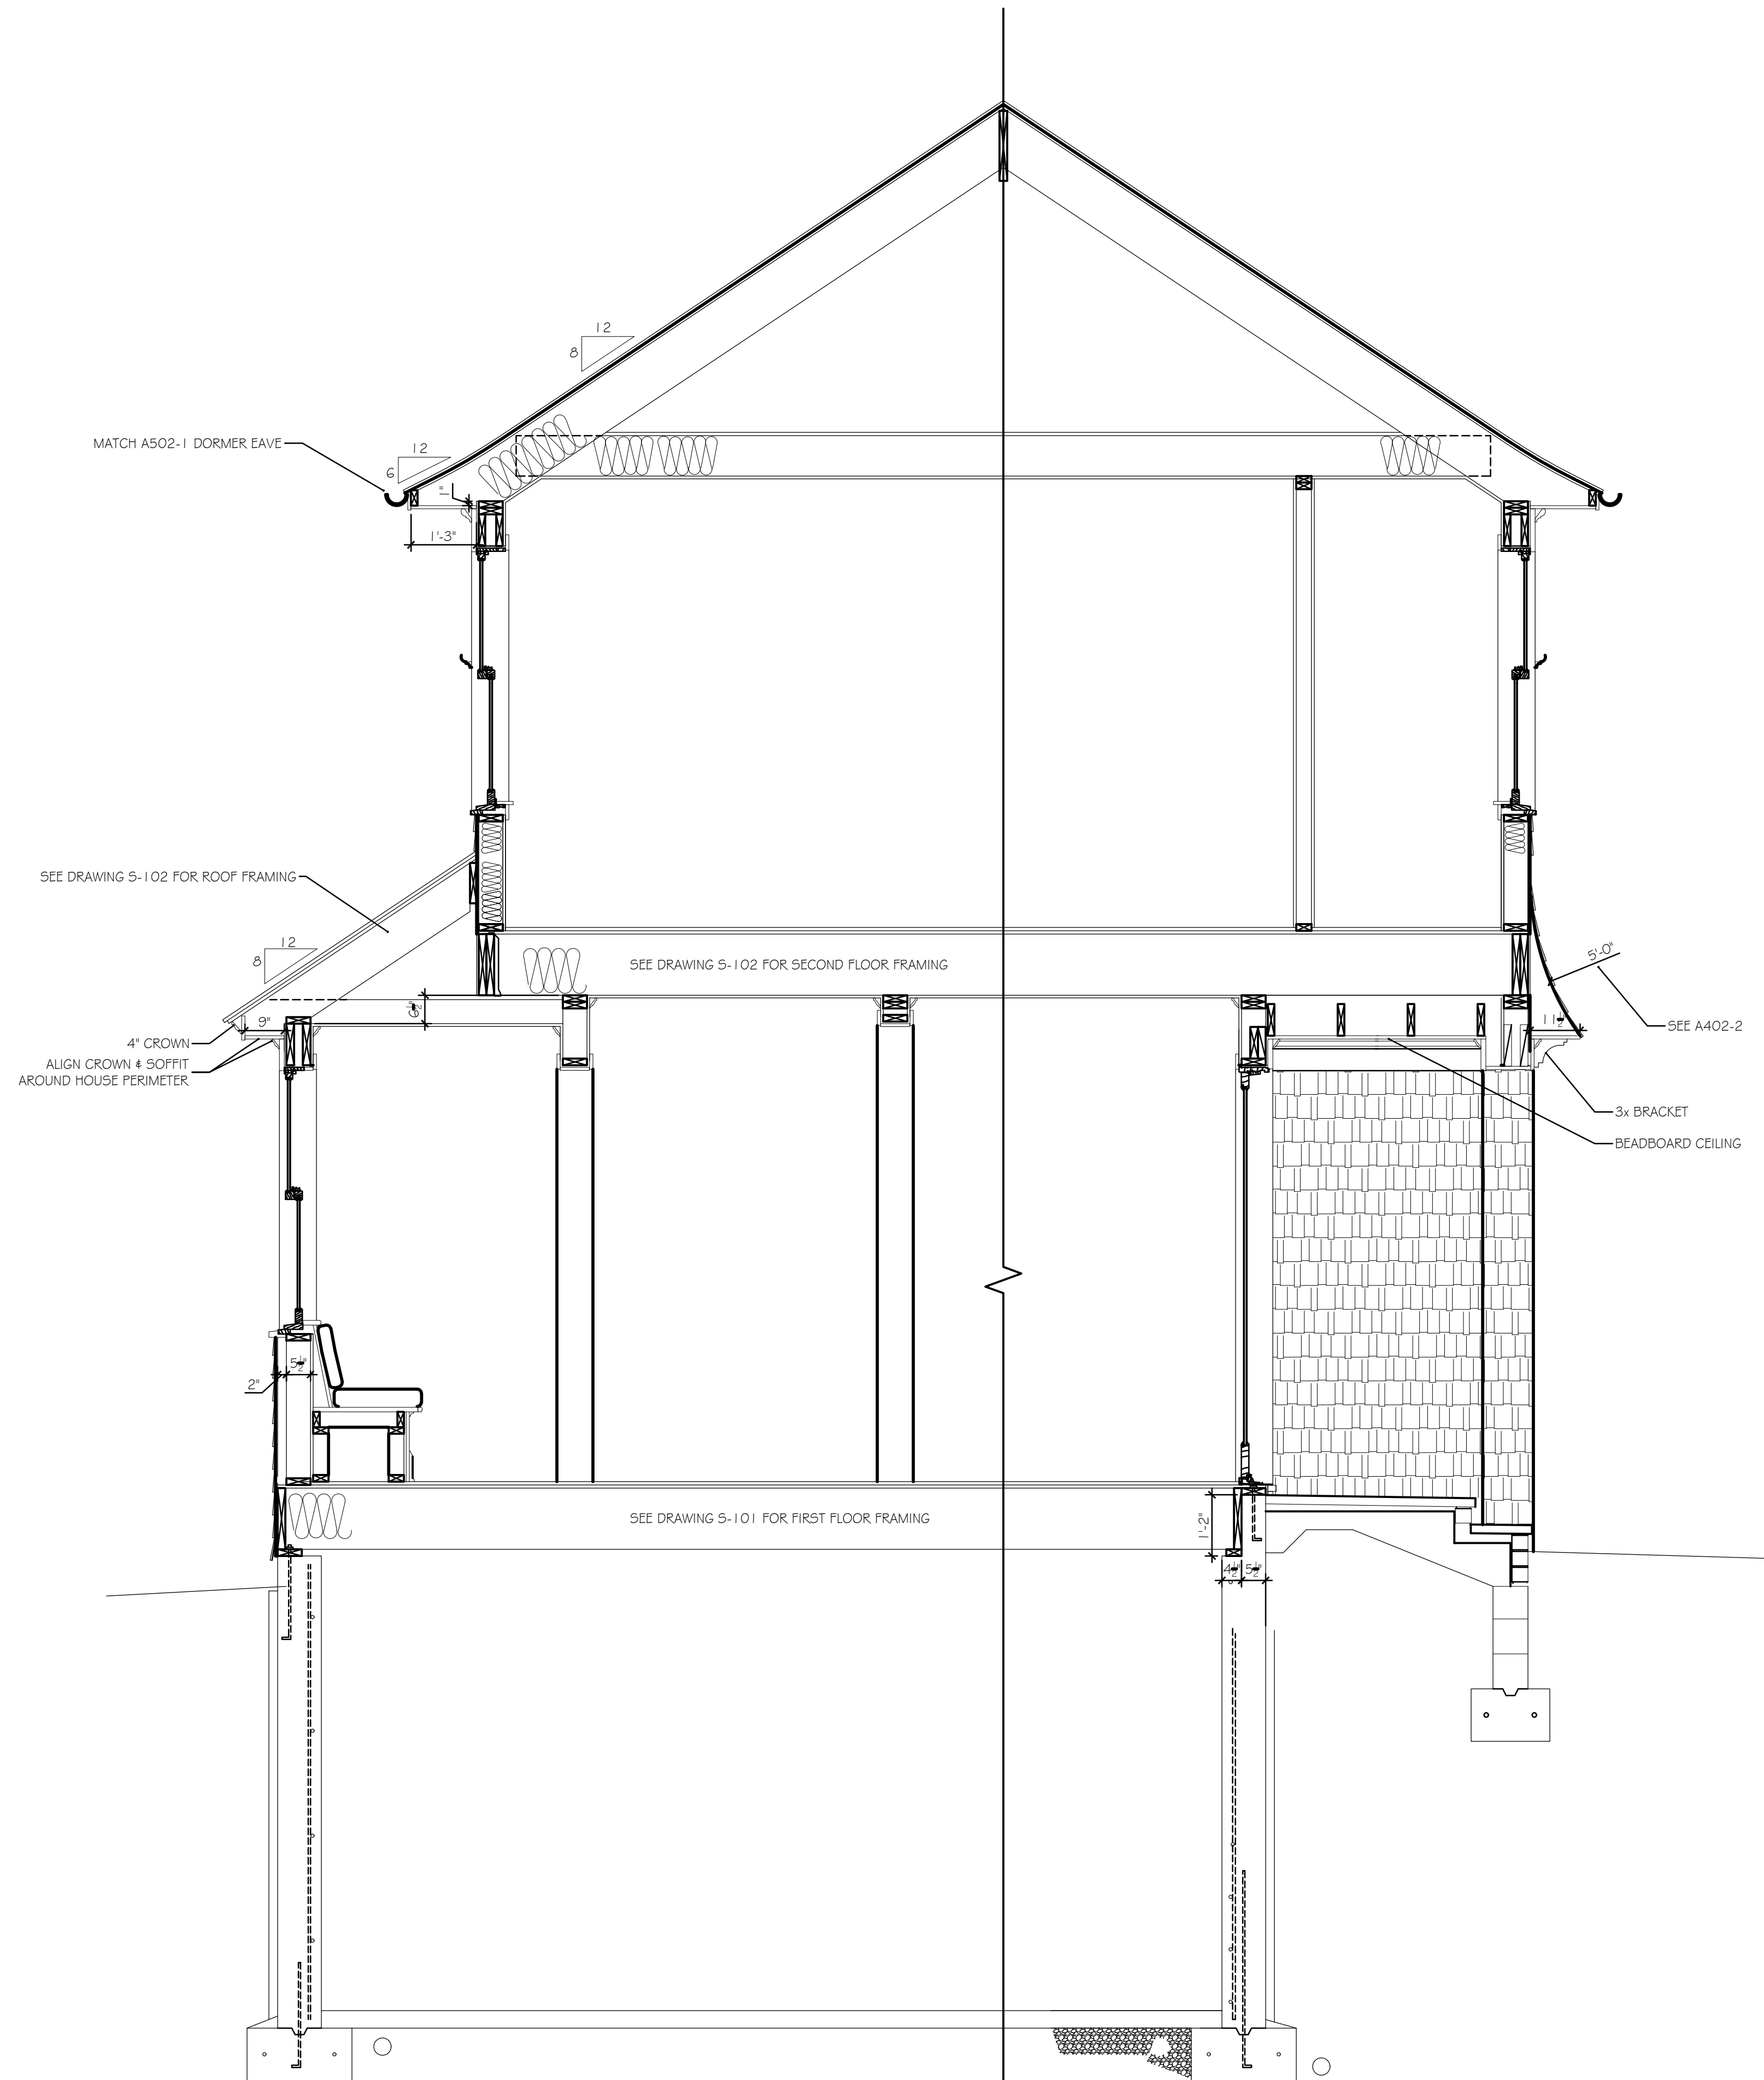

1 SECTION- MUDROOM PORCH/BREAKFAST BAY
SCALE: 1/2" = 1'-0"
NOTE: MATCH DRAWING A501/1 UNLESS NOTED OTHERWISE

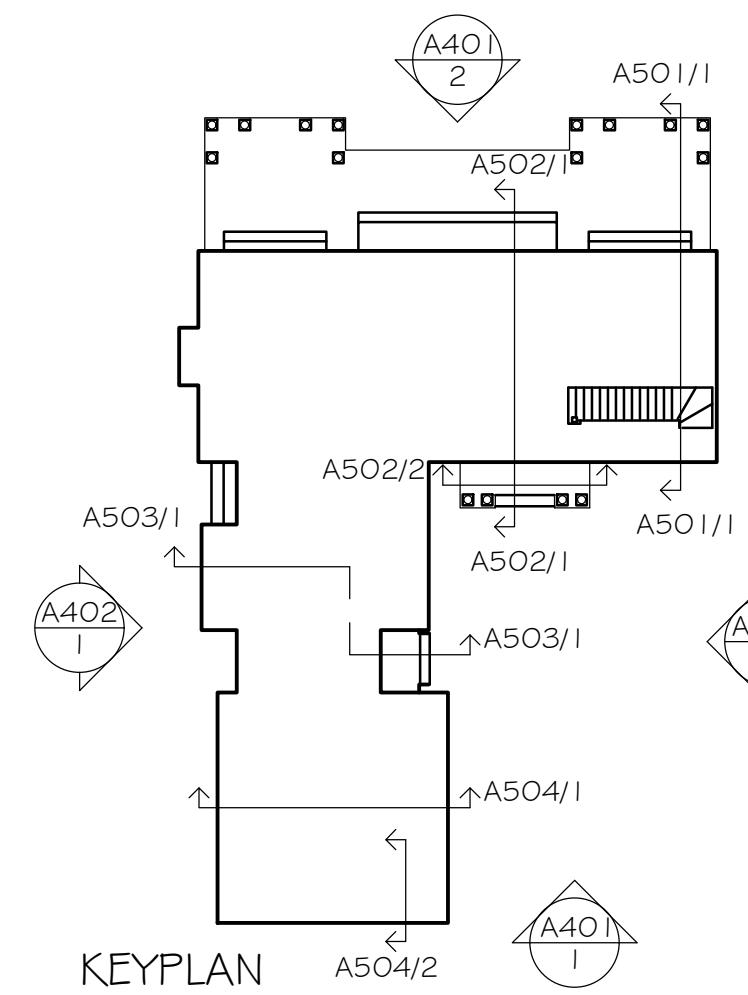

DAVID NEFF, ARCHITECT
300 GRAHAM AVE. #2L
BROOKLYN, NY 11211
davidneffarchitect.com 917 647-2039


PROPOSED NEW CONSTRUCTION FOR:
CLIFTON CROSSING
7 WARE LANE
MARBLEHEAD, MA

FL REG. AR95938
NY REG. 031148


REVISIONS:

DATE:
6/19/2019
SCALE:
1/2" = 1'-0"

A-503
SECTIONS

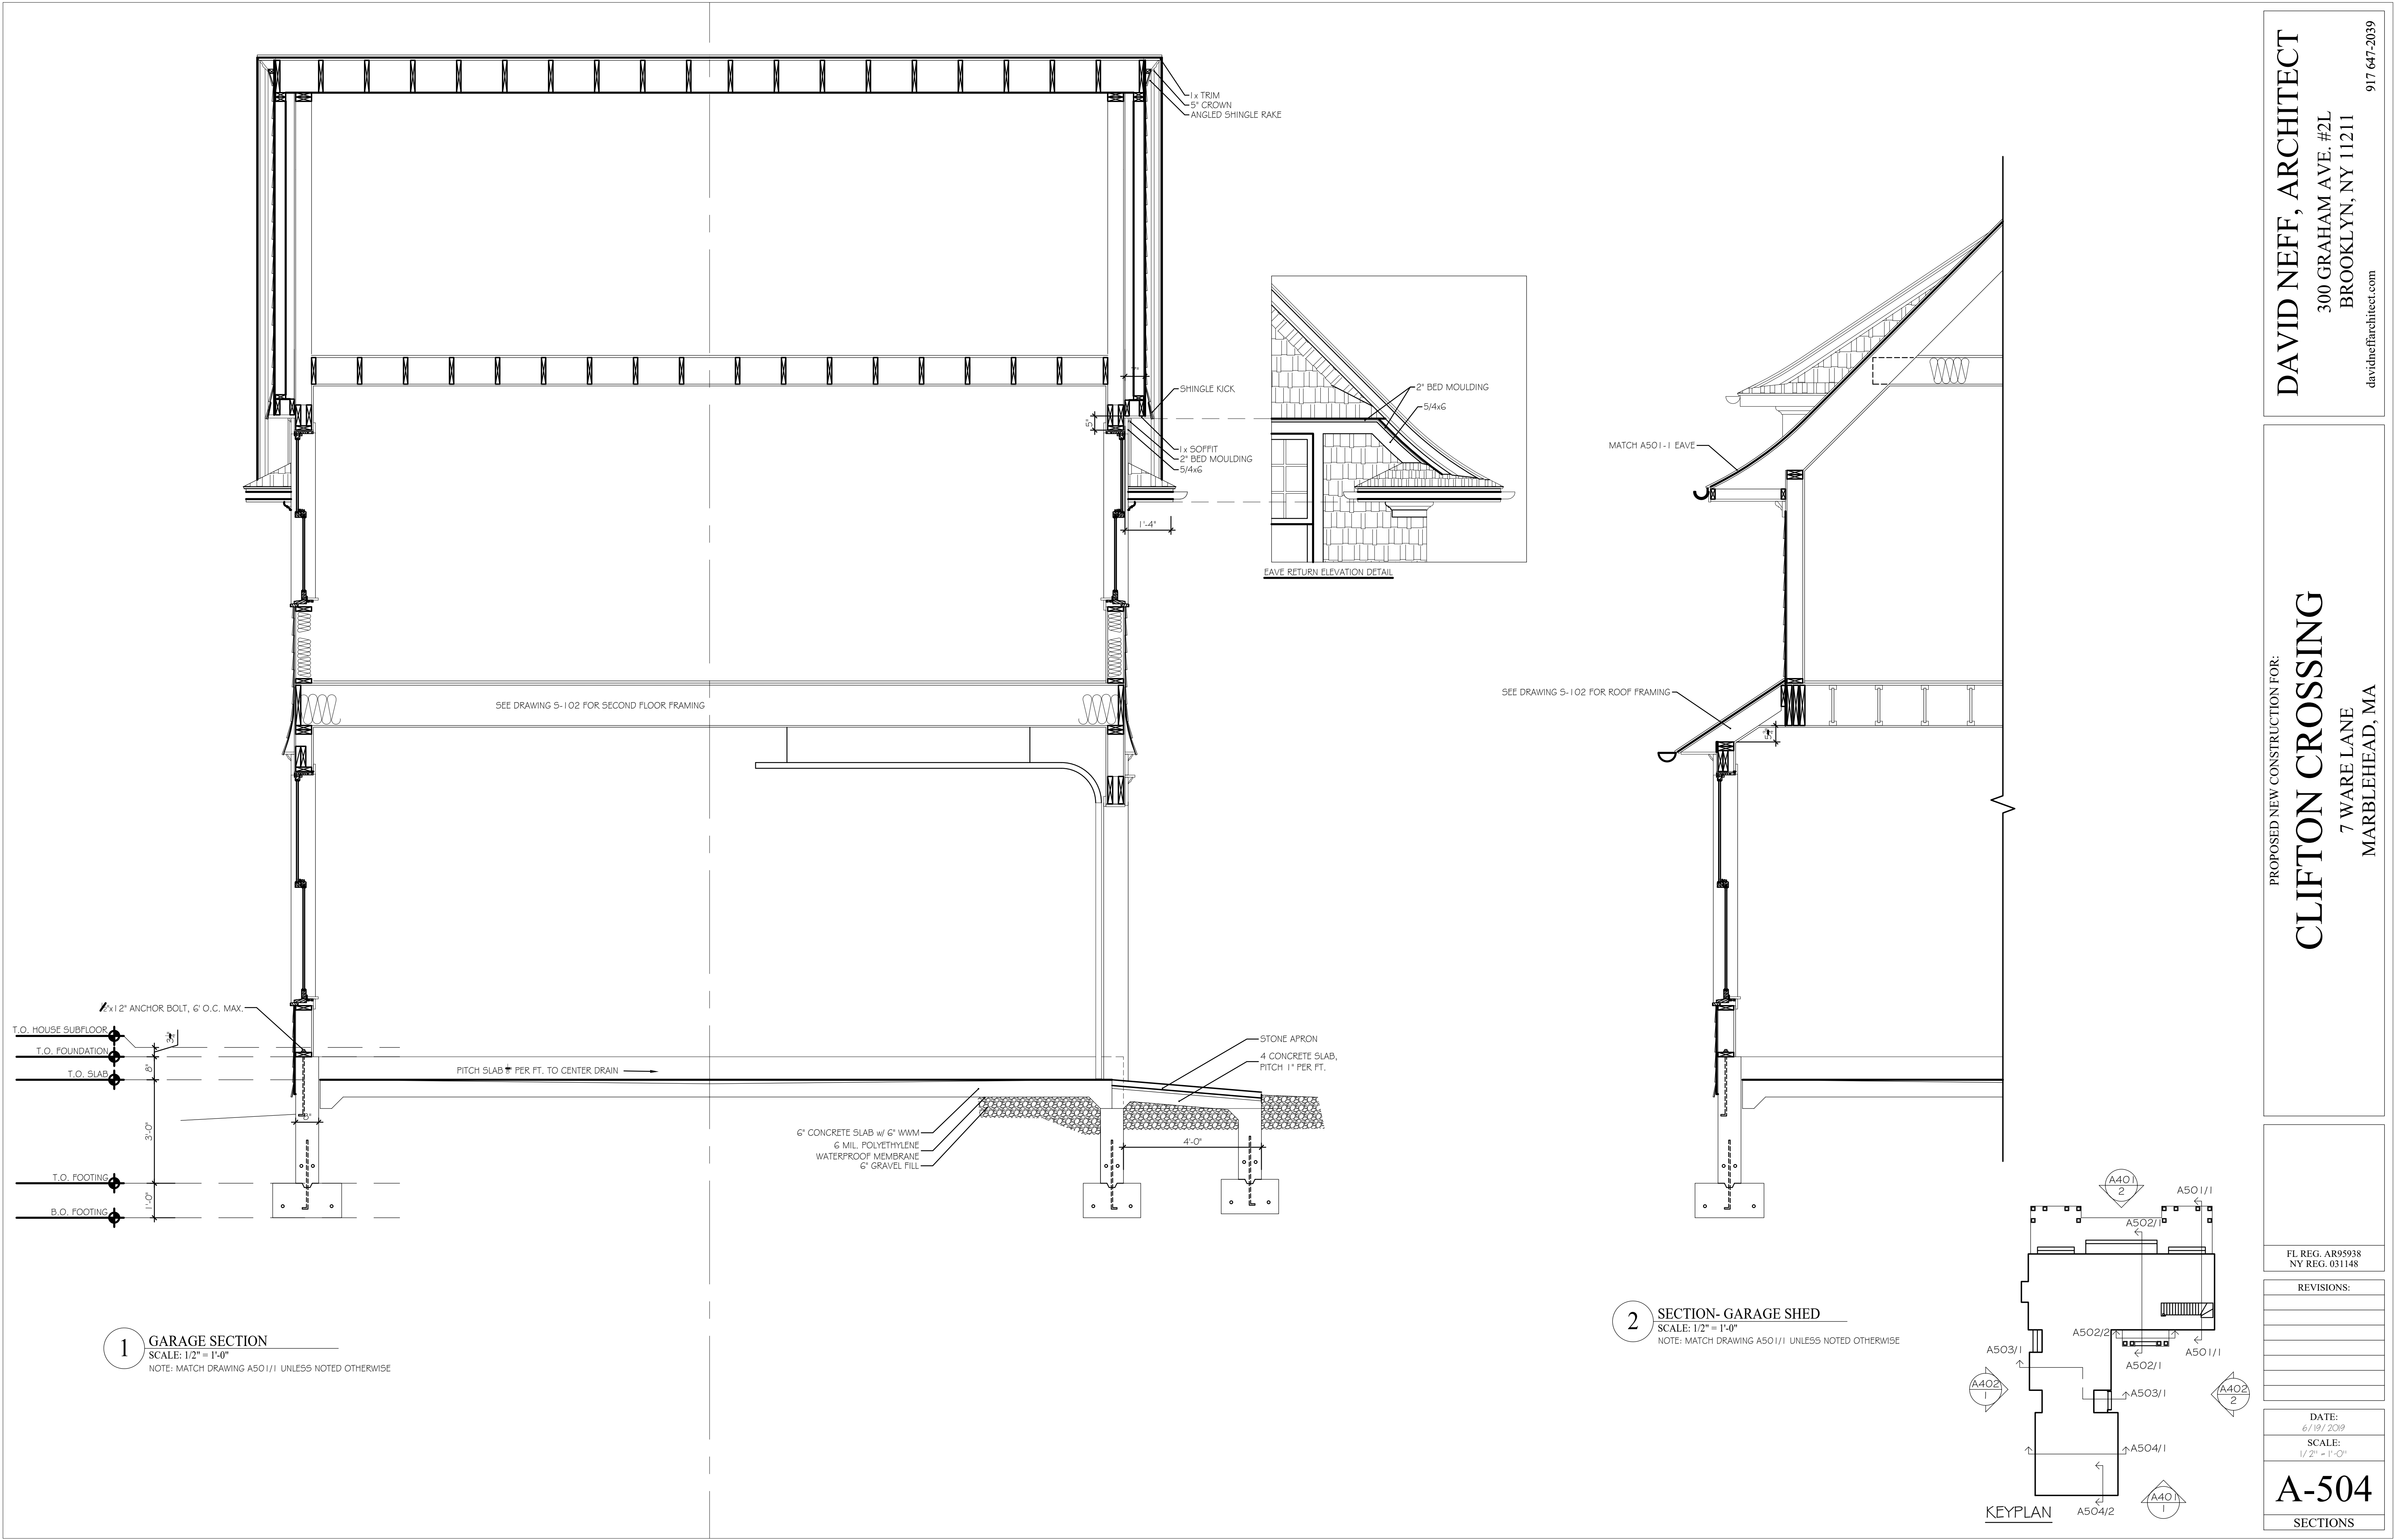


WINDOW SCHEDULE			
#	MANUFACTURER	SASH OPENING	COMMENTS
A	TBD	3'-4" x 6'-6"	
B		3'-0" x 5'-2"	EGRESS CODE-COMPLIANT
C		3'-4" x 4'-10"	COTTAGE DOUBLE HUNG, SEE TOP SASH DIMENSION AT RIGHT
D		2'-8" x 4'-10"	COTTAGE DOUBLE HUNG, SEE TOP SASH DIMENSION AT RIGHT
NOTES:			
1	ALL WINDOWS TO BE LOW-E, DOUBLE GLAZED, SDL		
2	ALL SIZES ABOVE ARE FOR WINDOW SASH OPENING, NOT OVERALL FRAME SIZE		

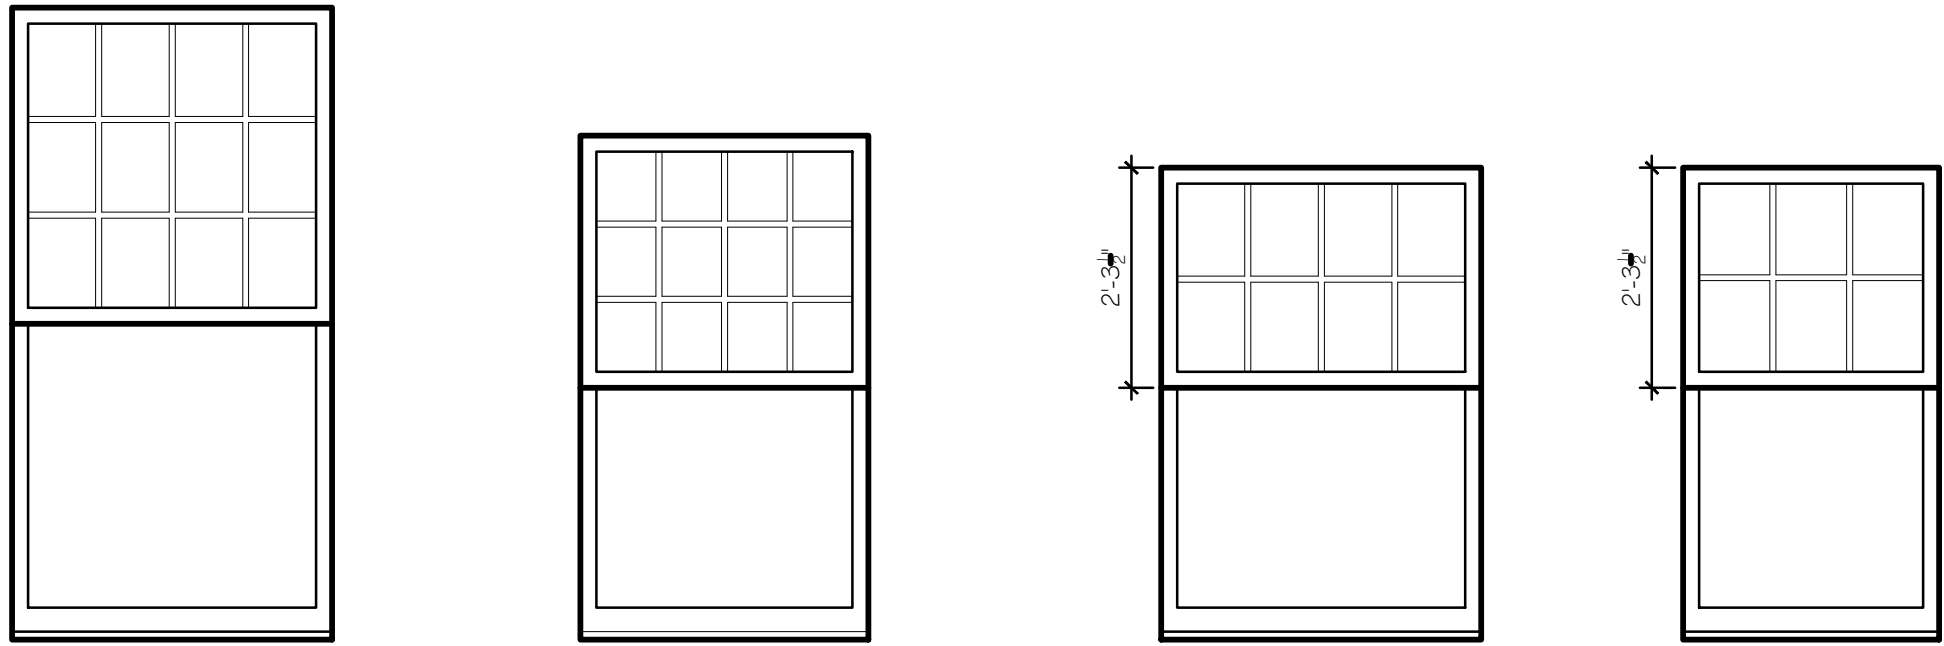


A B C D

EXTERIOR DOOR SCHEDULE			
#	MANUFACTURER	SIZE	COMMENTS
1	TBD	3'-4" x 8'-0"	SIDELIGHTS
2			
3		5'-4" x 8'-0"	
4			
5		5'-4" x 8'-0"	SIDELIGHTS
6		5'-4" x 8'-0"	SIDELIGHTS
7		3'-0" x 8'-0"	
8		3'-0" x 8'-0"	
9		3'-0" x 7'-0"	FIRE-RATED
10		9'-0" x 8'-0"	
11		9'-0" x 8'-0"	
12		3'-0" x 7'-2"	
13		3'-0" x 7'-2"	
NOTES:			
1.	GLASS DOORS TO BE LOW-E, DOUBLE GLAZED, SDL		

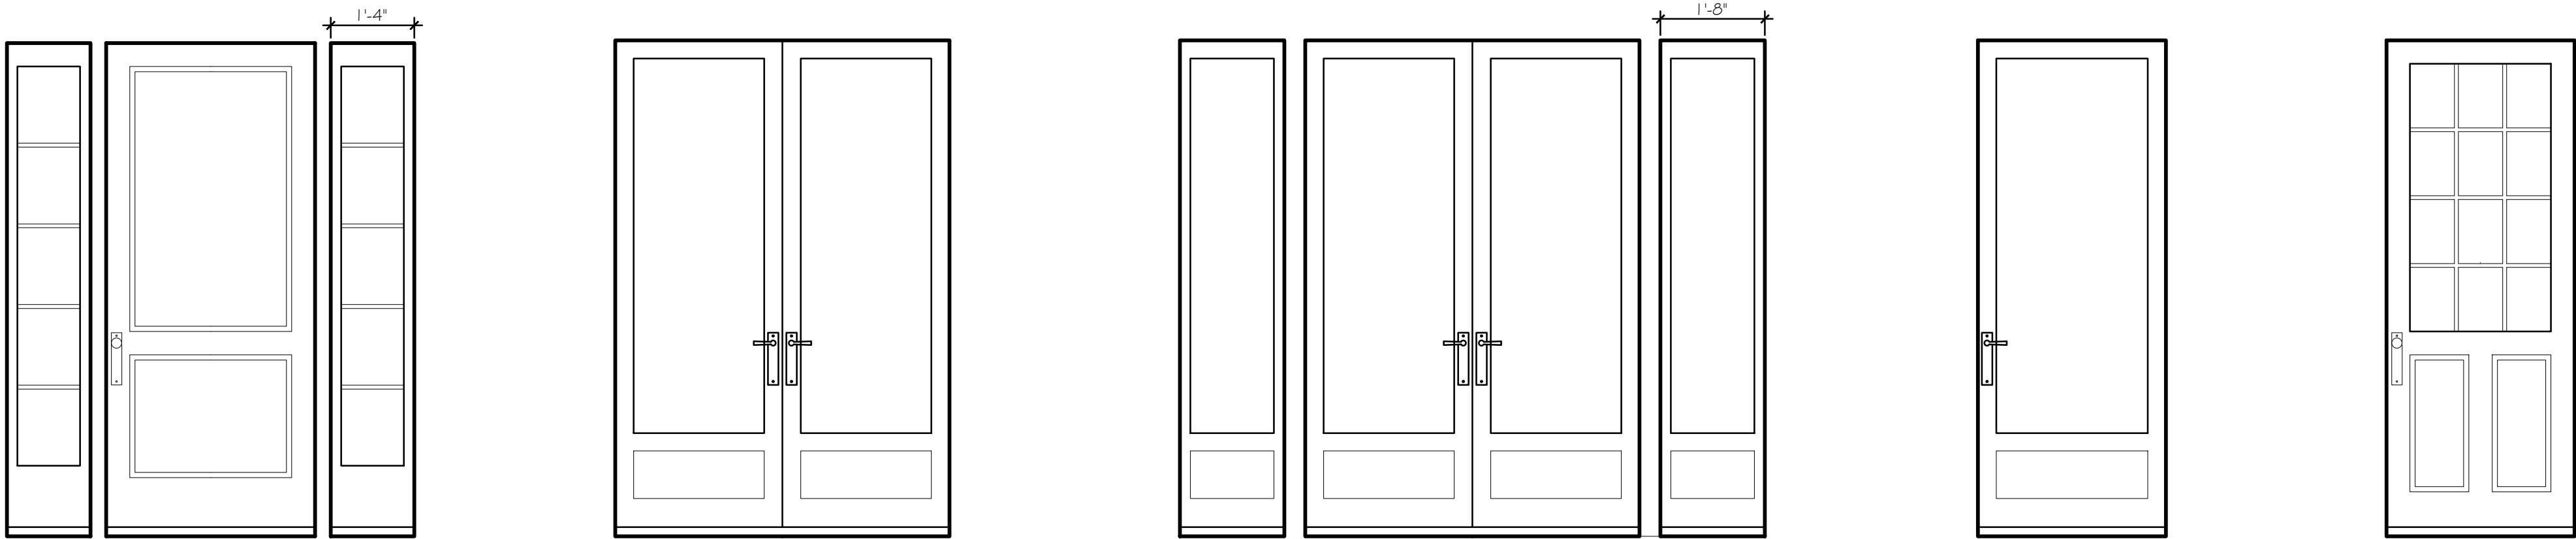


DOOR 1 DOOR 3 DOOR 5 & 6 DOOR 7 DOOR 8


INTERIOR DOOR SCHEDULE					
#	MANUFACTURER	W	H	HWARE GROUP	COMMENTS
001	TBD	3'-0"	6'-8"		FIRE-RATED
101		2'-0"	7'-0"		
102		2'-8"	7'-0"		
103		2'-4"	7'-0"		
104		2'-8"	7'-0"		DOUBLE ACTION
105		2'-0"	7'-0"		
106		4'-0"	7'-10"		POCKET DOOR
201		2'-8"	7'-0"		
202		2'-6"	7'-0"		
203		2'-6"	7'-0"		
204		2'-8"	7'-0"		
205		2'-8"	7'-0"		
206		2'-6"	7'-0"		
207		2'-0"	7'-0"		
208		2'-6"	7'-0"		
209		2'-8"	7'-0"		
210		(2) 2'-0"	7'-0"		
211		2'-4"	7'-0"		
212		2'-8"	7'-0"		
213		2'-4"	7'-0"		
214		2'-8"	7'-0"		
215		2'-4"	7'-0"		
216		2'-6"	7'-0"		
217		2'-8"	7'-0"		POCKET DOOR
218		(2) 2'-6"	7'-0"		GLASS DOORS
NOTES:					
1.	DOORS TO BE 1 1/2" PAINT GRADE				

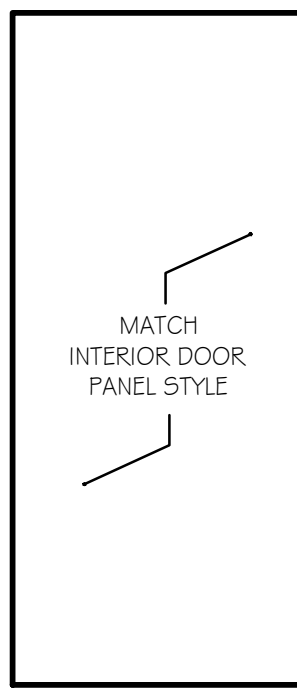

DOOR 9

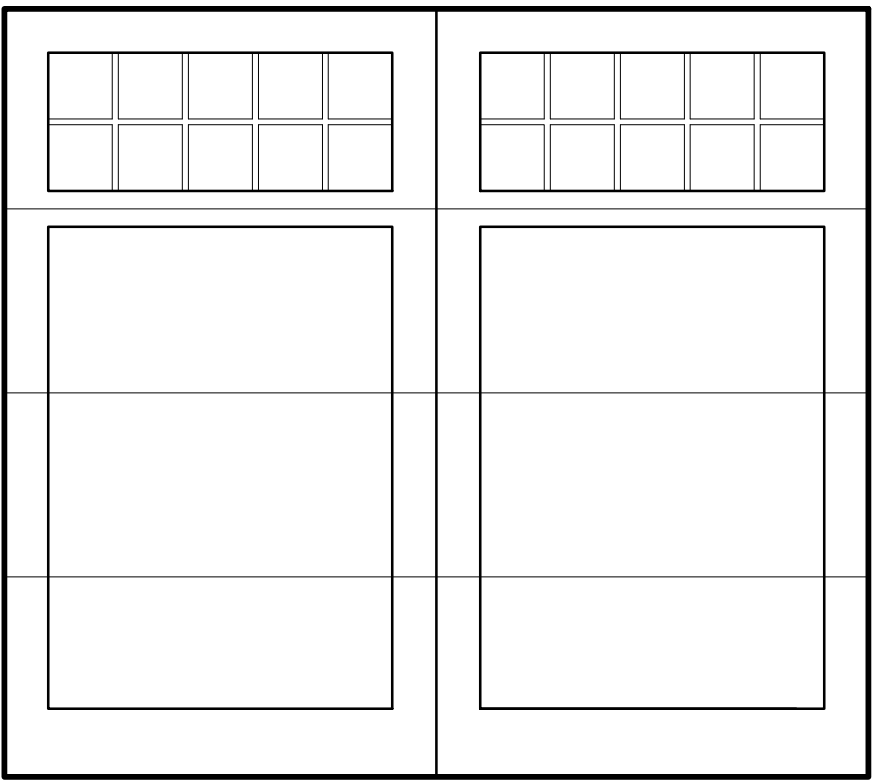

DOORS 10&11

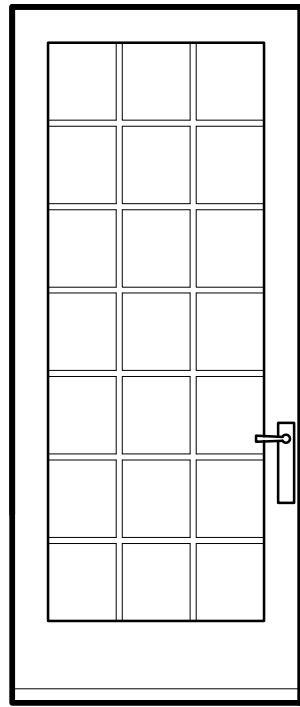

DOORS 12&13

DAVID NEFF, ARCHITECT
300 GRAHAM AVE. #2L
BROOKLYN, NY 11211
davidneffarchitect.com 917 647-2039

PROPOSED NEW CONSTRUCTION FOR:
CLIFTON CROSSING
7 WARE LANE
MARBLEHEAD, MA

FL REG. AR95938
NY REG. 031148

REVISIONS:

DATE:
6/19/2019
SCALE:
1/2" = 1'-0"

A-901

SCHEDULES