


ORIGINAL

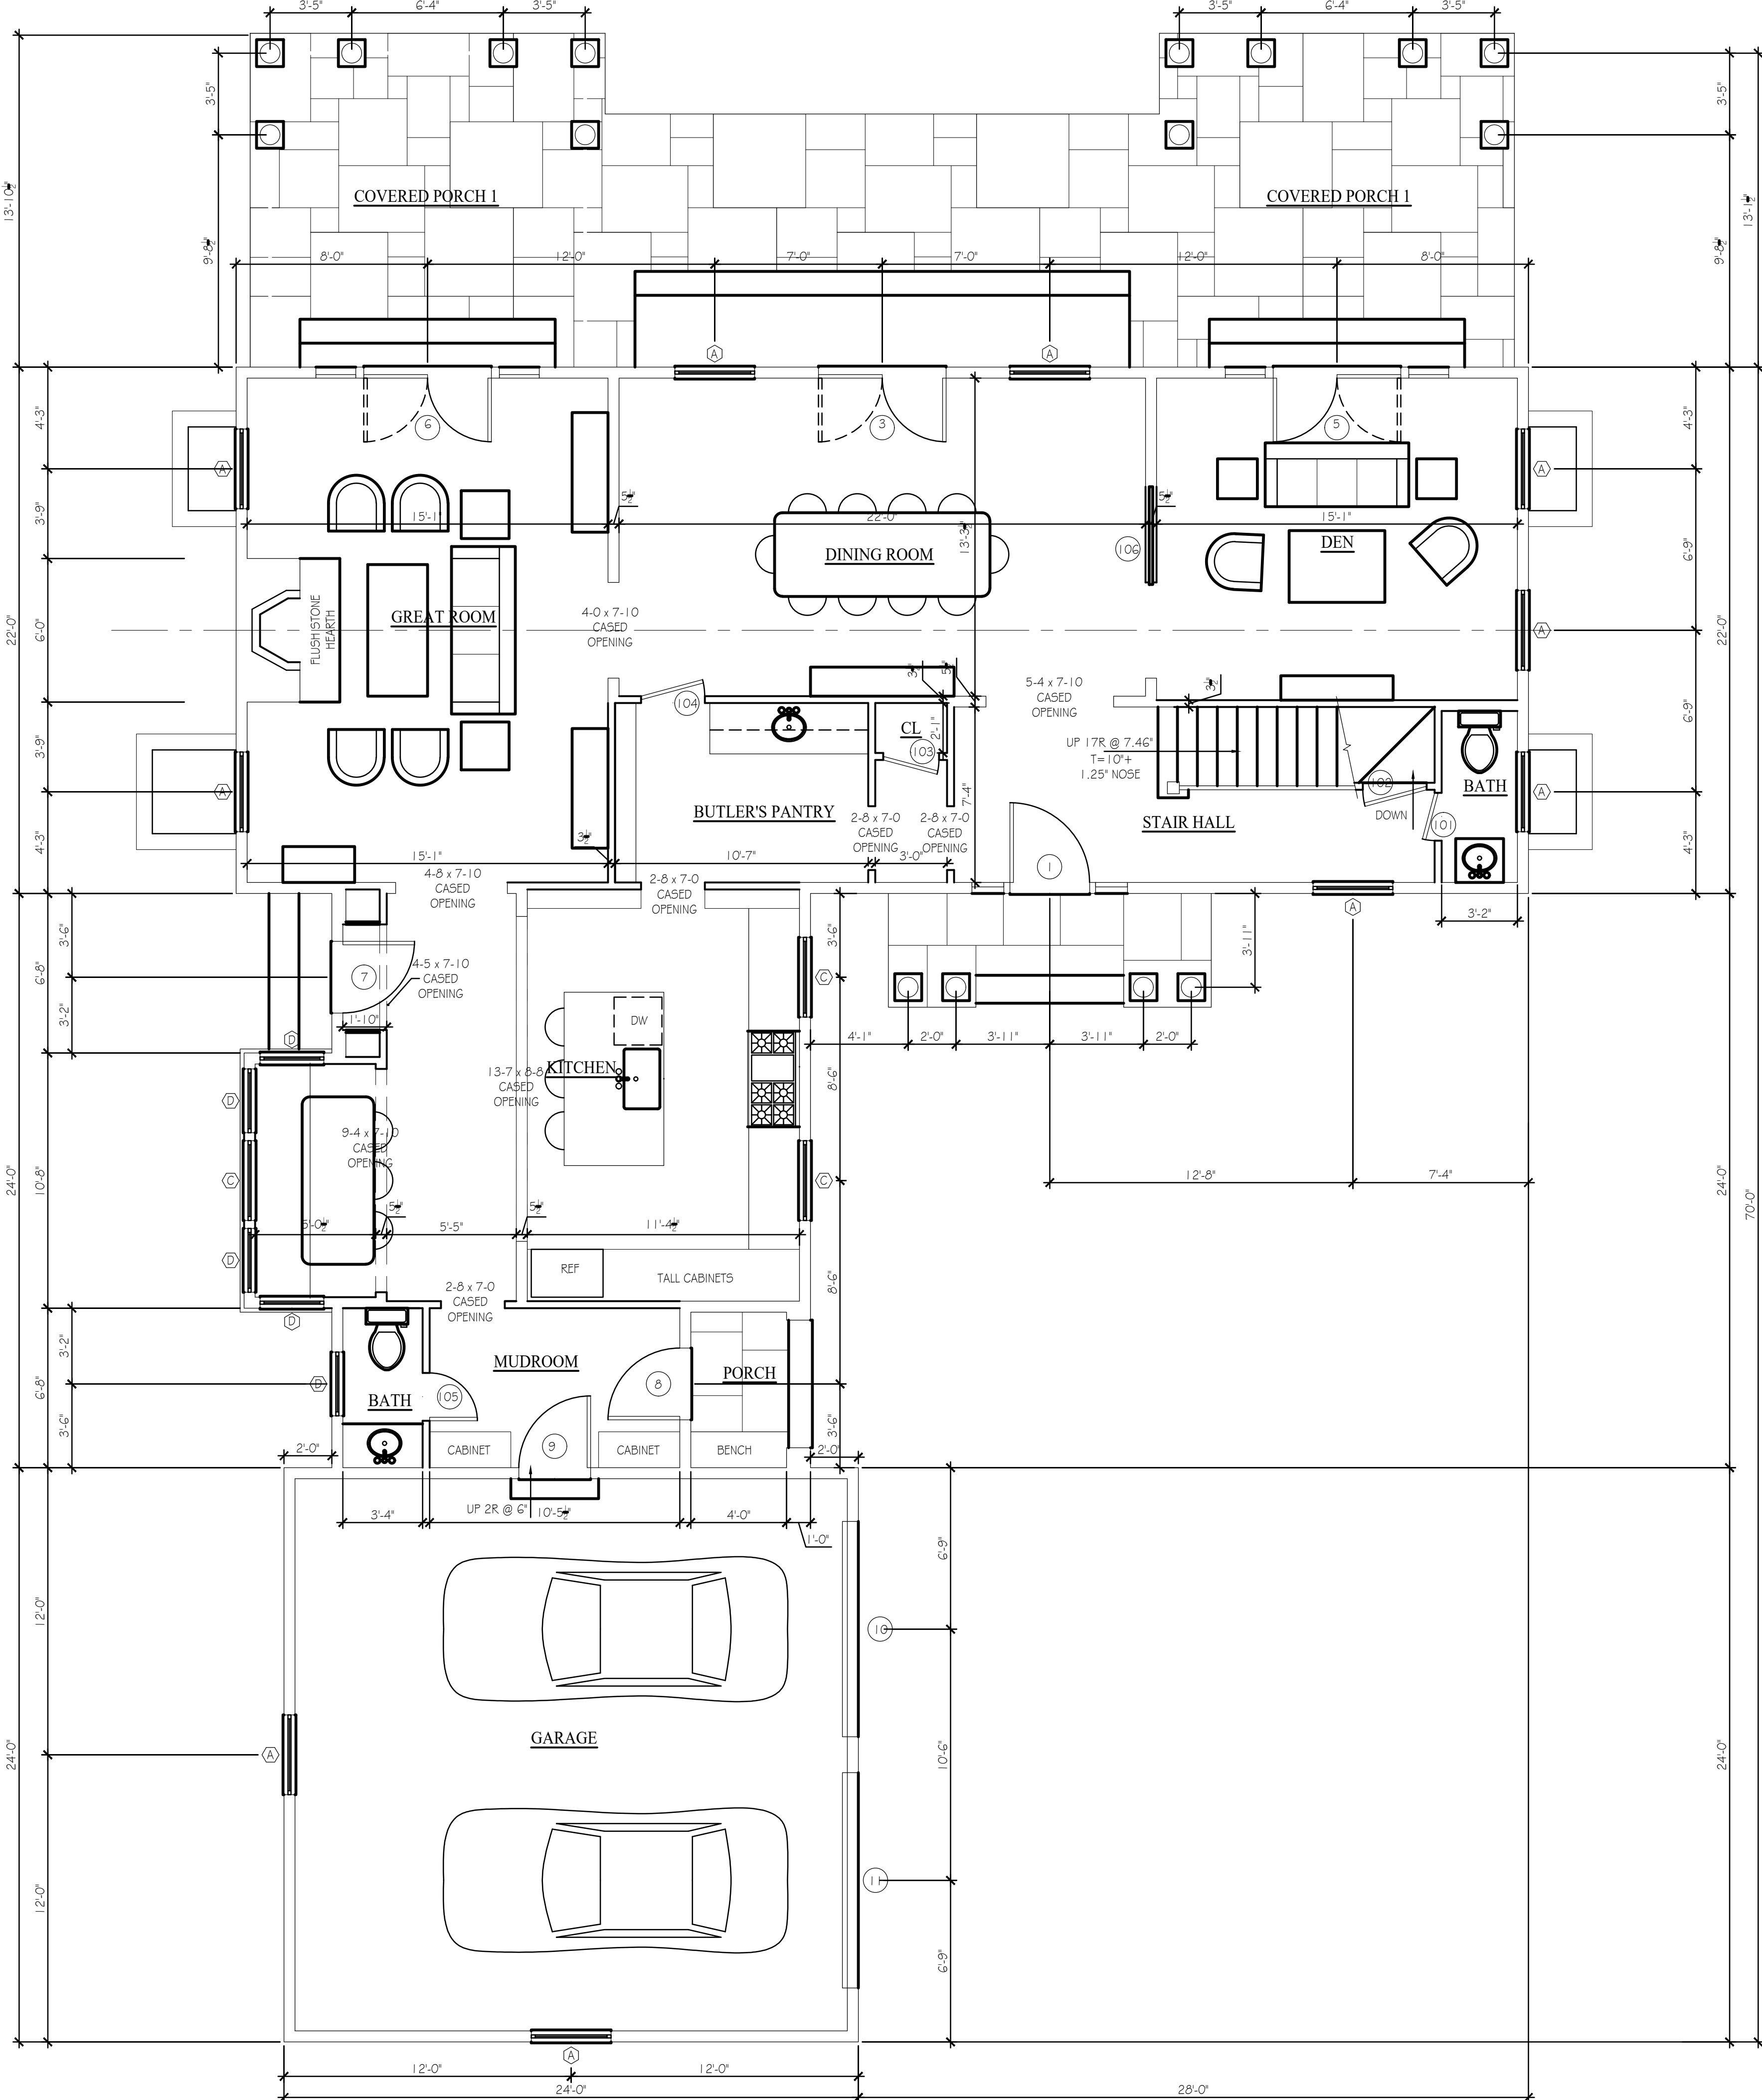

DAVID NEFF, ARCHITECT


BROOKLYN, NY 11211

davidneffarchitect.com 917 647-2039

PROPOSED NEW CONSTRUCTION FOR:

# CLIFTON CROSSING

7 WARE LANE  
MARBLEHEAD, MA

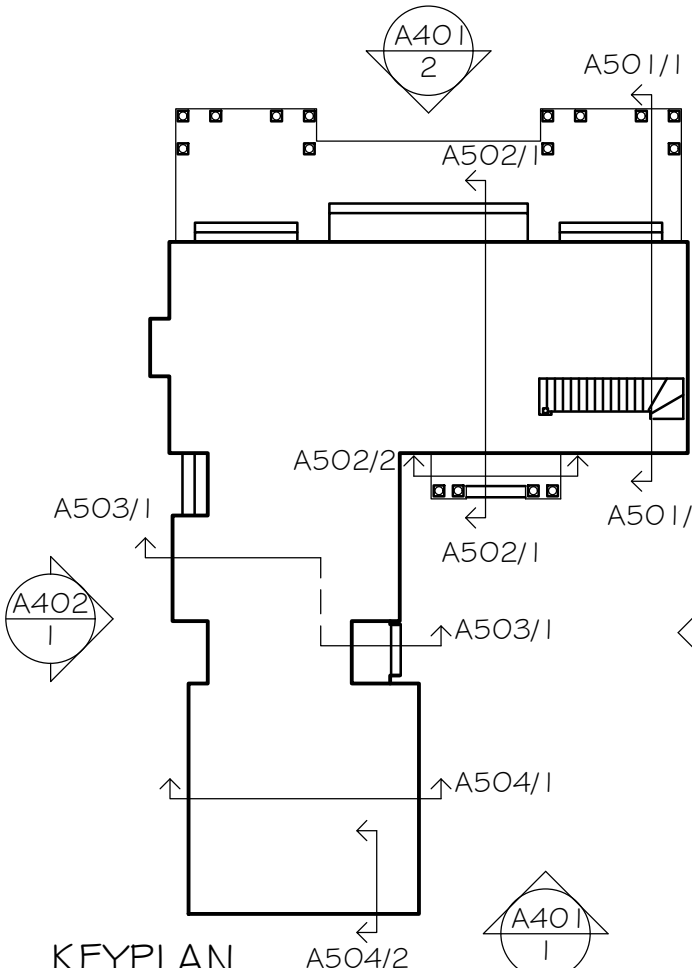

FL REG. AR95938  
NY REG. 031148

REVISIONS:

DATE:  
6/19/2019


SCALE:  
1/4" = 1'-0"

A-211


1st FLOOR PLAN



OPTION A

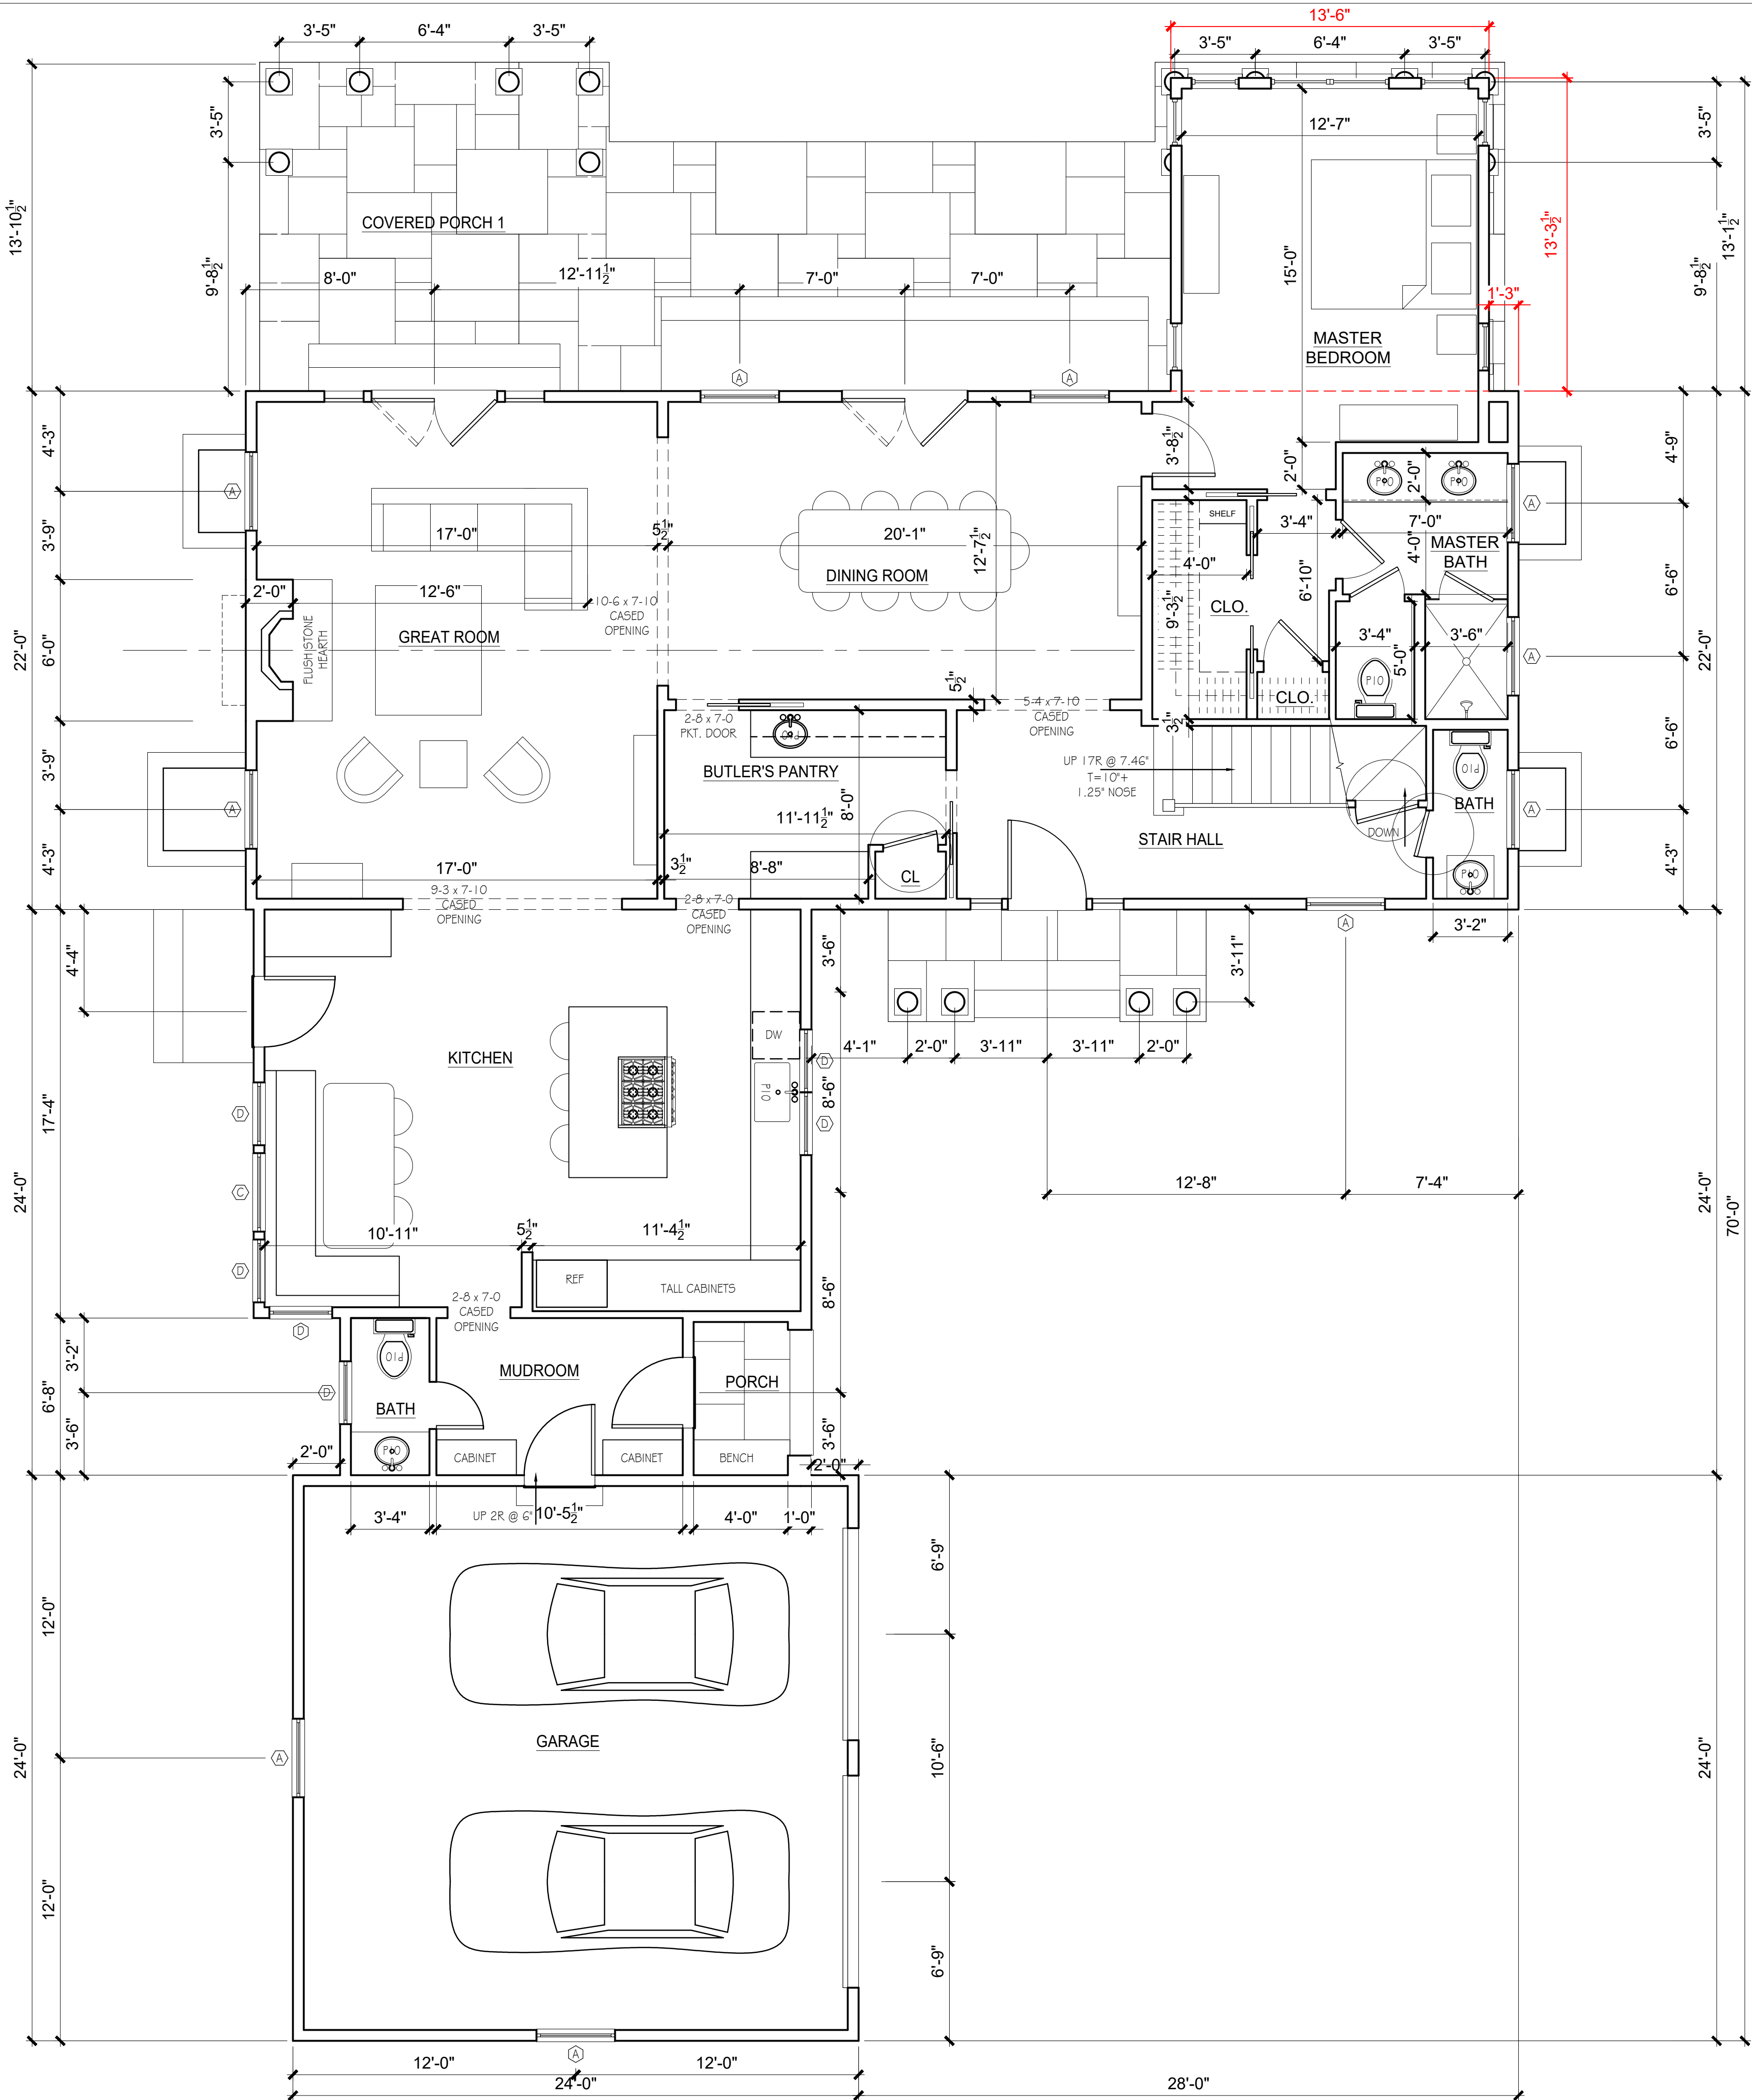

179 S.F. ADDED ON FIRST FLOOR  
1,008 S.F. REMOVED FROM SECOND FLOOR

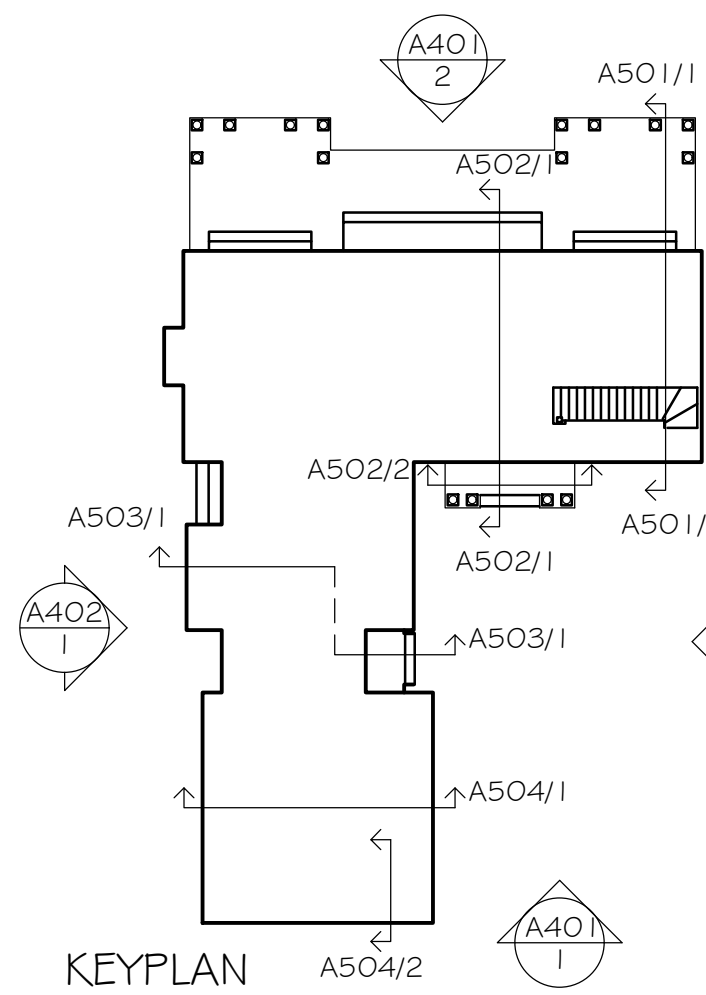

PROPOSED NEW CONSTRUCTION FOR:

CLIFTON CROSSING  
7 WARE LANE  
MARBLEHEAD, MA

FL REG. AR95938  
NY REG. 031148


REVISIONS:

DATE:  
6/19/2019  
SCALE:  
1/4" = 1'-0"


A-211  
1st FLOOR PLAN



OPTION B

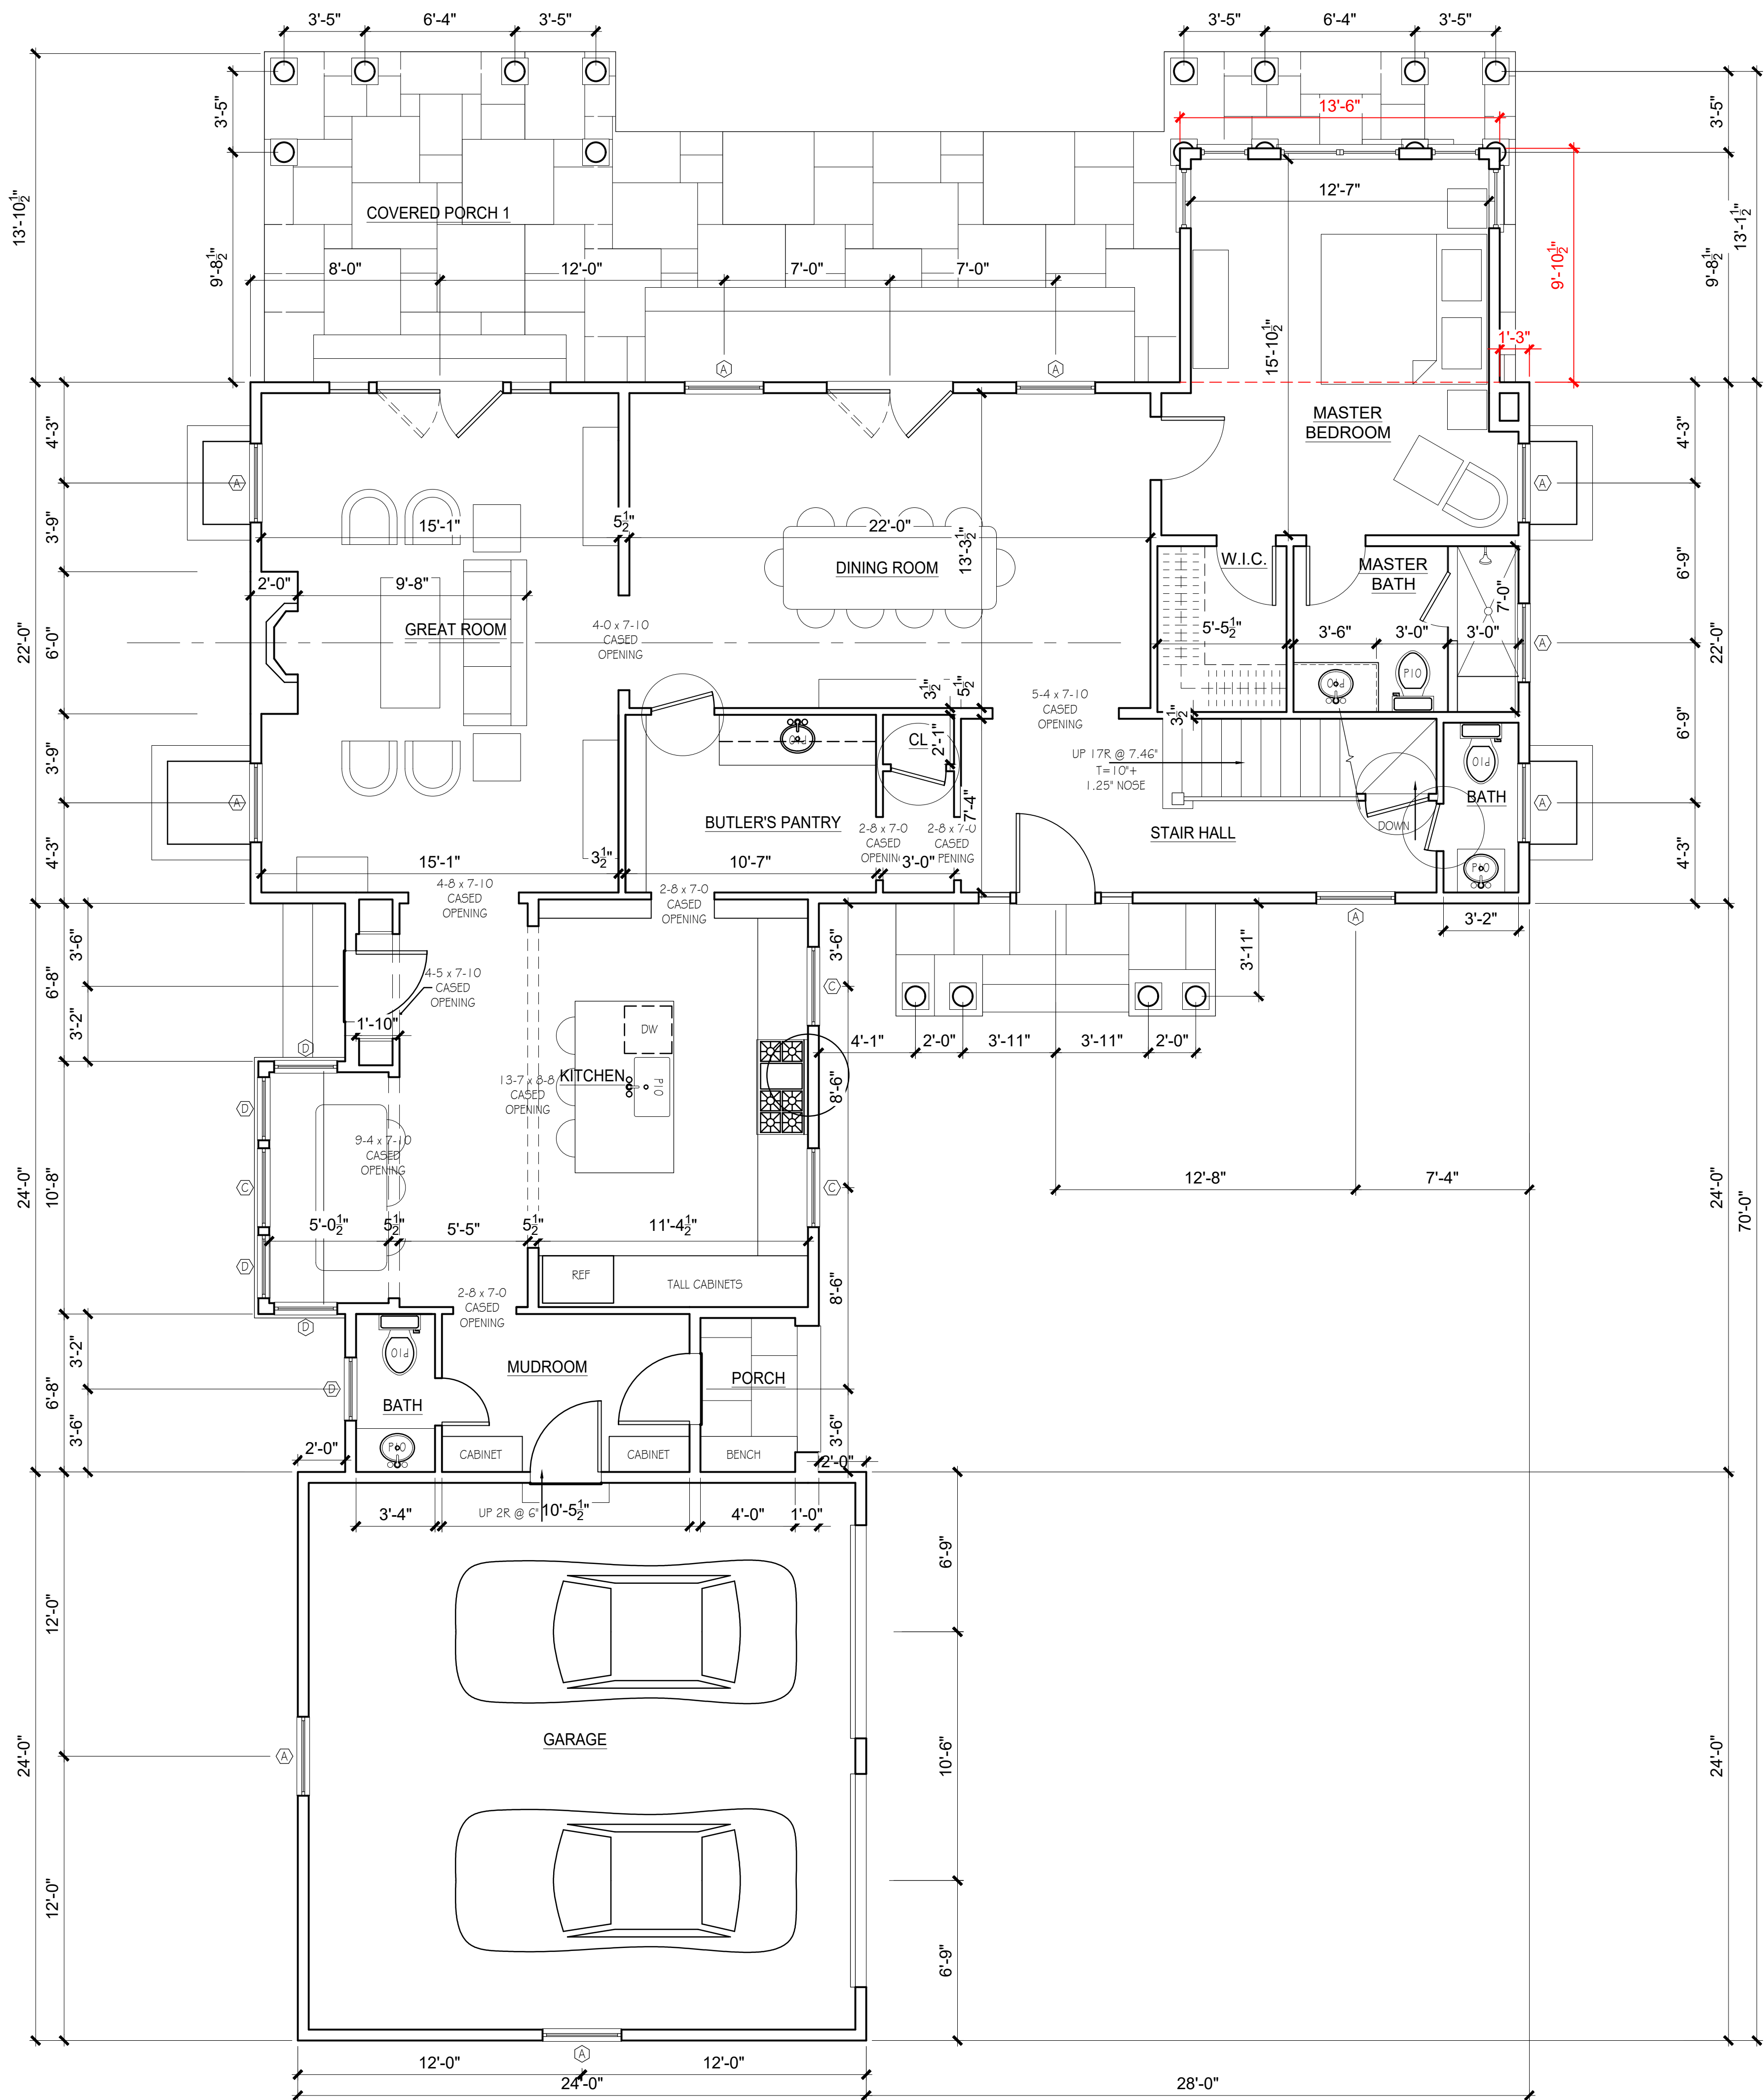

133 S.F. ADDED ON FIRST FLOOR  
1,008 S.F. REMOVED FROM SECOND FLOOR

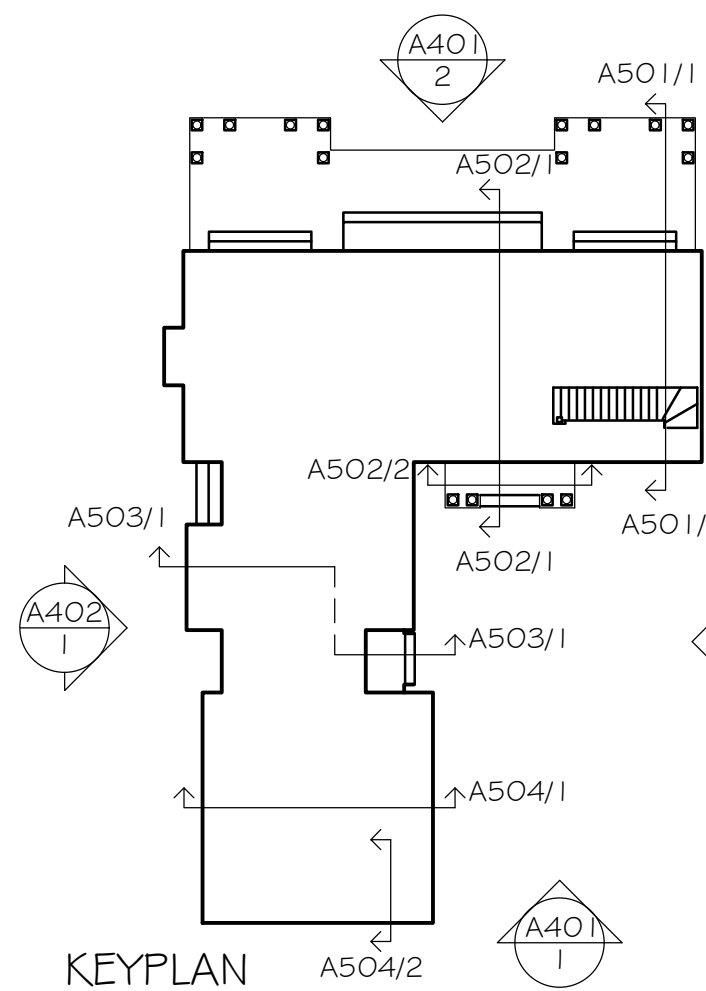

PROPOSED NEW CONSTRUCTION FOR:

CLIFTON CROSSING  
7 WARE LANE  
MARBLEHEAD, MA

FL REG. AR95938  
NY REG. 031148

REVISIONS:



DATE:  
6/19/2019  
SCALE:  
1/4" = 1'-0"

A-211

1st FLOOR PLAN



ORIGINAL  
SECOND  
FLOOR

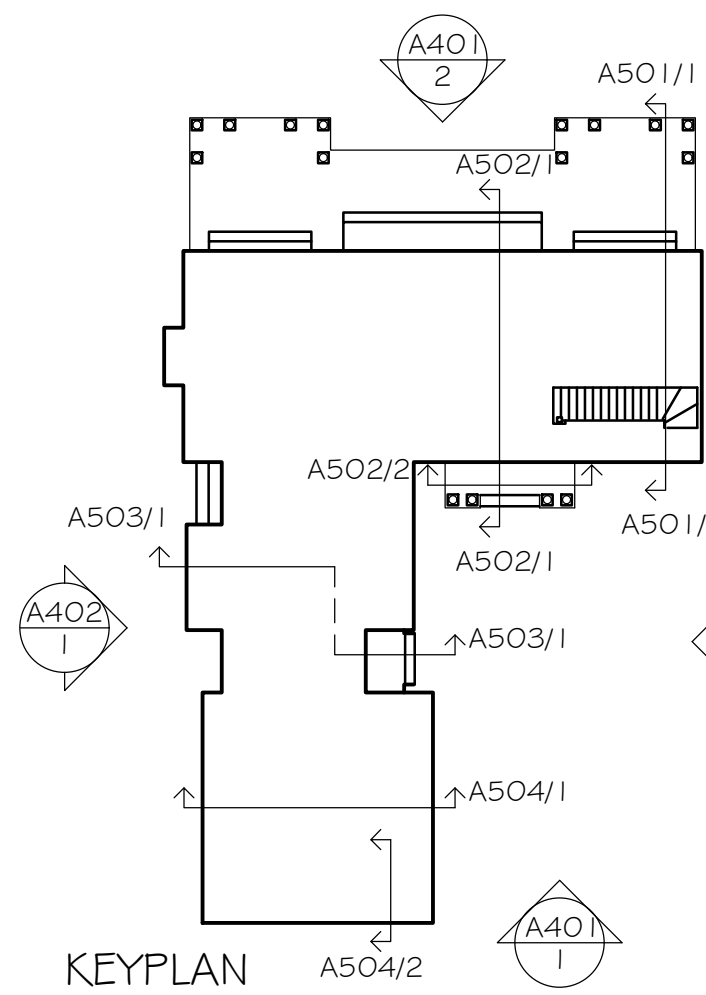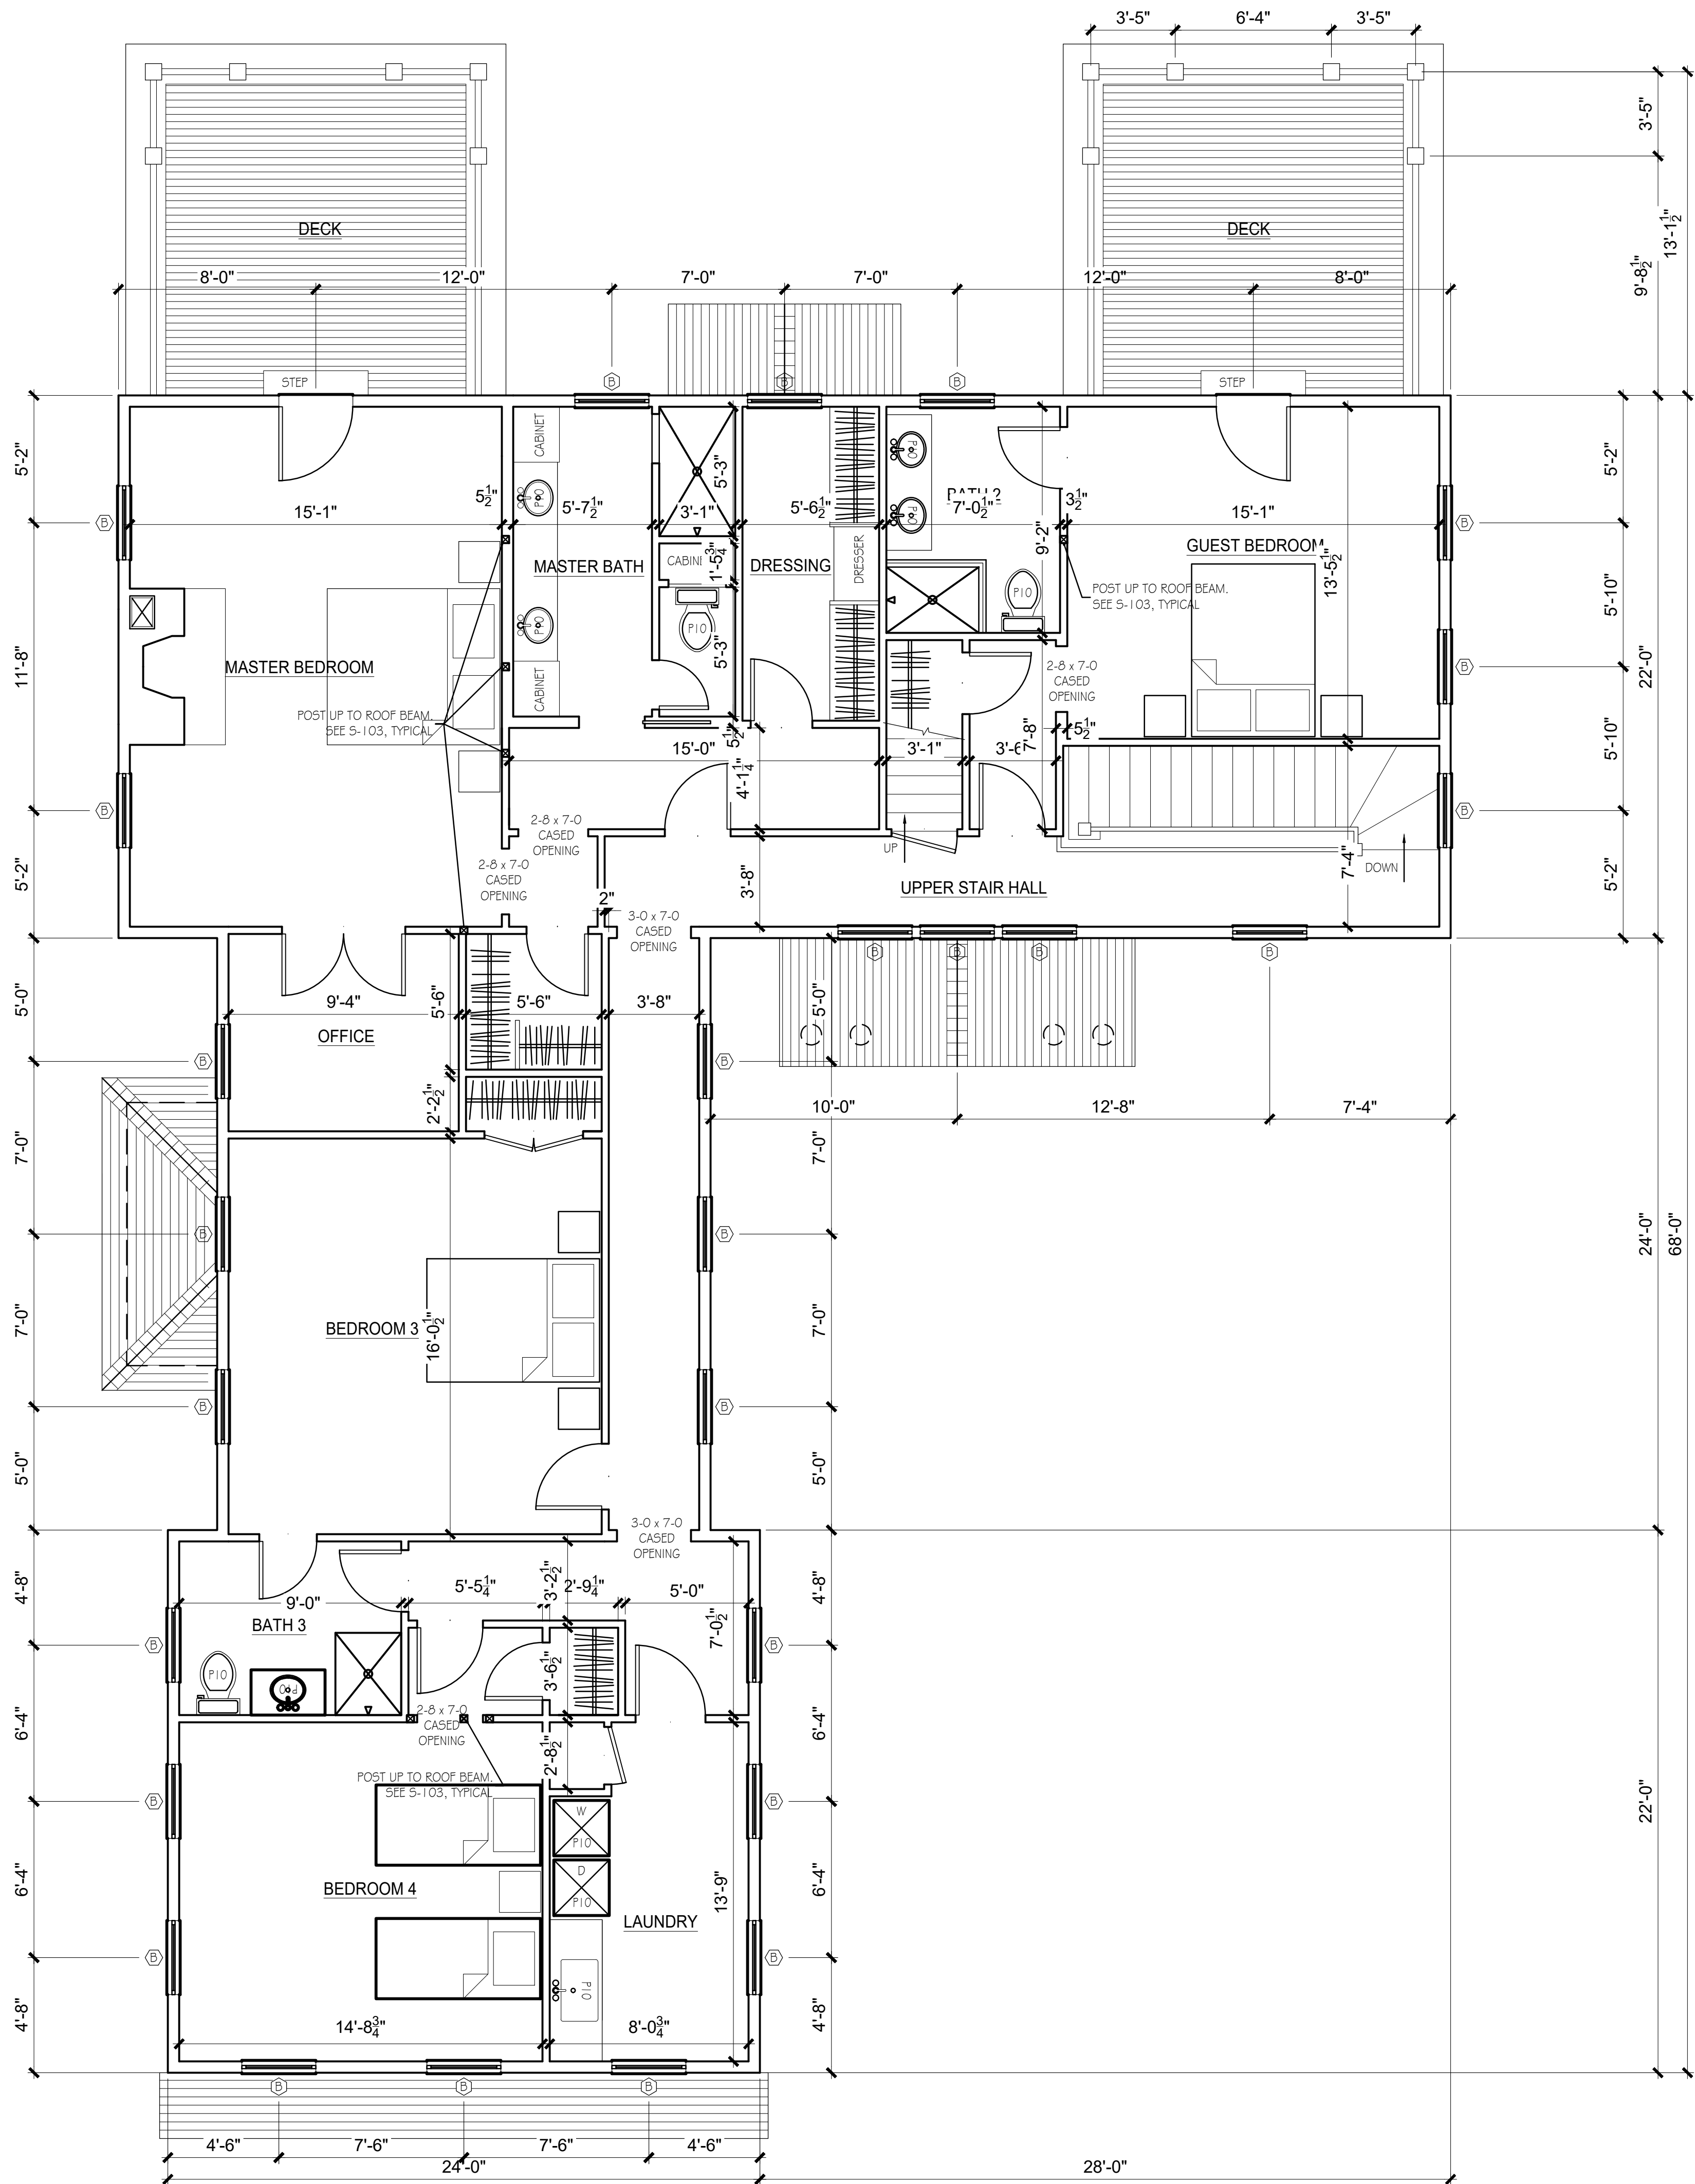

PROPOSED NEW CONSTRUCTION FOR:

CLIFTON CROSSING  
7 WARE LANE  
MARBLEHEAD, MA

FL REG. AR95938  
NY REG. 031148

REVISIONS:

DATE:  
6/19/2019  
SCALE:  
1/4" = 1'-0"


A-221

2nd FLOOR PLAN


917 647-2039



UPDATED  
SECOND  
FLOOR

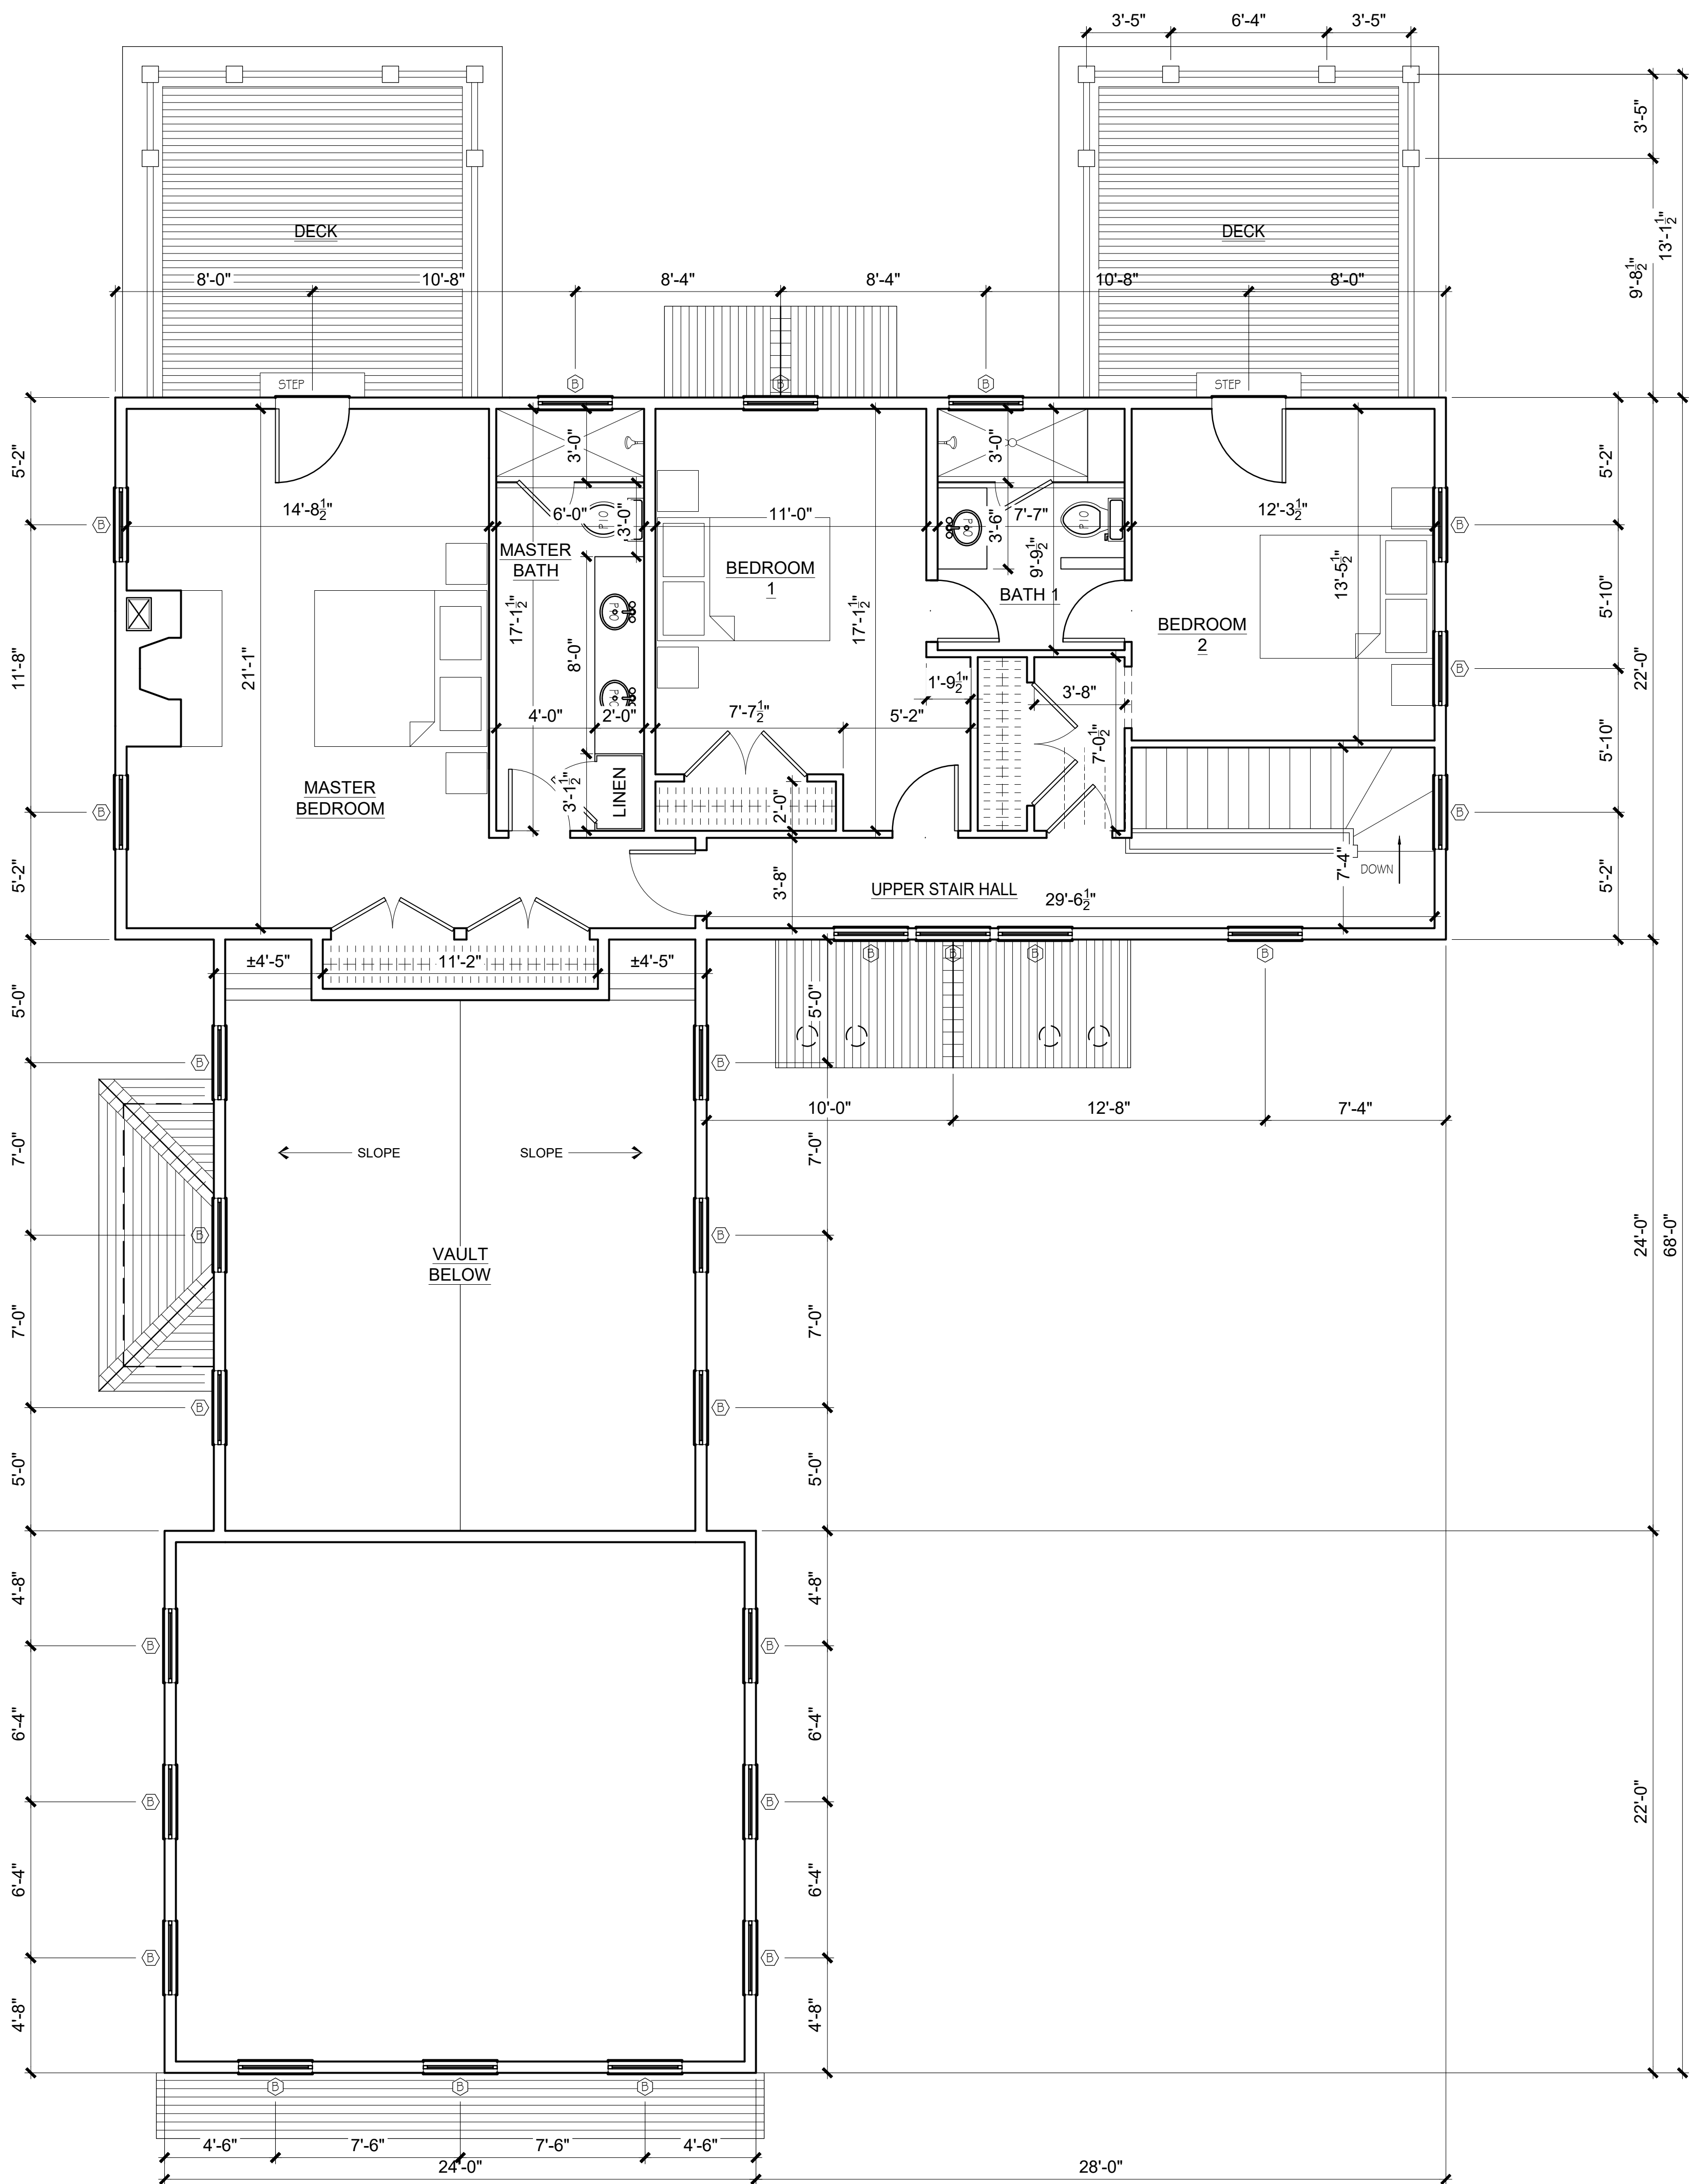

1,008 S.F. REMOVED FROM SECOND FLOOR

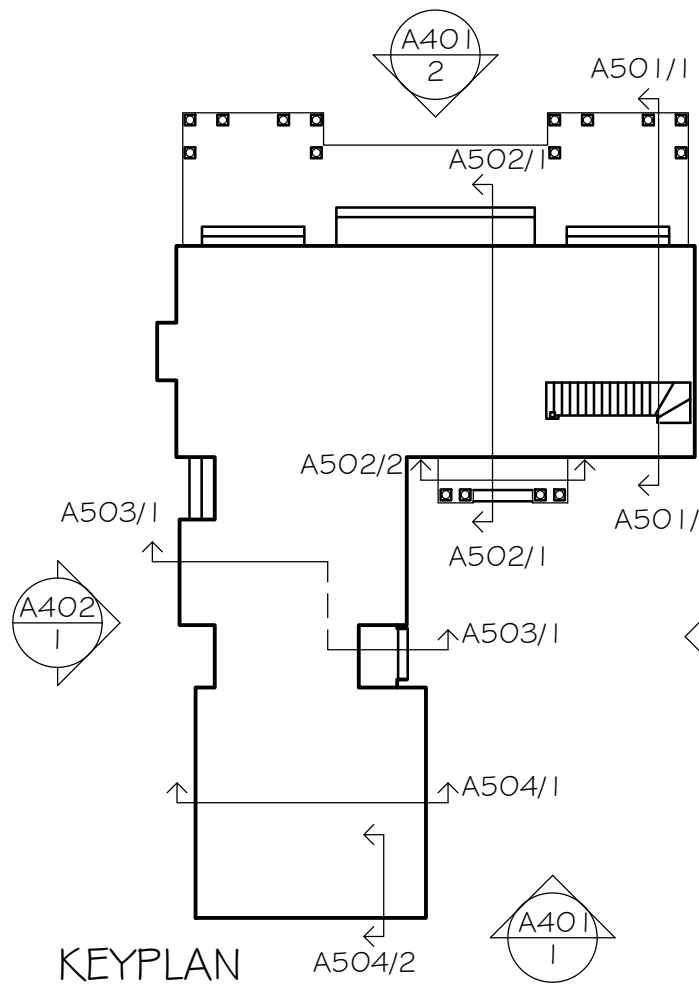

PROPOSED NEW CONSTRUCTION FOR:

CLIFTON CROSSING  
7 WARE LANE  
MARBLEHEAD, MA

FL REG. AR95938  
NY REG. 031148

REVISIONS:

DATE:  
6/19/2019  
SCALE:  
1/4" = 1'-0"

A-221  
2nd FLOOR PLAN